

Дизайн проект

(рабочий проект)



DE-Club

Авторский коллектив:

Архитектор
ГАП
ГИП
Заказчик

Состав проекта

№ п/п	Наименование чертежа.	Марка
1	Титульный лист	P-1
2	Состав проекта	P-2
3	Обмерный план	P-3
4	План демонтажа	P-4
5	План монтажа	P-5
6	Виды 1, 2, 3, А, Б, В, Г	P-6
7	Виды 4, 5	P-7
8	Виды 6, 7	P-8
9	Виды 8, 9, 10, 11	P-9
10	План после перепланировки (только для смет)	P-10
11	Спецификация дверных проёмов	P-11
12	План пола	P-12
13	Экспликация полов	P-13
14	План теплых полов	P-14
15	План расстановки сантехники	P-15
16	План раскладки плитки по полу	P-16
17	План раскладки плитки в с/у 1	P-17
18	План раскладки плитки в с/у 2	P-18
19	План потолка	P-19
20	Лекальные линии потолка в помещении №10	P-20
21	Разрезы потолка 1-1; 2-2;	P-21
22	Разрезы потолка 3-3; 4-4; 5-5; 6-6;	P-22
23	Разрезы потолка 7-7; 8-8; 11-11;	P-23
24	Разрезы потолка 9-9; 10-10;	P-24
25	План расстановки светильников	P-25
26	План расстановки выключателей	P-26
27	План расположения электроточек силовых и слаботочных	P-27
28	Компоновка внешней электрофурнитуры	P-28
29	План мебели	P-29
30	План отделки	P-30
31	Ведомость отделки 1	P-31
32	Ведомость отделки 2	P-32
33	Приложение 1	P-33
34	Приложение 2	P-34

Пояснительная записка

Дизайн-проект квартиры общей площадью 142,3 м² (без отделки) разработан на основе технического задания, утвержденного с заказчиком. Квартира предназначена для проживания 4-х человек: Родители и 2 дочки. Необходимо было увеличить количество комнат, при этом не объединять гостиную с кухней. Так же, Мы увеличили зону гостевого санузла за счет холла, при этом не затрагивая несущих конструкций. Этого достигли путем пристройки к с/у зоны постирочной, где аккуратно спрятали стиральную машину, гладильную доску и сушку для белья. Т.к. перед архитектором, в большей степени, стояла задача достичь максимальной функциональности, планировка получилась достаточно строгая. Геометрия в рисунке и потолках добавили ей сложности. Основой стилевого решения явилось желание иметь современный спокойный, холодный интерьер с элементами отделанными современными отделочными материалами. Архитектором была предложена идея оттолкнуться от дизайнера напольной плитки. Она и стала отправной точкой в колорите гостиной и холла. Таким образом, соединив все эти пожелания по цвету, фактуре и формам, родился очень стильный образ квартиры. Холодный колорит холла и гостиной смягчает плитка, которая используется как на полу холла и балкона так и на стенах гостиной. Витражи, так же поддерживают лейтмотив квартиры завязанный на плитке. Строгость придают конструктивные элементы оттеланые декоративной штукатуркой с ярковыраженной фактурой сего цвета. Во всех помещениях правит геометрия. линии пола переходящие в стены и на потолок разрывают пространство, делая его интересным и необычным.


Согласовано

Изв. № подп. Подл. и дата
Взам. инд. №

							Заказчик:		
Изм.	Кол.уч	Лист	№ док	Подп.	Дата	Разработал			
ГАП						ГИП			
Чертил						Дата изменения			
Заказчик						Состав проекта			
							Стадия	Лист	Листов
							P	2	34

Обмерный план

Высота потолка - 2955 мм. Общая площадь - 142.27 кв.м

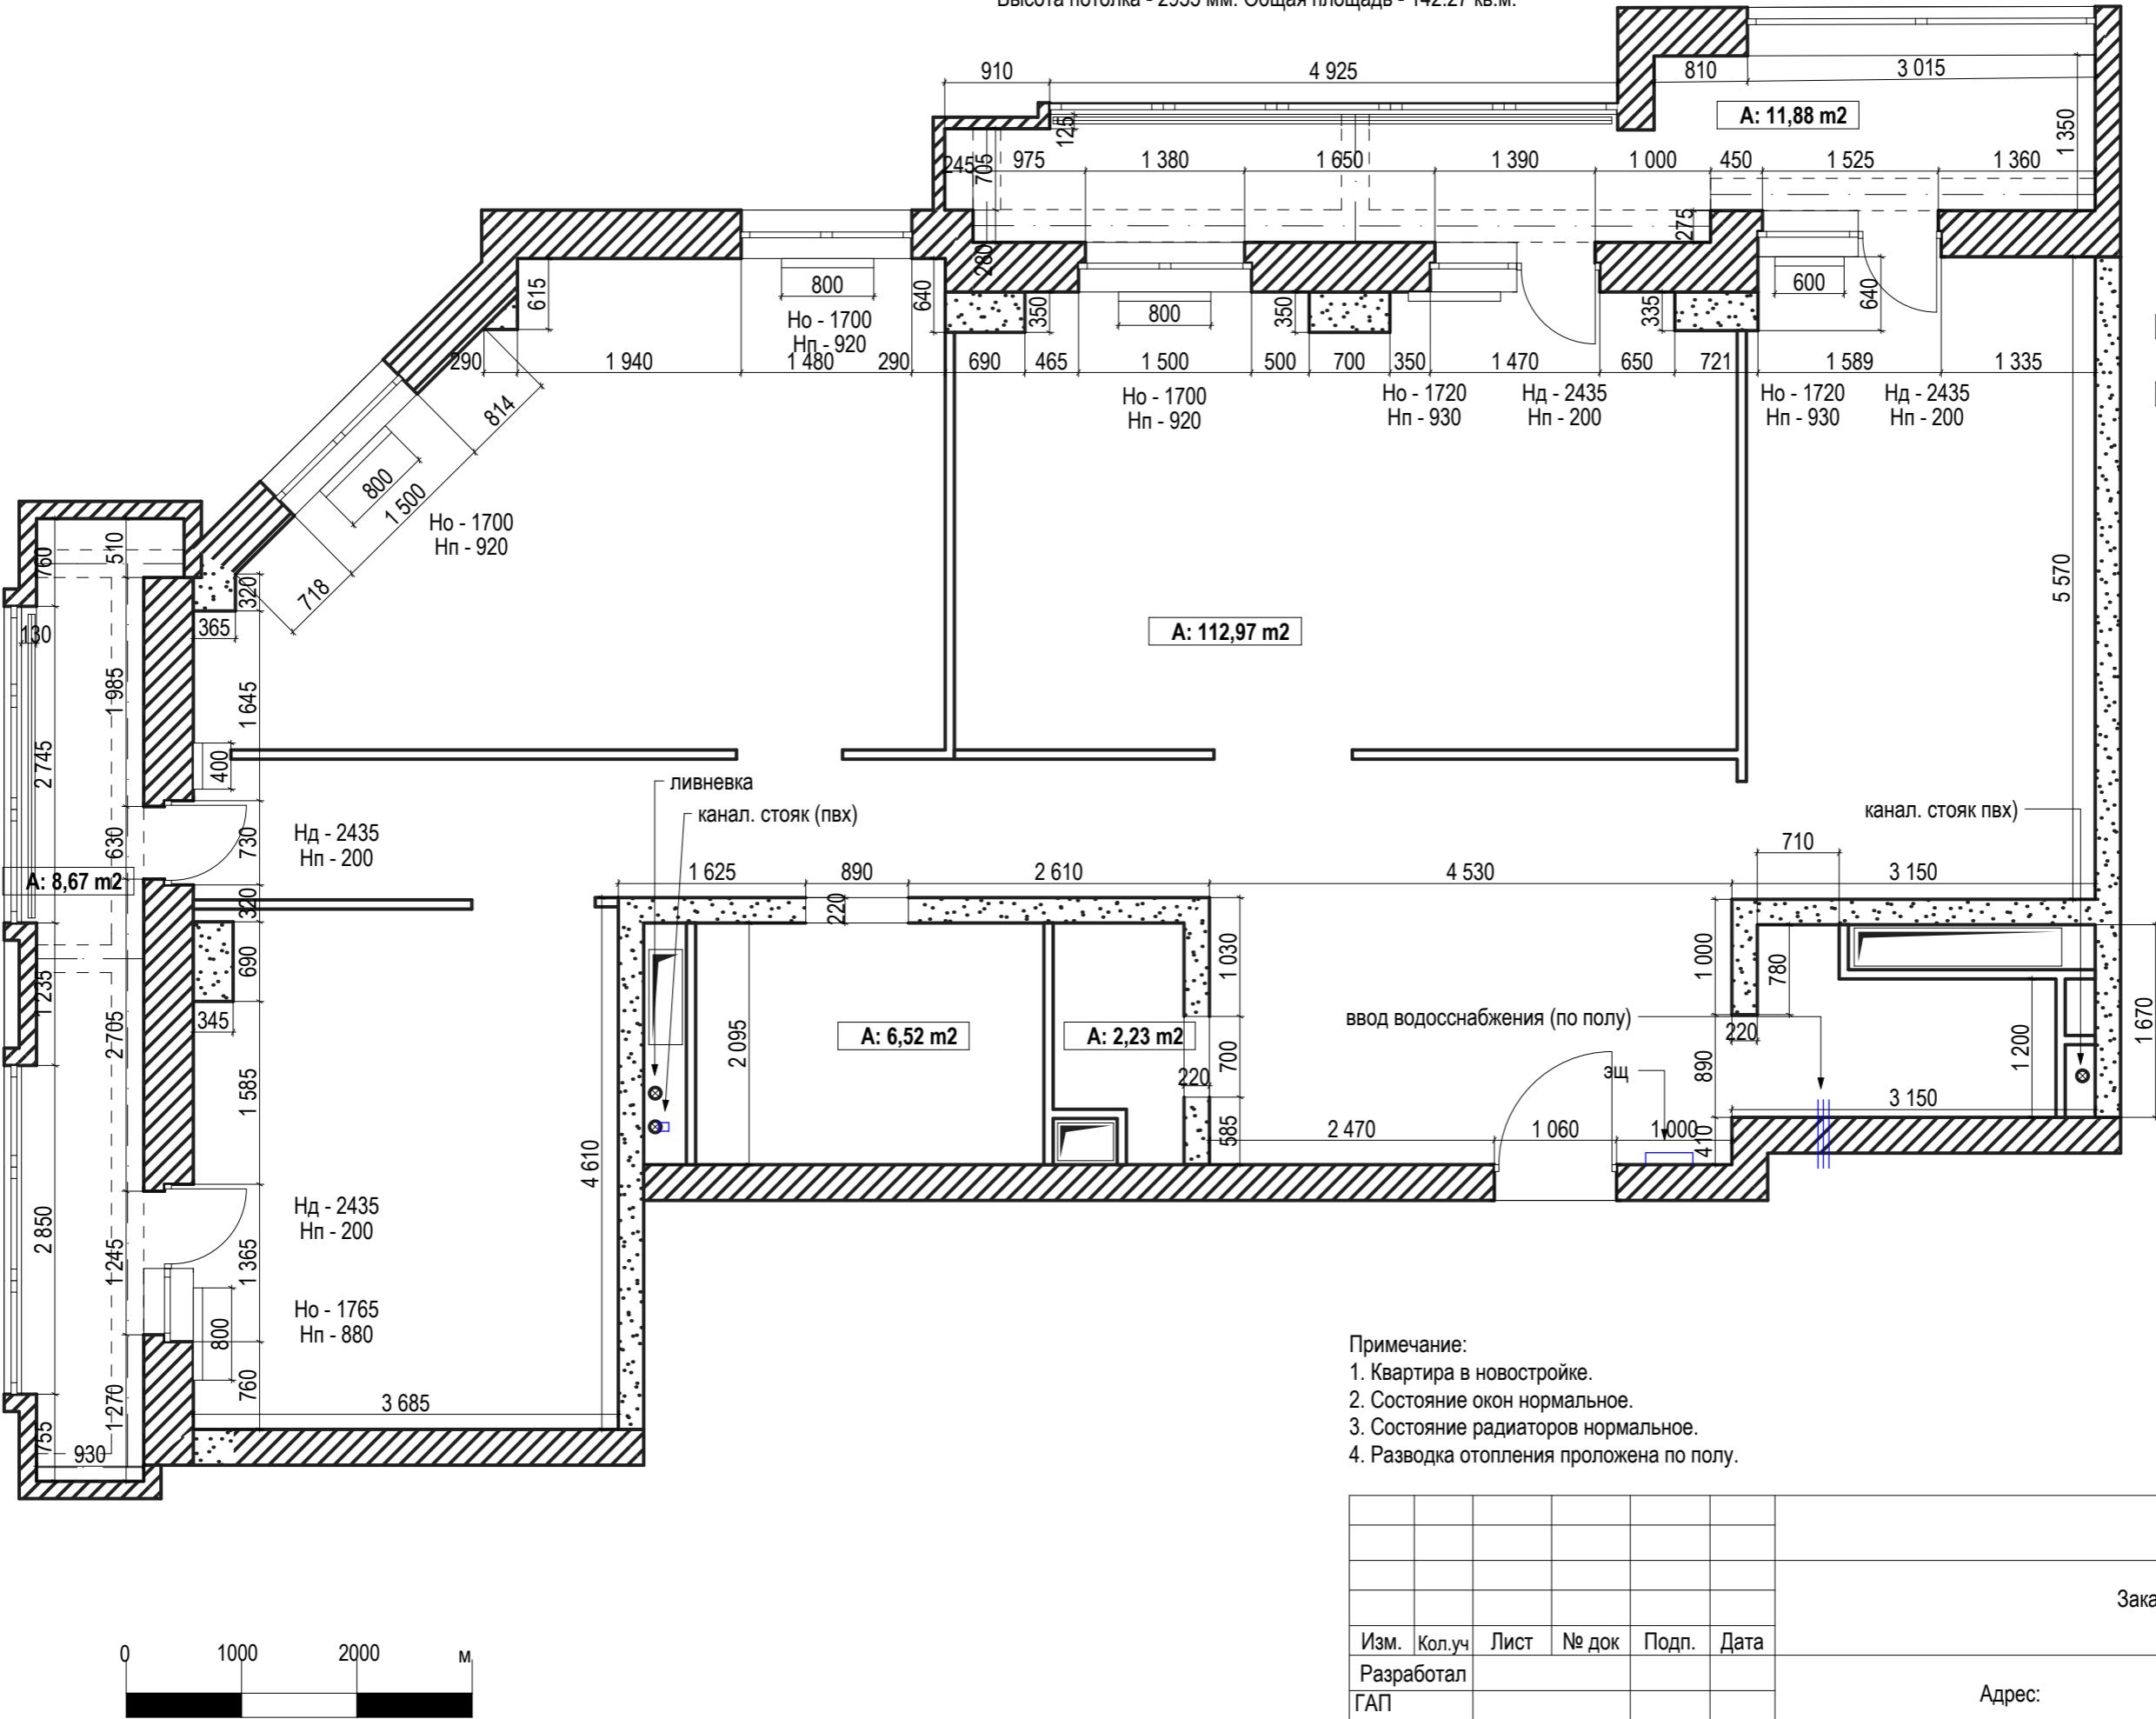


Примечание:

1. Квартира в новостройке.
2. Состояние окон нормальное.
3. Состояние радиаторов нормальное.
4. Разводка отопления проложена по полу

План демонтажа

Высота потолка - 2955 мм. Общая площадь - 142.27 кв.м.

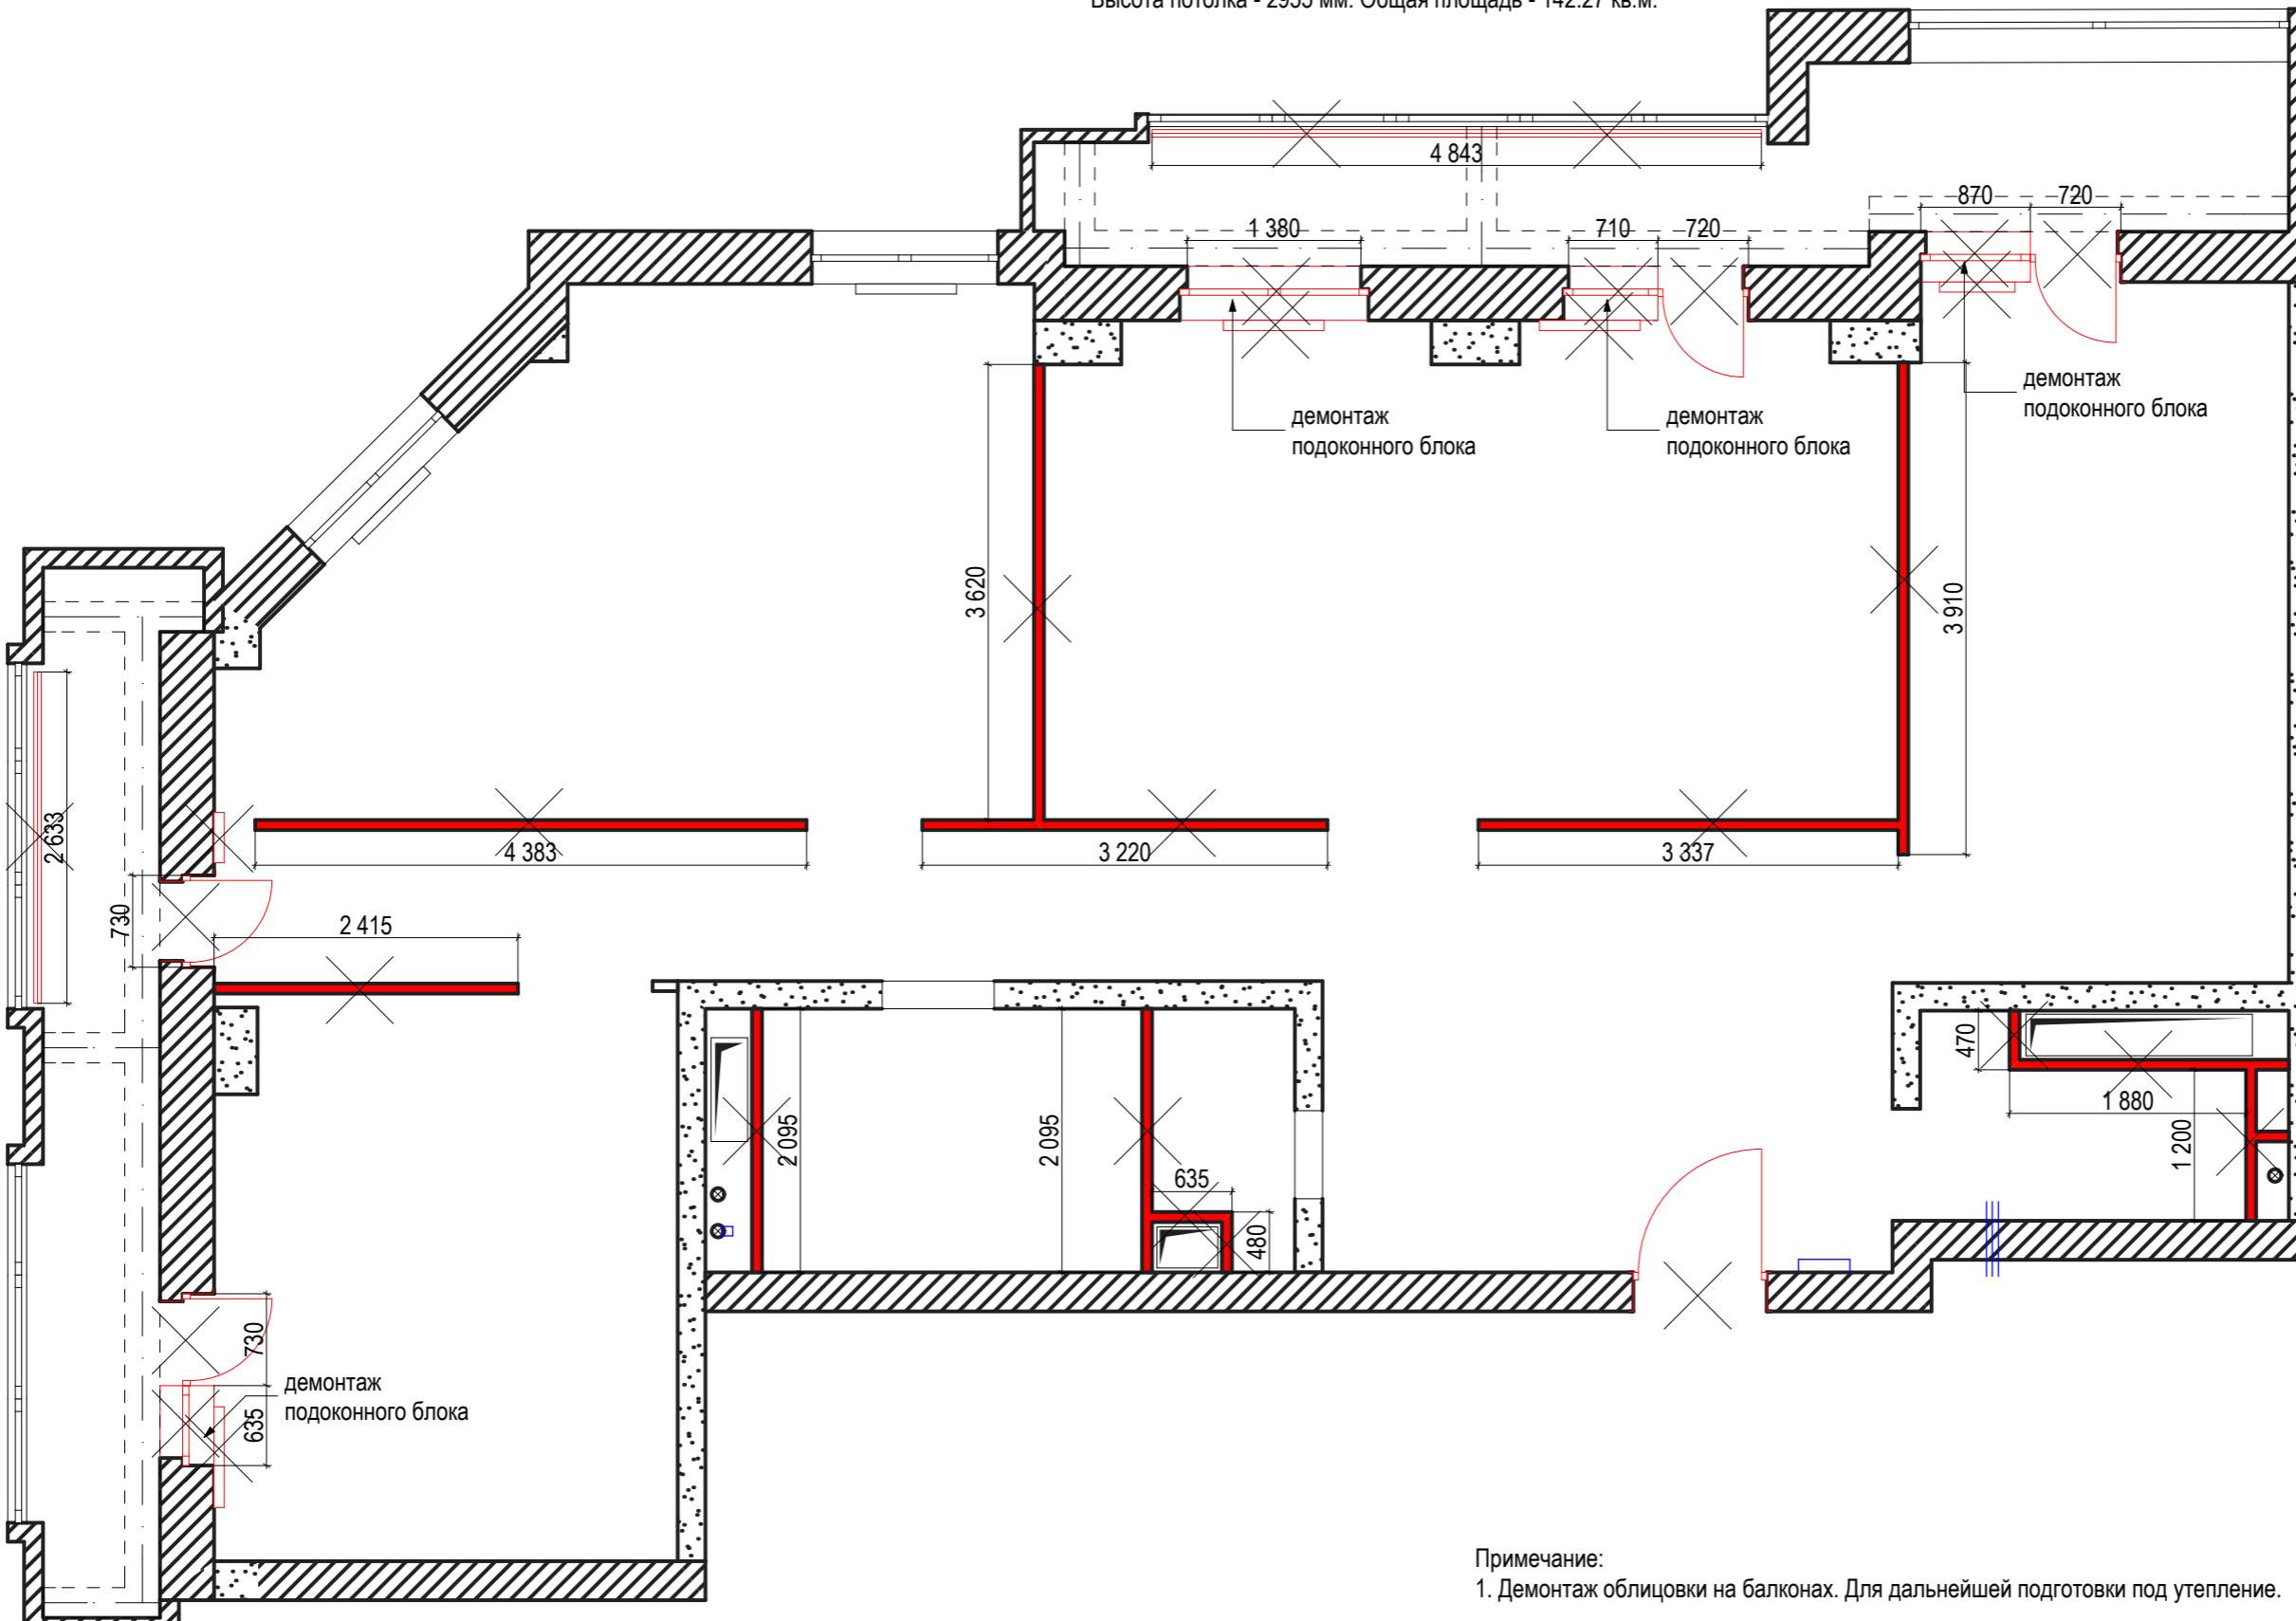




Примечание:
1. Демонтаж облицовки на балконах. Для дальнейшей подготовки под утепление.

Инв. № подп.	Подп. и дата	Взам. инд. №	Заказчик:	Стадия	Лист	Листов
Изм.	Кол.уч	Лист	№ док	Подп.	Дата	
Разработал						
ГАП						
ГИП						
Чертит						
Дата изменения						
Заказчик						



План демонтажа

Виды 1, 2, 3, А, Б, В, Г

Высота потолка - 2955 мм. Общая площадь - 141.24 кв.м.

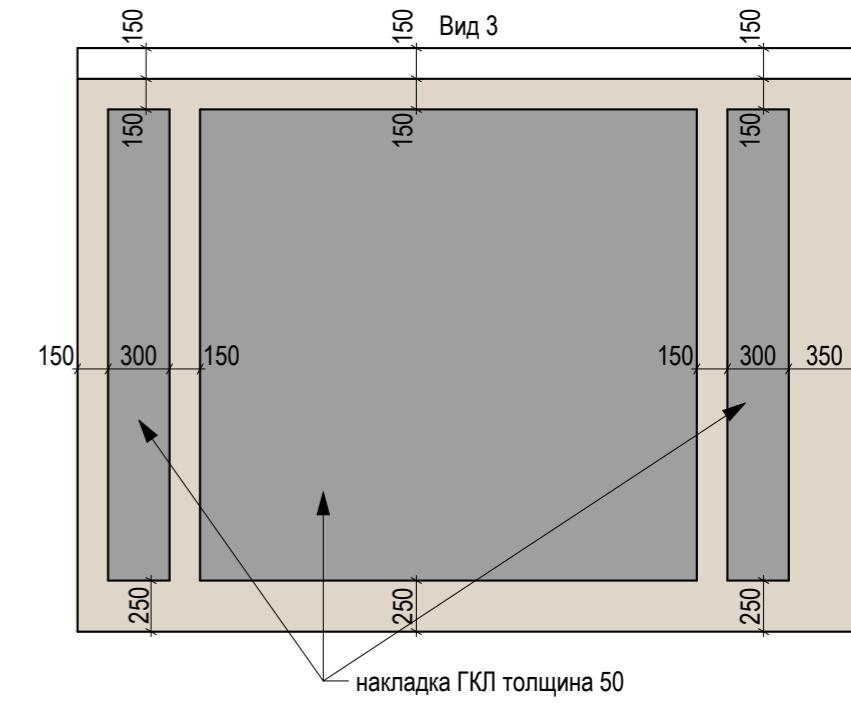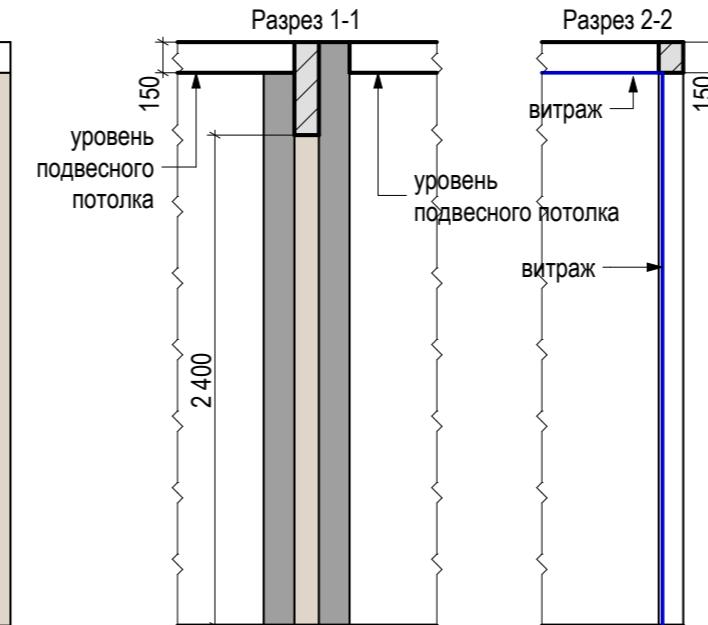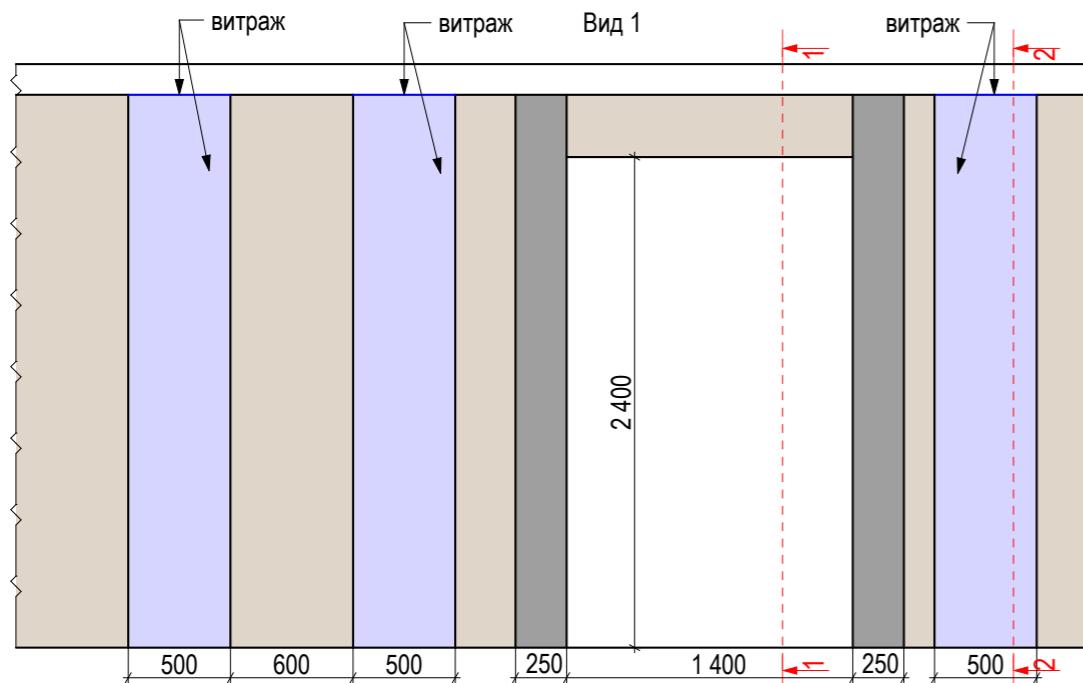

Вид 2

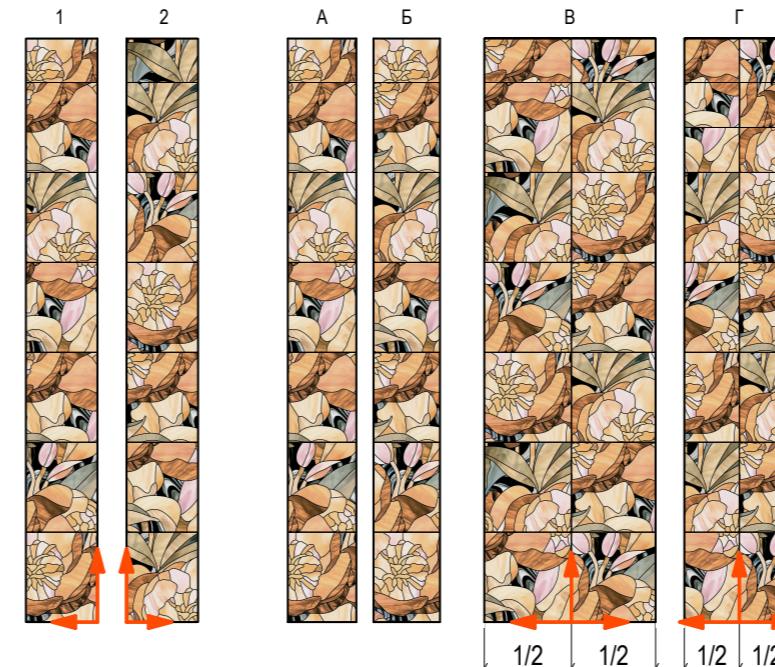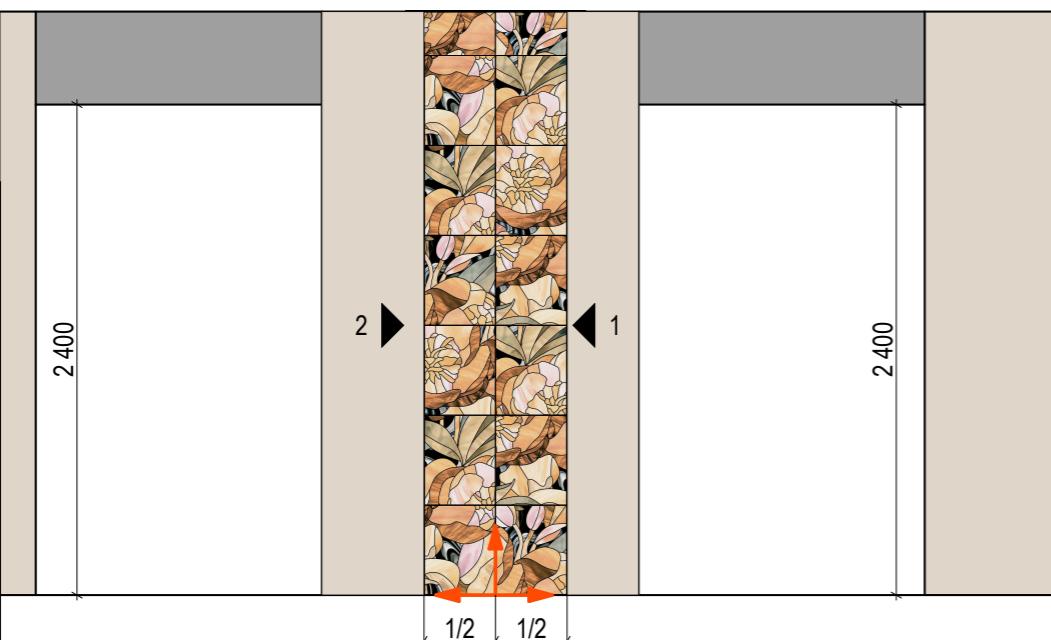

Условные обозначения:
Ф-ка Peronda кол-я Candela

- | | | |
|--|--|--------|
| | Керамогранит CANDELA/44/P размер 440x440 | 70 шт. |
| | Декоративное покрытие 1 | |
| | Декоративное покрытие 2 | |
| | Витраж | |
| | Направление раскладки | |

Примечания:

1. Количество плитки дано без учёта на скол и подрезку.
2. Плитка и керамогранит, шов минимальный.
3. Затирку шва подобрать в цвет плитки.
4. Магазин, плитка:

Изм.	Кол.уч	Лист	№ док	Подп.	Дата
Разработал					
ГАП					
ГИП					
Чертил					
Дата изменения					
Заказчик					

Заказчик:

Адрес:	Стадия	Лист	Листов
	P	6	34

Виды 1, 2, 3, А, Б, В, Г




Согласовано			

Инв. № подп.	Подп. и дата	Взам. инд. №	


0 1000 2000 м

Виды 4, 5

Высота потолка - 2955 мм. Общая площадь - 141.24 кв.м.

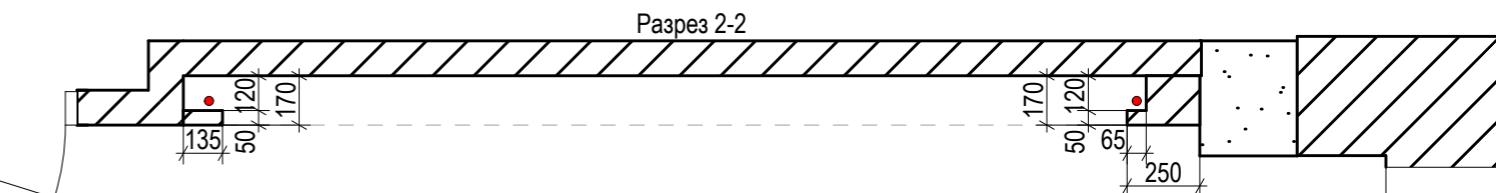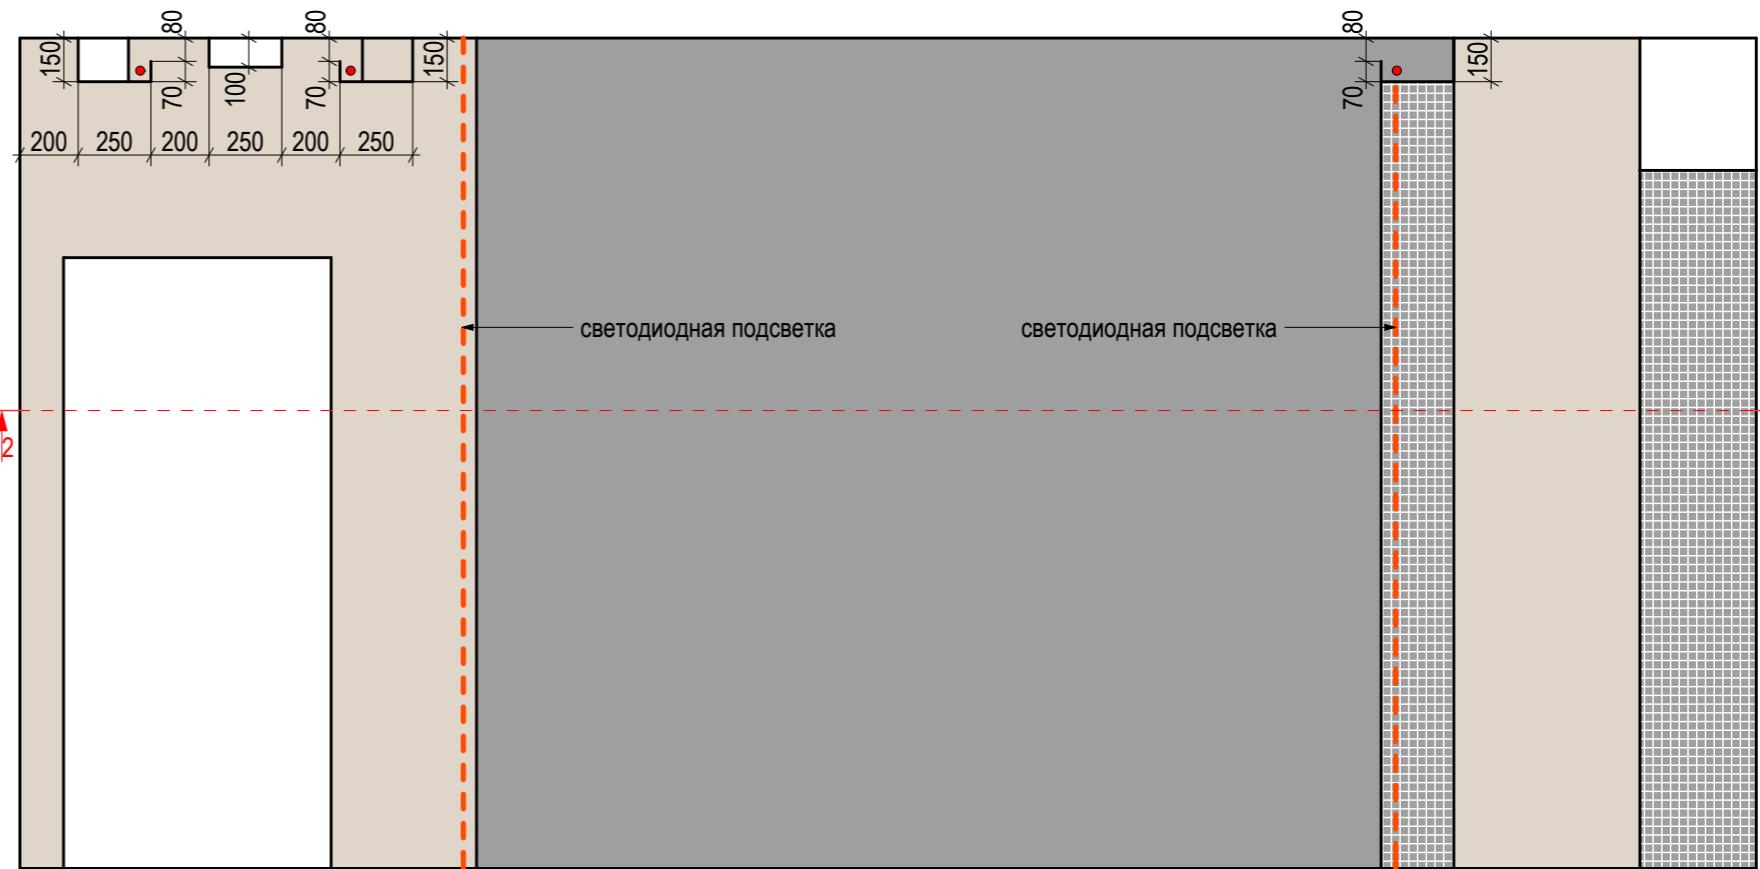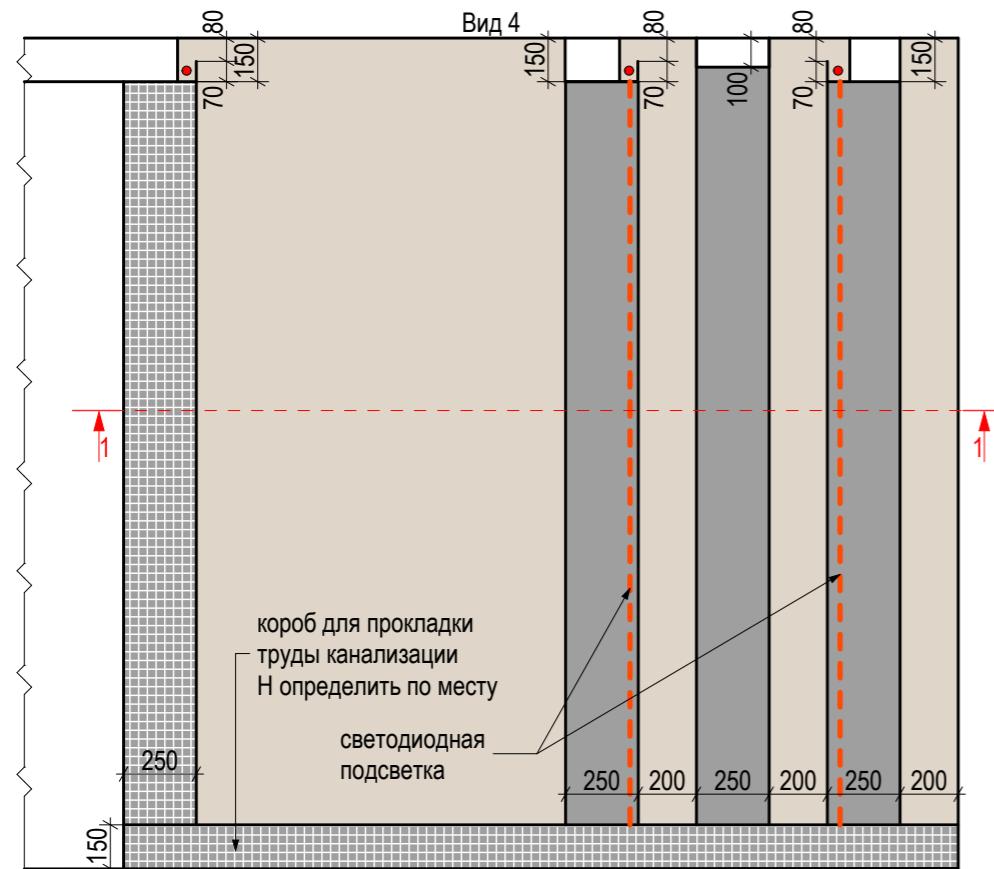

Условные обозначения:

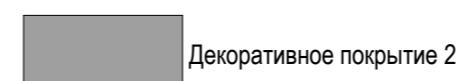

Мозаика Dune 184330 2.5X2.5 VITRA MOSAICO PLATINO BRILL D910 290x290 3,31 м²

Светодиодная лента

Примечания:

- Затирку шва подобрать в цвет плитки.
- Магазин, плитка:

Изм.	Кол.уч	Лист	№ док	Подп.	Дата
Разработал					
ГАП					
ГИП					
Чертит					
дата изменения					
Заказчик					

Заказчик:

Адрес:

Стадия Лист Листов
Р 7 34

Виды 4, 5

Согласовано



Инв.№ подп.	Подп. и дата	Взам. инд.№
-------------	--------------	-------------



М

Виды 6, 7

Высота потолка - 2955 мм. Общая площадь - 141.24 кв.м.

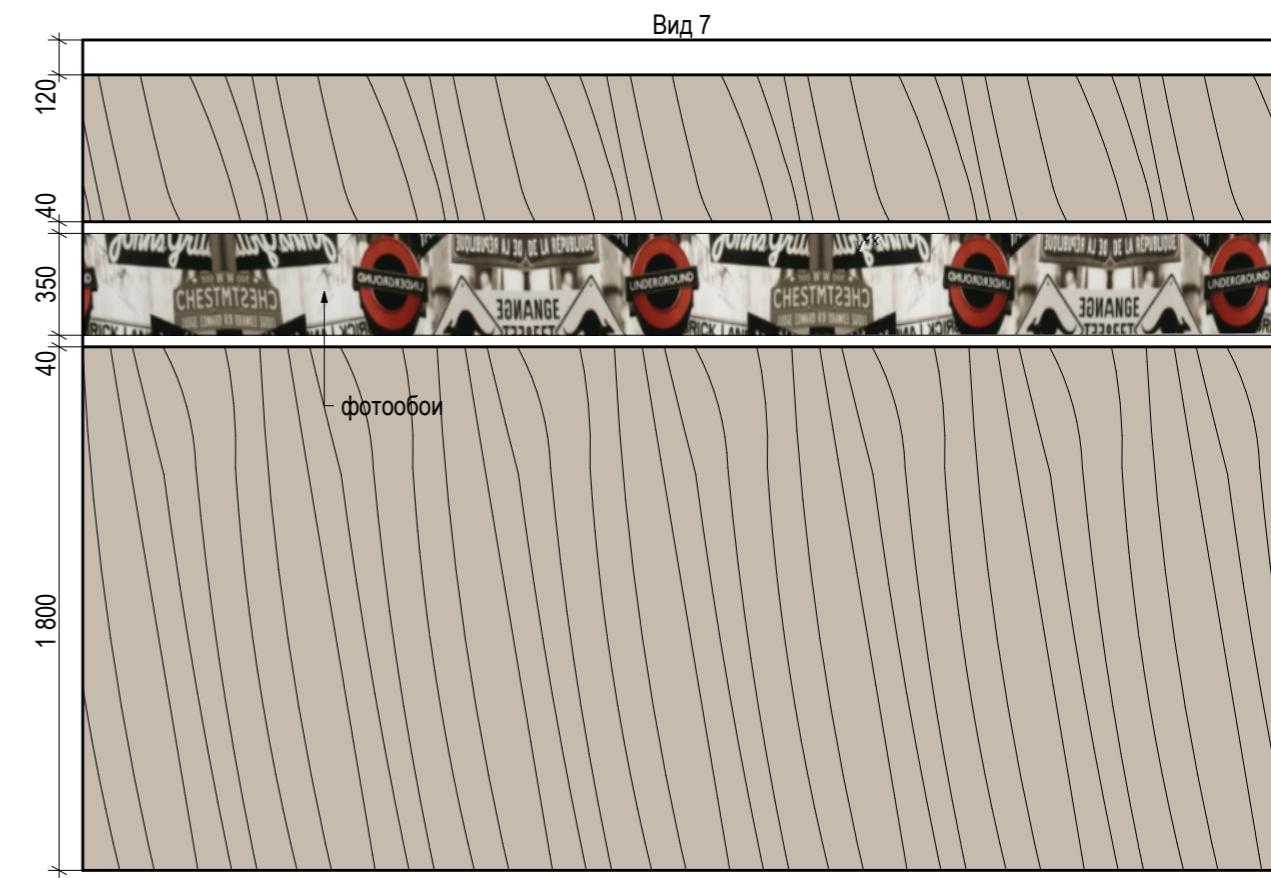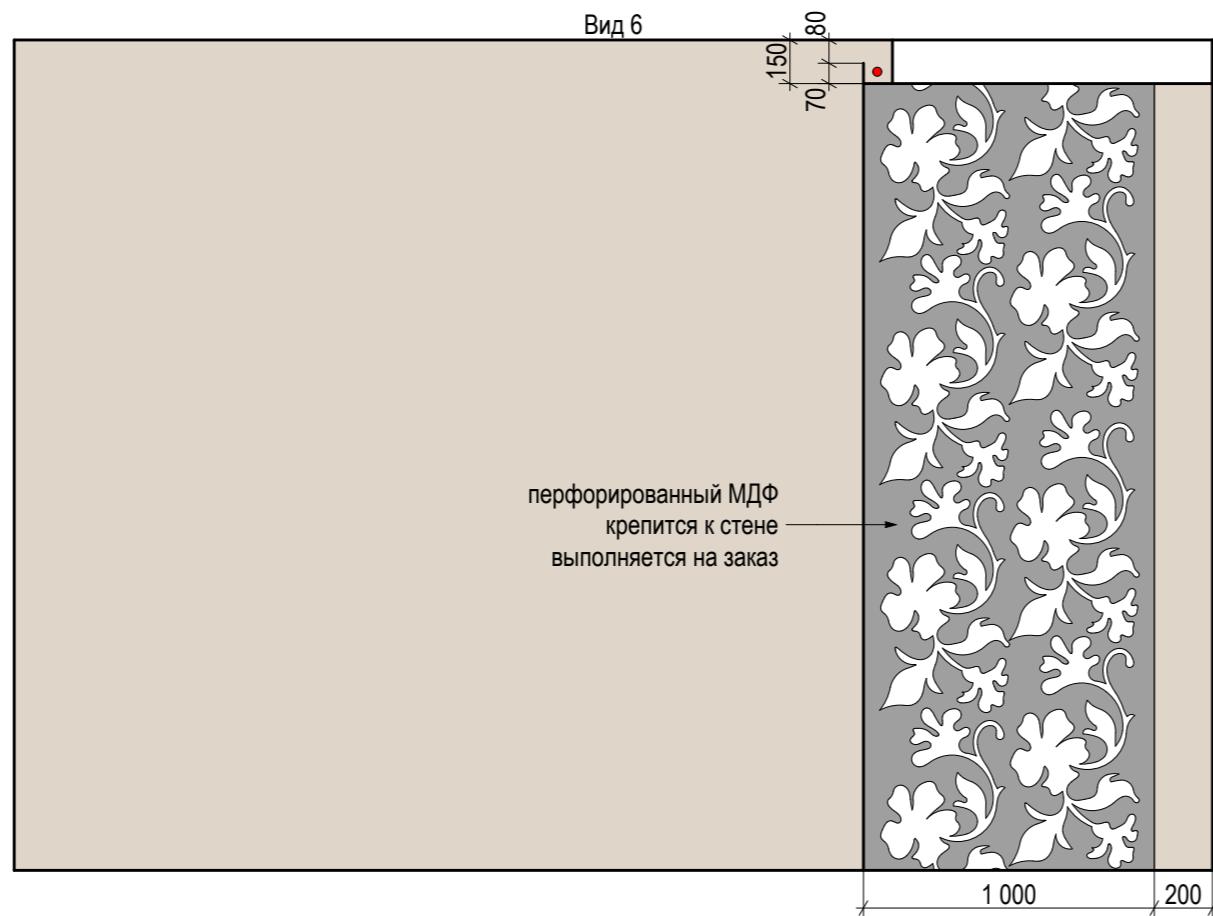

Условные обозначения:



Инженерная доска FINEX/Фиоччи/185x500/2400x16



Декоративное покрытие 2



Фотообои



Светодiodная лента

Примечания:

1. Магазин, инженерная доска:

Заказчик:					
Адрес:			Стадия	Лист	Листов
	P	8			34
Виды 6, 7					
Изм.	Кол.уч	Лист	№ док	Подп.	Дата
Разработал					
ГАП					
ГИП					
Чертит					
Дата изменения					
Заказчик					





Согласовано

Инв.№ подп.	Подп. и дата	Взам. инд.№
-------------	--------------	-------------



Виды 8, 9, 10, 11

Высота потолка - 2955 мм. Общая площадь - 141.24 кв.м.

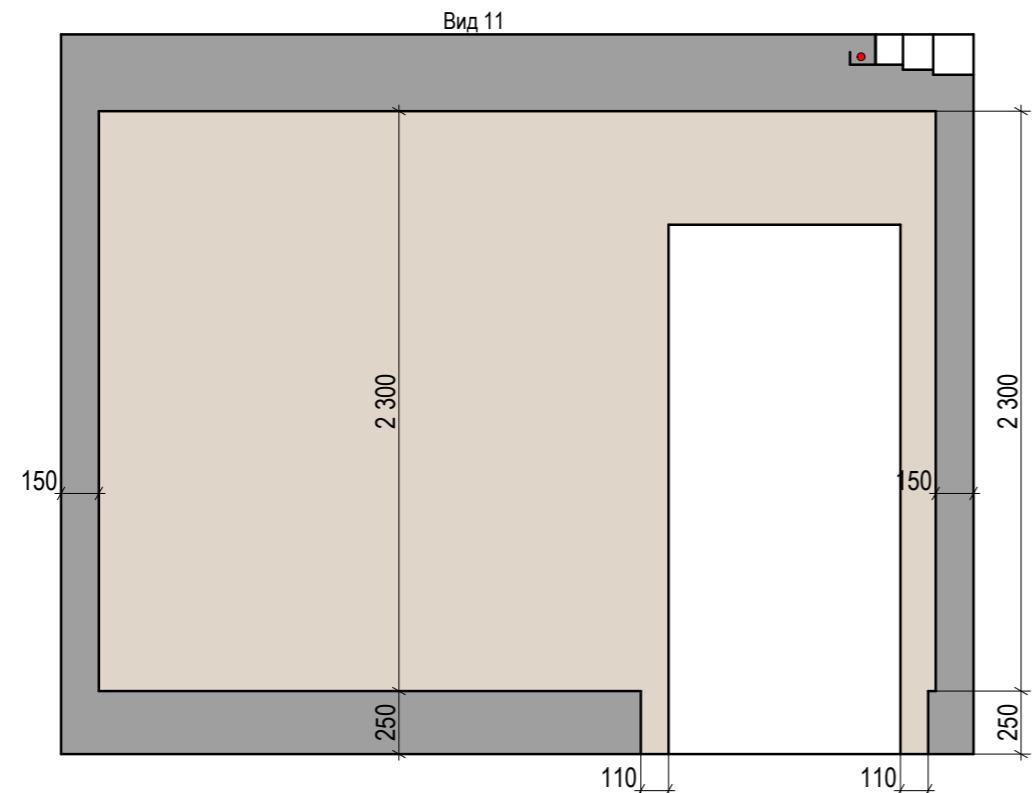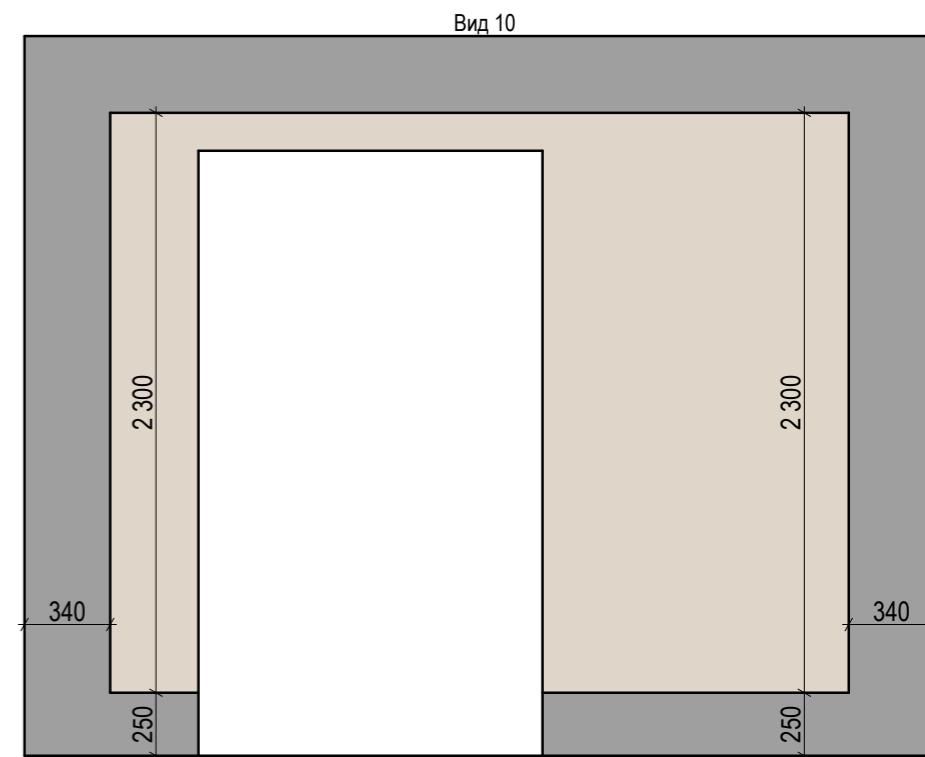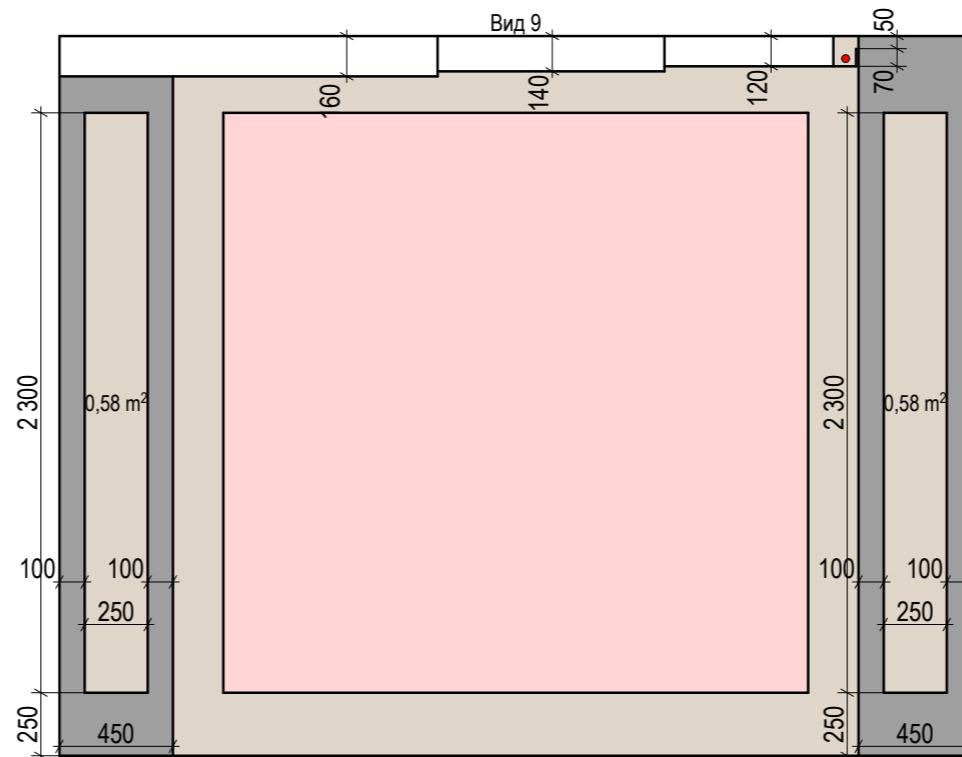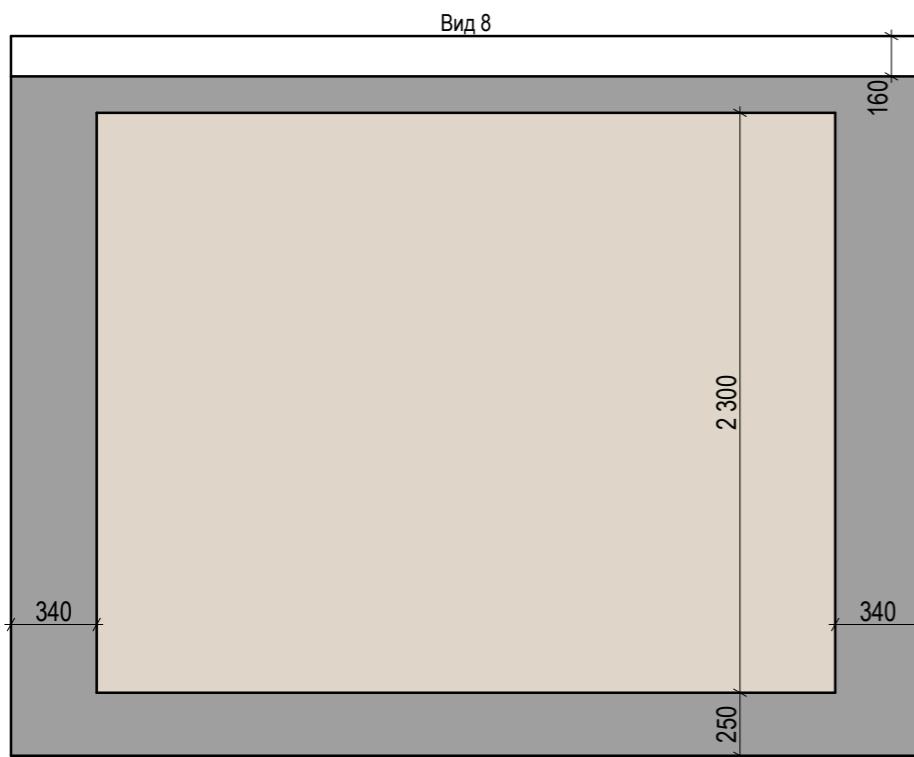

0 1000 2000 м

Условные обозначения:

	Декоративное покрытие 1	19,75 м ²
	Декоративное покрытие 2	9,93 м ²
	Декоративное покрытие 3	5,34 м ²
• Светодиодная лента		

Заказчик:

Изм.	Кол.уч	Лист	№ док	Подп.	Дата
Разработал					
ГАП					
ГИП					
Чертит					
Дата изменения					
Заказчик					

Адрес:

Стадия	Лист	Листов
P	9	34


Виды 8, 9, 10, 11

Согласовано			
Инв.№ подп.	Подп. и дата	Взам. инд.№	

План после перепланировки (только для смет)

Высота потолка - 2955 мм. Общая площадь - 141.24 кв.м.

Экспликация помещений

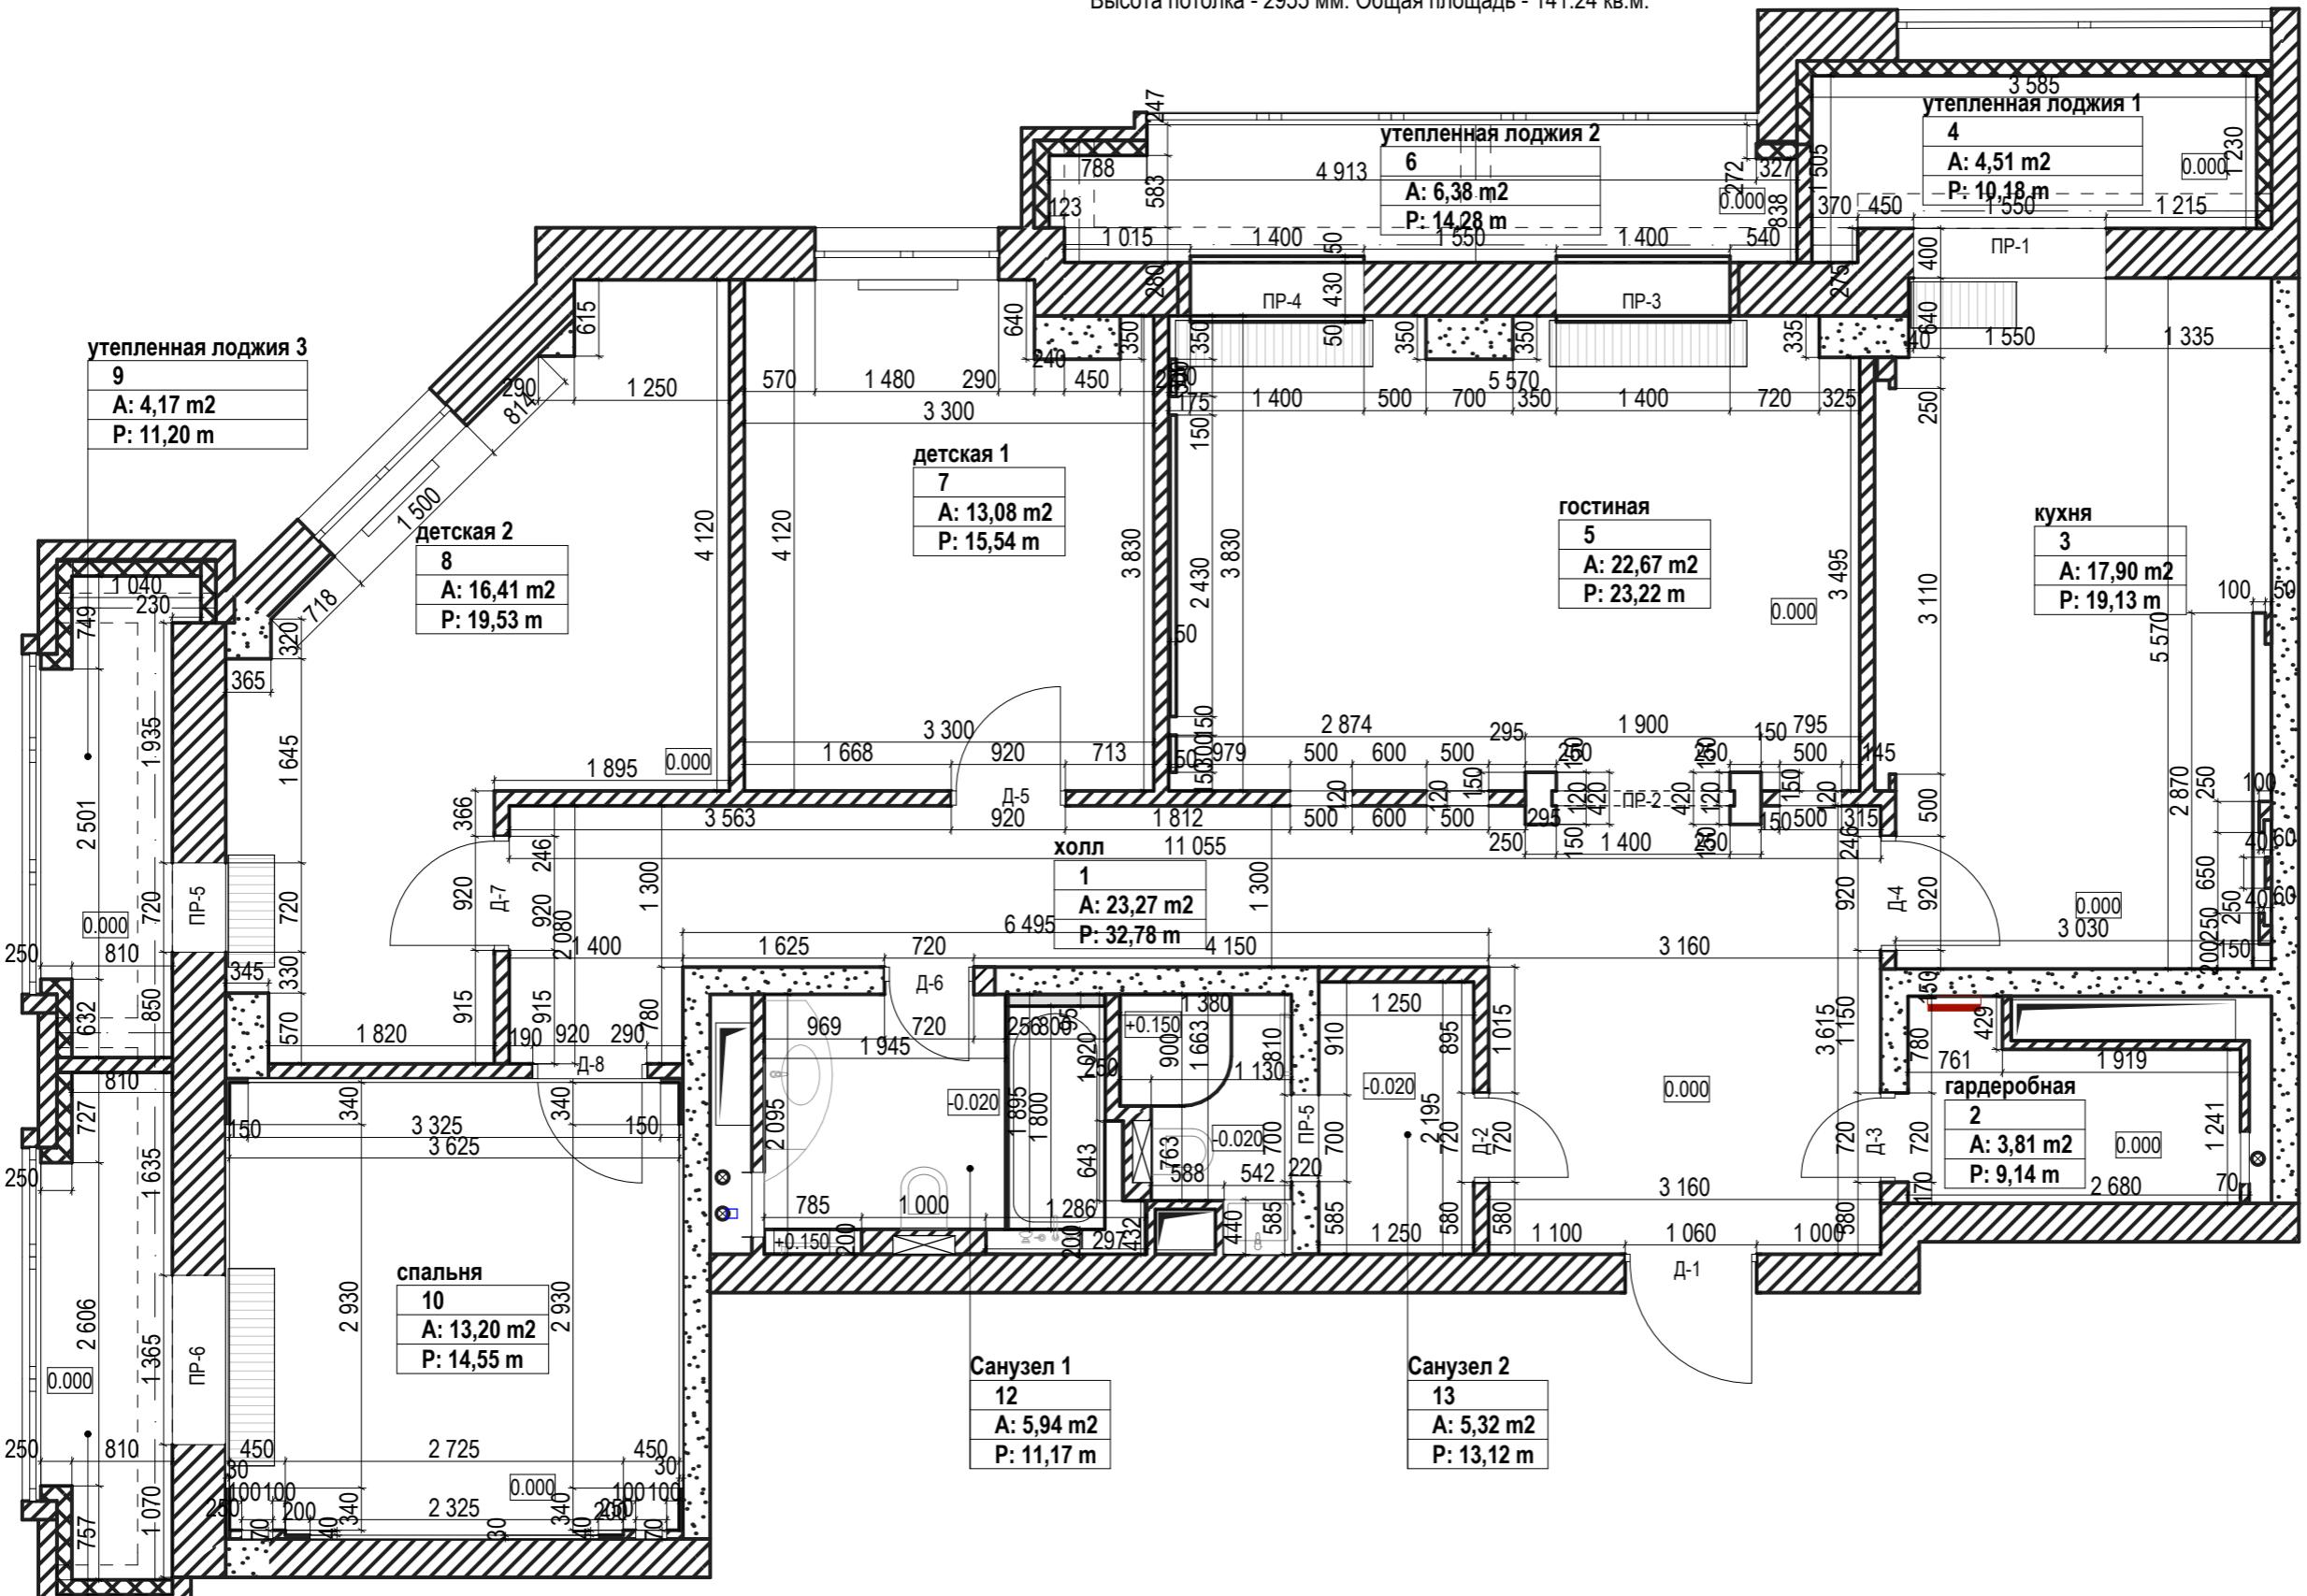

Спецификация дверных проёмов.

Марка	Обозначение	Наименование (размер)	Кол-во	Примечание
	ДВЕРИ			
Д-1	Входная дверь Excellence ICE RAL7036, цвет короба и кромки полотна RAL9006 цвет фурнитуры ручки и накладки в алюминии серебристом	Существующий проем	1шт	
Д-2	ICE RAL7036 ON "Барраус" Нахимовский пр-т, 24, павильон 3, стенд 528	720x2150	1шт	
Д-3	ICE RAL7036 ON "Барраус" Нахимовский пр-т, 24, павильон 3, стенд 528	720x2150	1шт	
Д-4	ICE RIVER RAL7036 "Барраус" Нахимовский пр-т, 24, павильон 3, стенд 528	920x2150	1шт	
Д-5	ICE RAL7036 ON "Барраус" Нахимовский пр-т, 24, павильон 3, стенд 528	920x2150	1шт	
Д-6	ICE RAL7036 ON "Барраус" Нахимовский пр-т, 24, павильон 3, стенд 528	720x2150	1шт	
Д-7	ICE RAL7036 ON "Барраус" Нахимовский пр-т, 24, павильон 3, стенд 528	920x2150	1шт	
Д-8	ICE RAL7036 ON "Барраус" Нахимовский пр-т, 24, павильон 3, стенд 528	920x2150	1шт	
ПР-1		1550x2400	1шт	
ПР-2		1400x2400	1шт	
ПР-3		1400x2400	1шт	
ПР-4		1400x2400	1шт	
ПР-5		720x2400	1шт	
ПР-6		1360x2400	1шт	

Примечание


1. Смотреть совместно с листом № 5.
 2. Магазин:

План пола

Высота потолка - 2955 мм. Общая площадь - 142.27 кв.м.

Экспликация помещений

N-N	Наименование	Площадь м ²
1	Холл	23,52
2	Гардеробная	3,81
3	Кухня	17,45
4	Утепленная лоджия 1	5,13
5	Гостиная	21,36
6	Утепленная лоджия 2	7,65
7	Детская 1	13,18
8	Детская 2	16,17
9	Утепленная лоджия 3	4,16
10	Спальня	13,20
11	Утепленная лоджия 4	4,56
12	сан.узел 1	5,73
13	сан.узел 2	5,35
	Всего	141,27

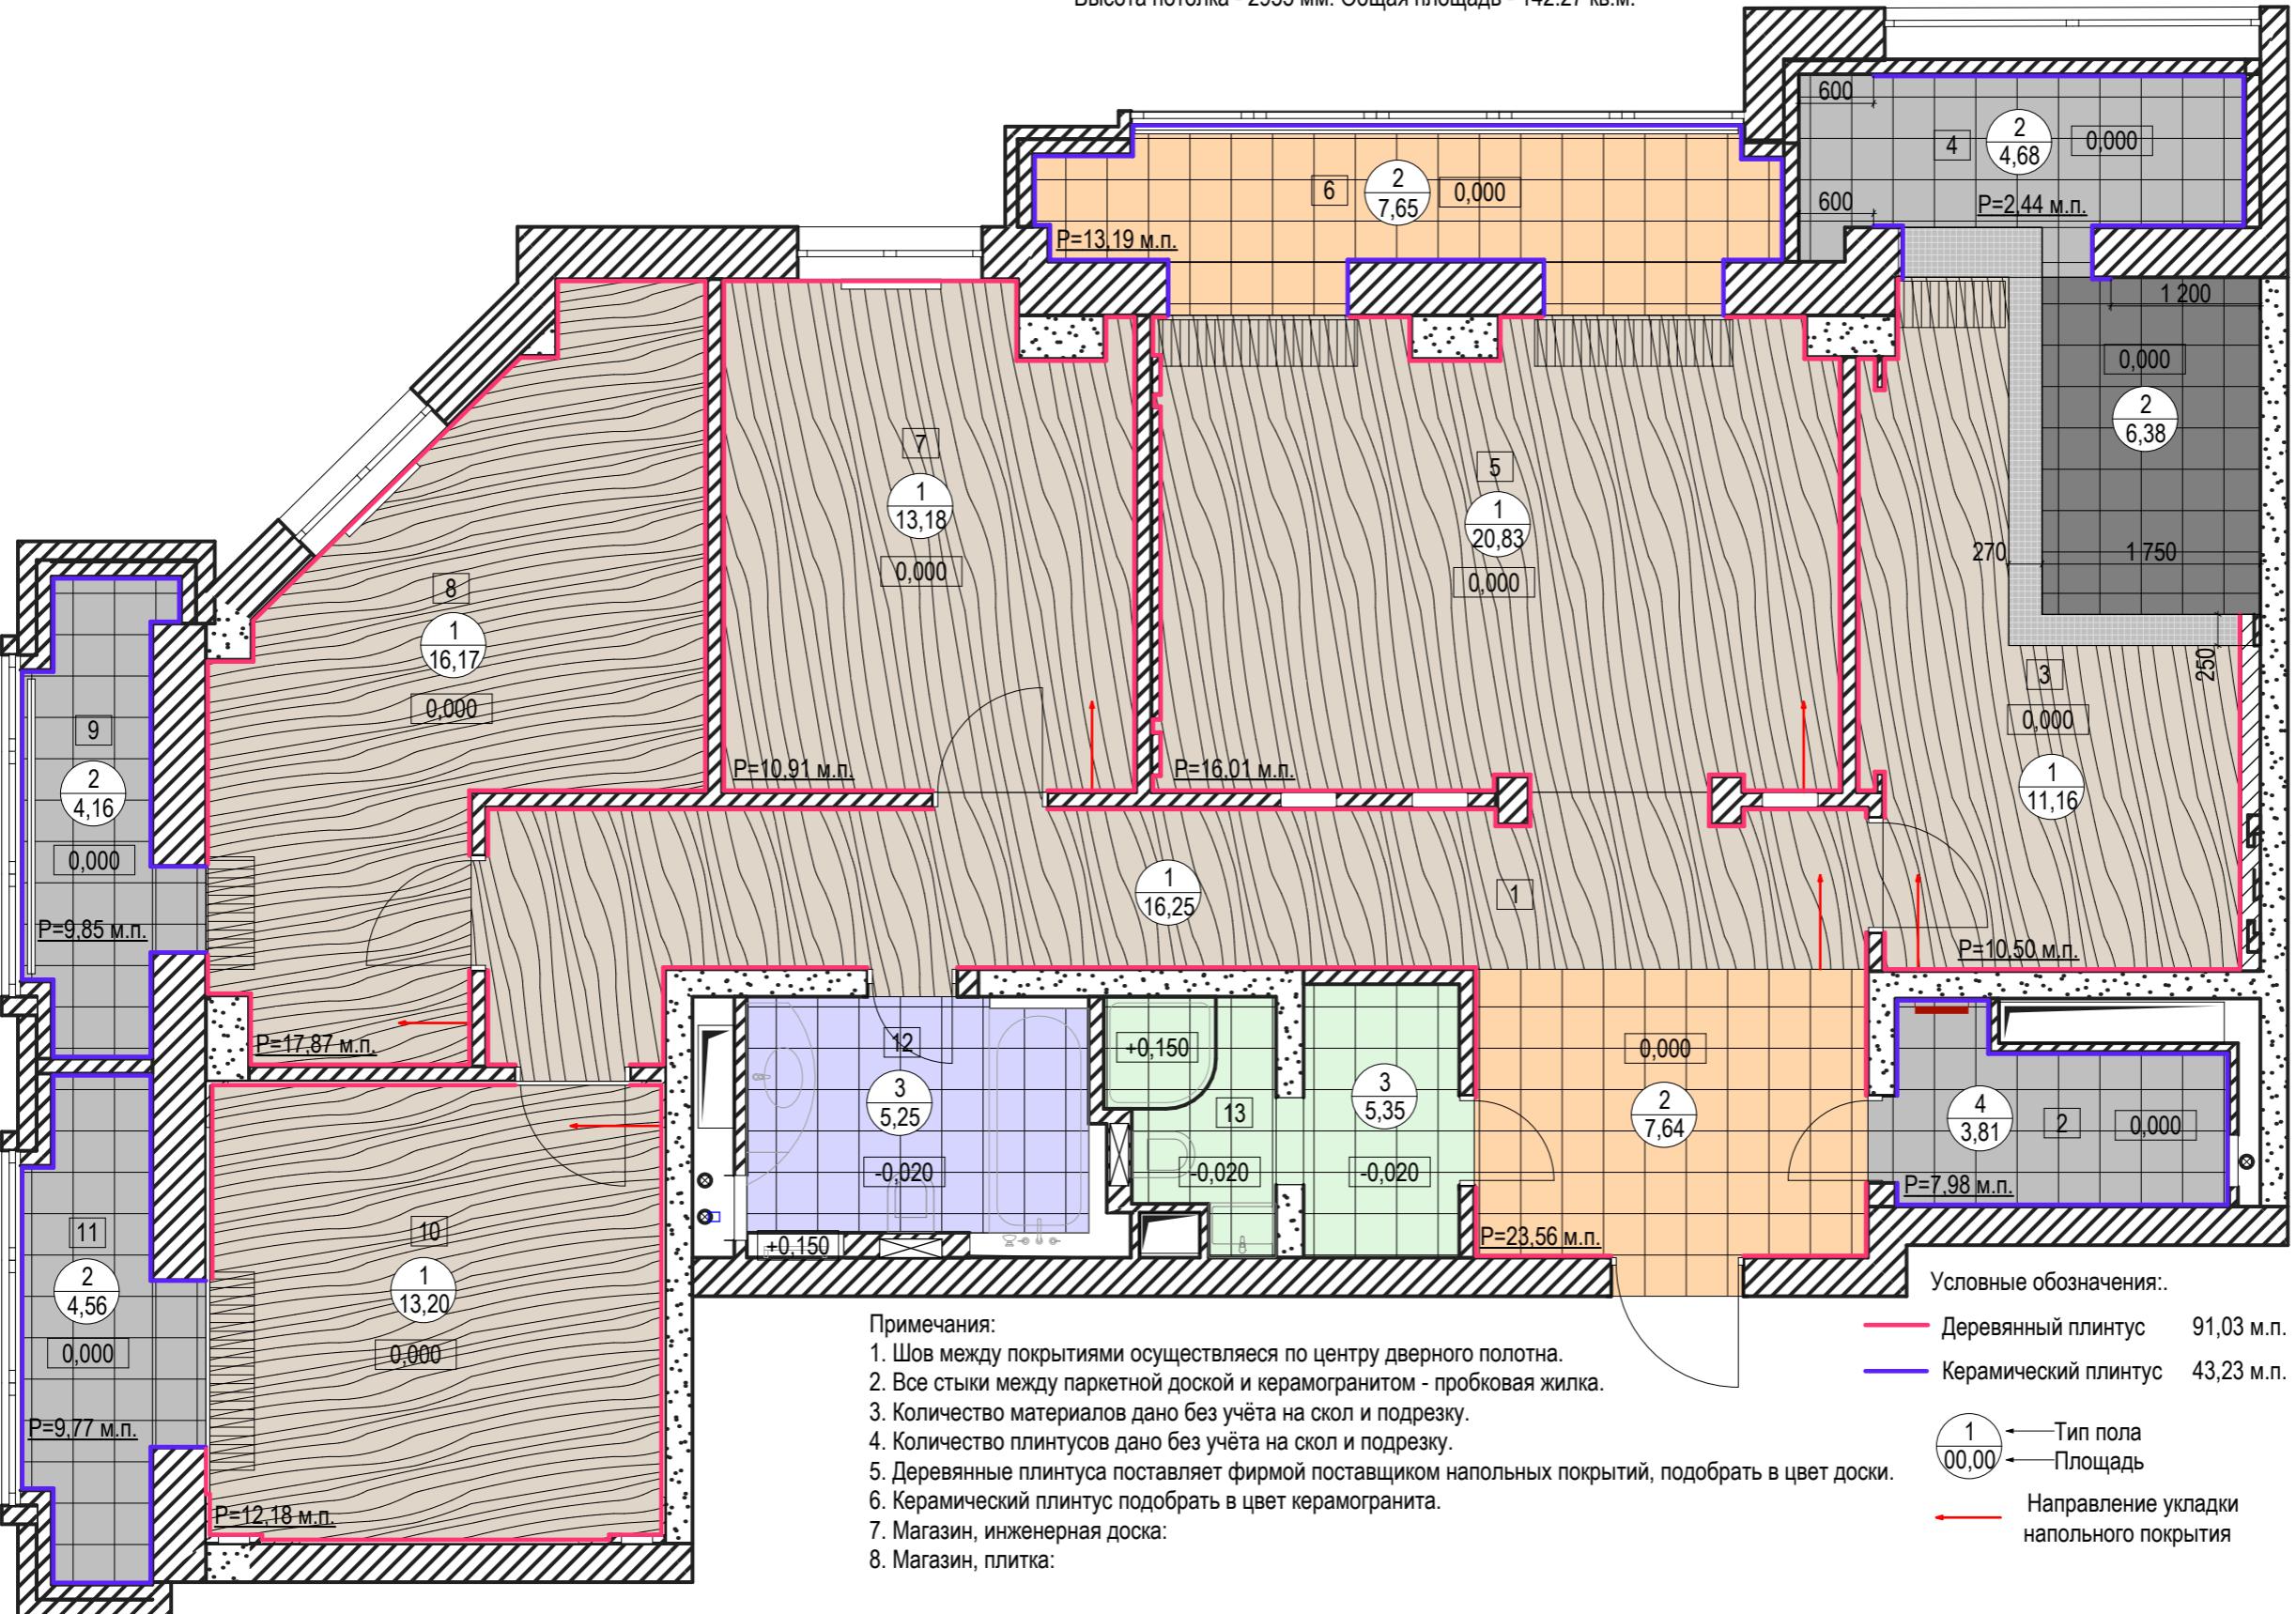

Инв. № подп. Подп. и дата Взам. инд. №

0 1000 2000 м

Изм.	Кол.уч	Лист	№ док	Подп.	Дата	Адрес:	Стадия	Лист	Листов
Разработал							P	12	34
ГАП						Заказчик:			
ГИП						План пола			
Чертит									
Дата изменения									
Заказчик									


Экспликация полов

Наименование помещения	Тип пола	Схема пола	Данные элементов пола (наименование, толщина, основание и др.)	Площадь пола, м ²
Холл Кухня Гостиная Детская 1 Детская 2 Спальня	1		1. Инженерная доска t=15 мм 2. Клей t=2-6 мм 3. Фанера t=15 мм 4. Наливной пол t=2-5 мм 5. Армированная стяжка t= 2мм 6. Существующее перекрытие	S=90,79м ²
Холл Кухня Лоджия 1 Лоджия 2 Лоджия 3 Лоджия 4	2		1. Керамогранит/керамическая плитка t=10 мм 2. Клей t=2-6 мм 3. Наливной пол t=2-5 мм 4. Теплый пол t= 2мм 5. Армированная стяжка t= 2мм 6. Существующее перекрытие	S=35,07м ²
C/y1 C/y2	3		1. Керамогранит/керамическая плитка t=10 мм 2. Клей t=2-6 мм 3. Наливной пол t=2-5 мм 4. Теплый пол t= 2мм 5. Армированная стяжка t= 2мм 6. Обмазочная гидроизоляция t=5 мм 7. Существующее перекрытие	S=11,60м ²
Гардеробная	4		1. Керамогранит/керамическая плитка t=10 мм 2. Клей t=2-6 мм 3. Наливной пол t=2-5 мм 4. Армированная стяжка t= 2мм 5. Существующее перекрытие	S=3,81м ²

Заказчик:

План теплого пола

Высота потолка - 2955 мм. Общая площадь - 142.27 кв.м.

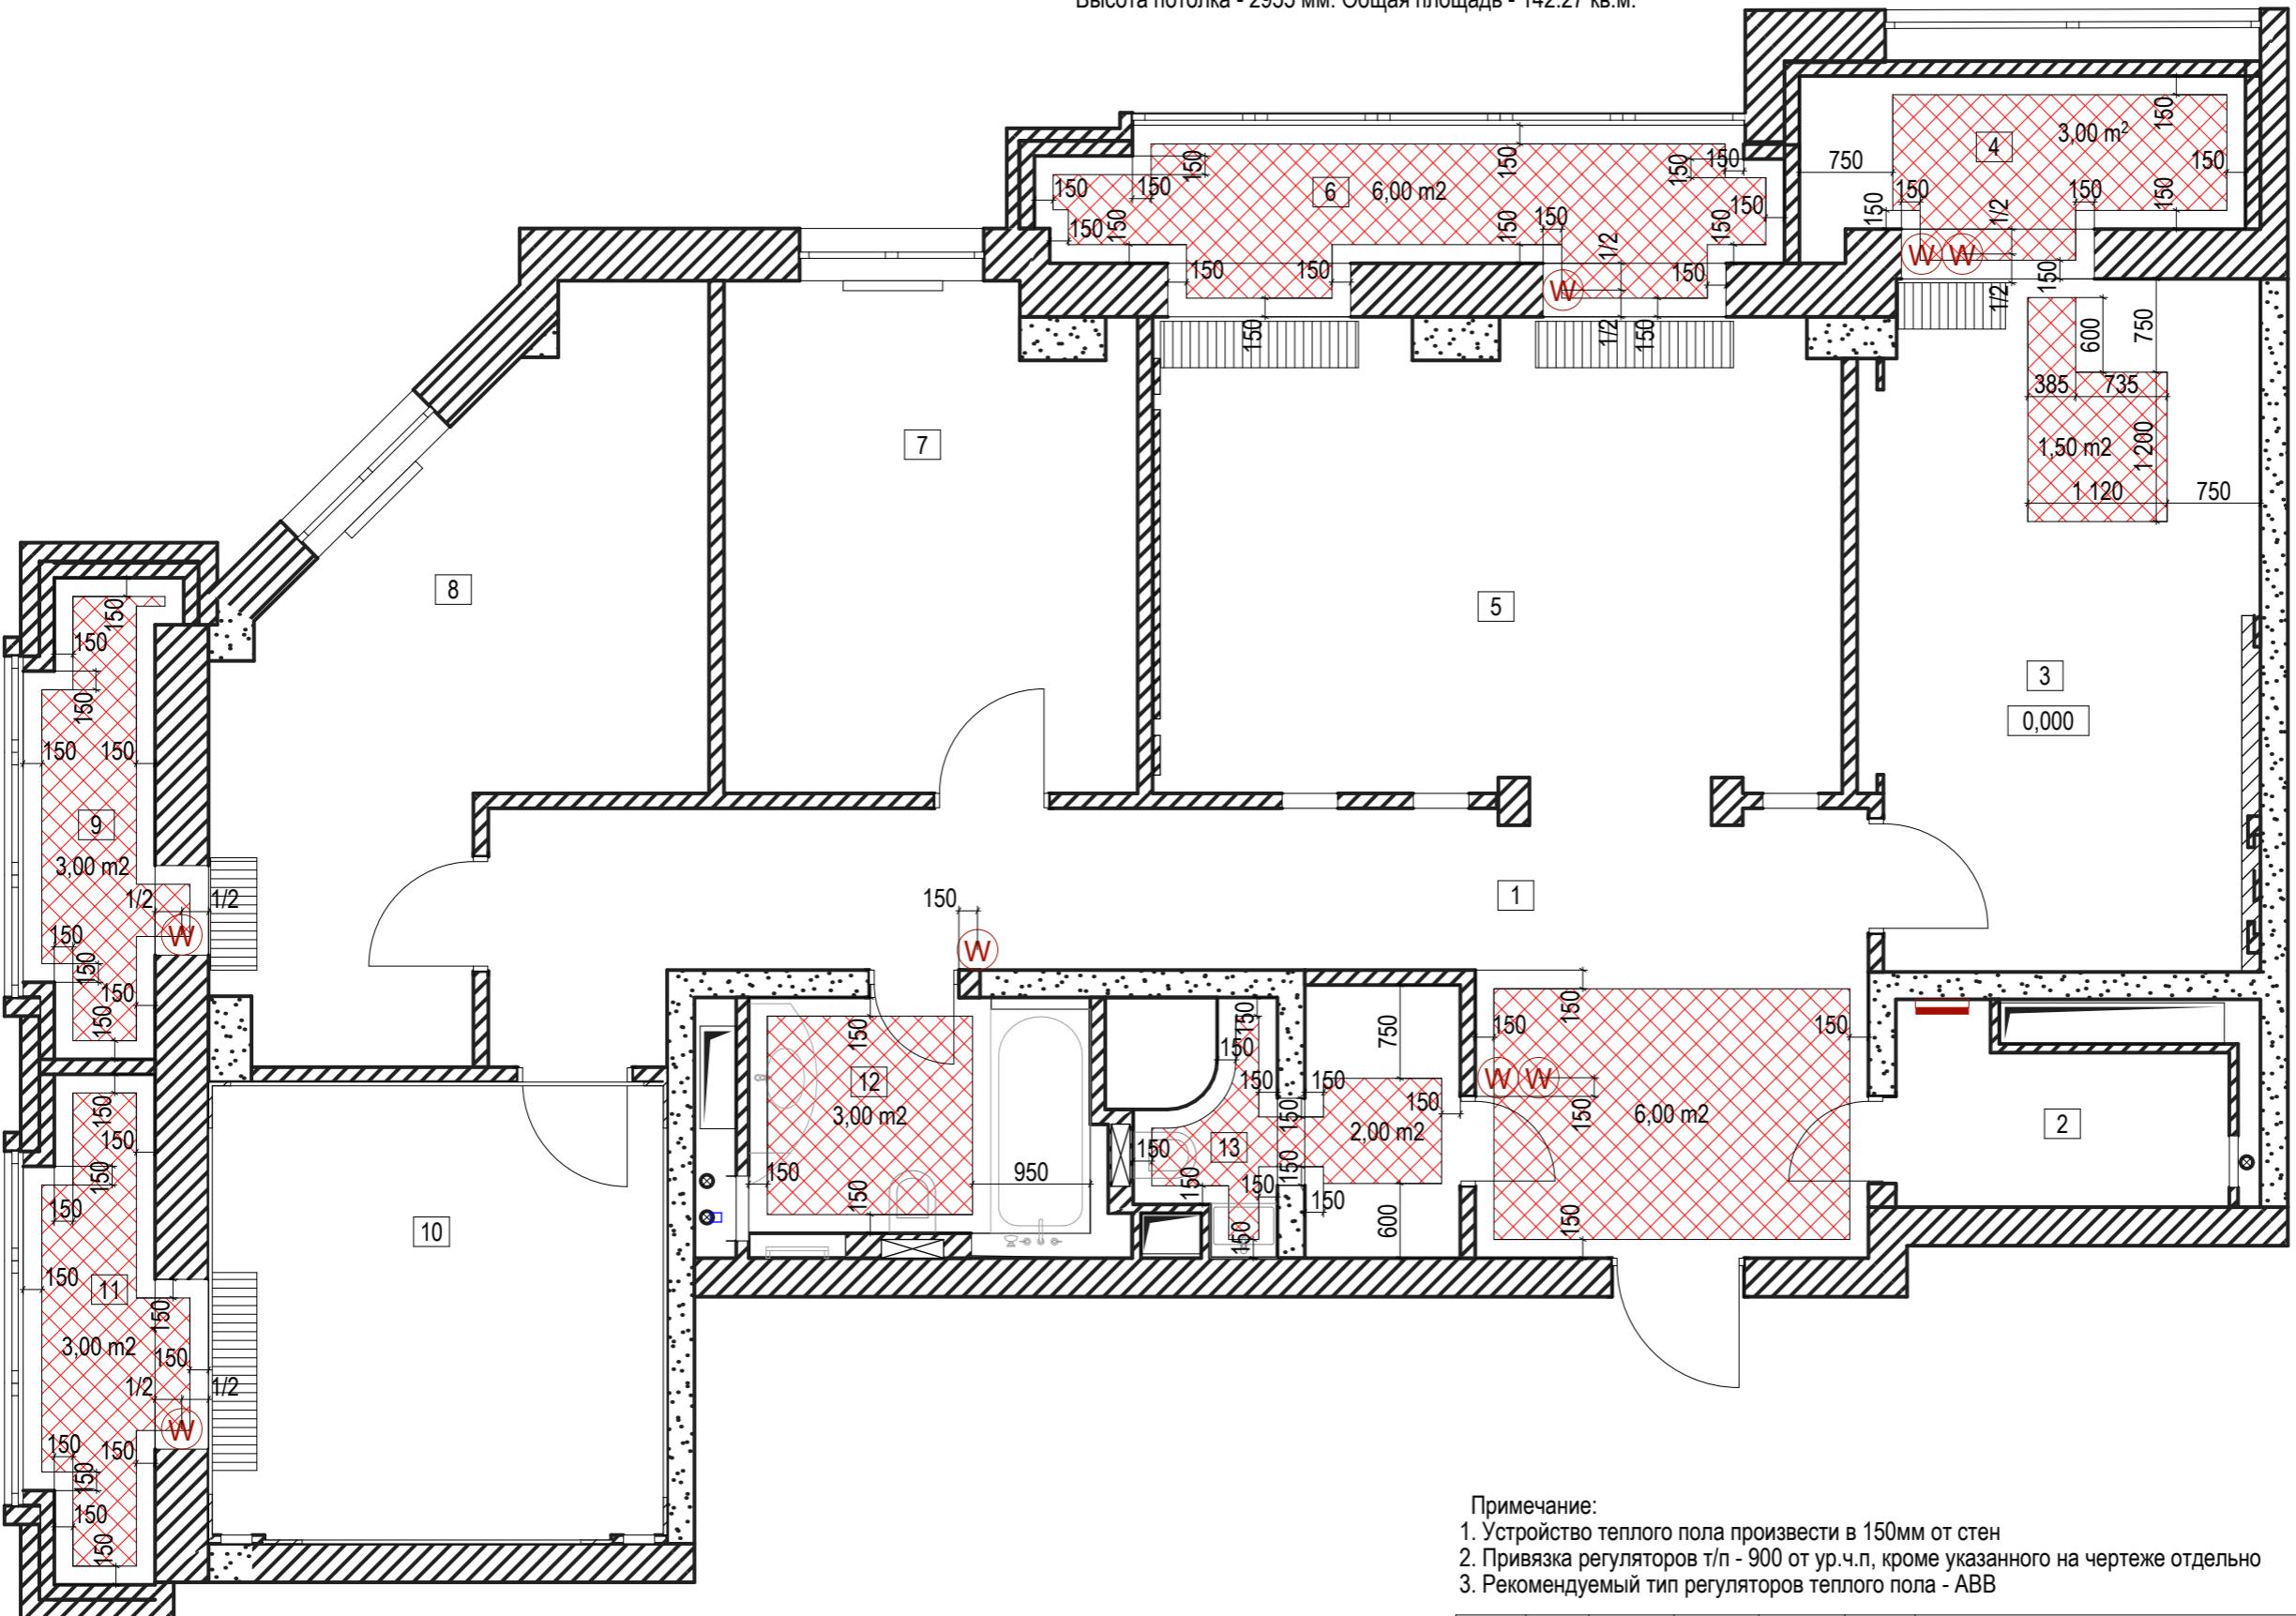

Экспликация помещений

N-N	Наименование	Площадь м ²
1	Холл	23,52
2	Гардеробная	3,81
3	Кухня	17,45
4	Утепленная лоджия 1	5,13
5	Гостиная	21,36
6	Утепленная лоджия 2	7,65
7	Детская 1	13,18
8	Детская 2	16,17
9	Утепленная лоджия 3	4,16
10	Спальня	13,20
11	Утепленная лоджия 4	4,56
12	сан.узел 1	5,73
13	сан.узел 2	5,35
	Всего	141,27

Условные обозначения:

0,00 m ²	Тёплый пол Собщ=27,50m ²
W	Регулятор теплого пола
—	Электрощиток

Примечание:

- Устройство теплого пола произвести в 150мм от стен
- Привязка регуляторов т/п - 900 от ур.ч.п, кроме указанного на чертеже отдельно
- Рекомендуемый тип регуляторов теплого пола - ABB

Изм.	Кол.уч	Лист	№ док	Подп.	Дата	Заказчик: Адрес: План теплого пола	Стадия	Лист	Листов
Разработал							P	14	34
ГАП									
ГИП									
Чертит									
Дата изменения									
Заказчик									

План расстановки сантехники


Высота потолка - 2955 мм. Общая площадь - 141.24 кв.м.

Экспликация помещений

N-N	Наименование	Площадь м ²
1	Холл	23,27
2	Гардеробная	3,81
3	Кухня	17,90
4	Утепленная лоджия 1	4,51
5	Гостиная	22,67
6	Утепленная лоджия 2	6,38
7	Детская 1	13,08
8	Детская 2	16,41
9	Утепленная лоджия 3	4,17
10	Спальня	13,20
11	Утепленная лоджия 4	4,58
12	Сан.узел 1	5,94
13		5,32
	Всего	141,24

Спецификация оборудования:

№	Наименование
1	Ванна 1800x800
2	Унитаз подвесной 370x560
3	Полотенцесушитель электрический
4	Раковина подвесная 1200x600
5	Душевое ограждение 1200x1500
6	Душевое ограждение 900x900x1900
7	Полотенцесушитель электрический
8	Стиральная машина 600x600
9	Сушильная машина 600x600
10	Раковина подвесная 451x450
11	Унитаз подвесной 360x490
12	Мойка 1200x600
13	Посудомоечная машина 600x600

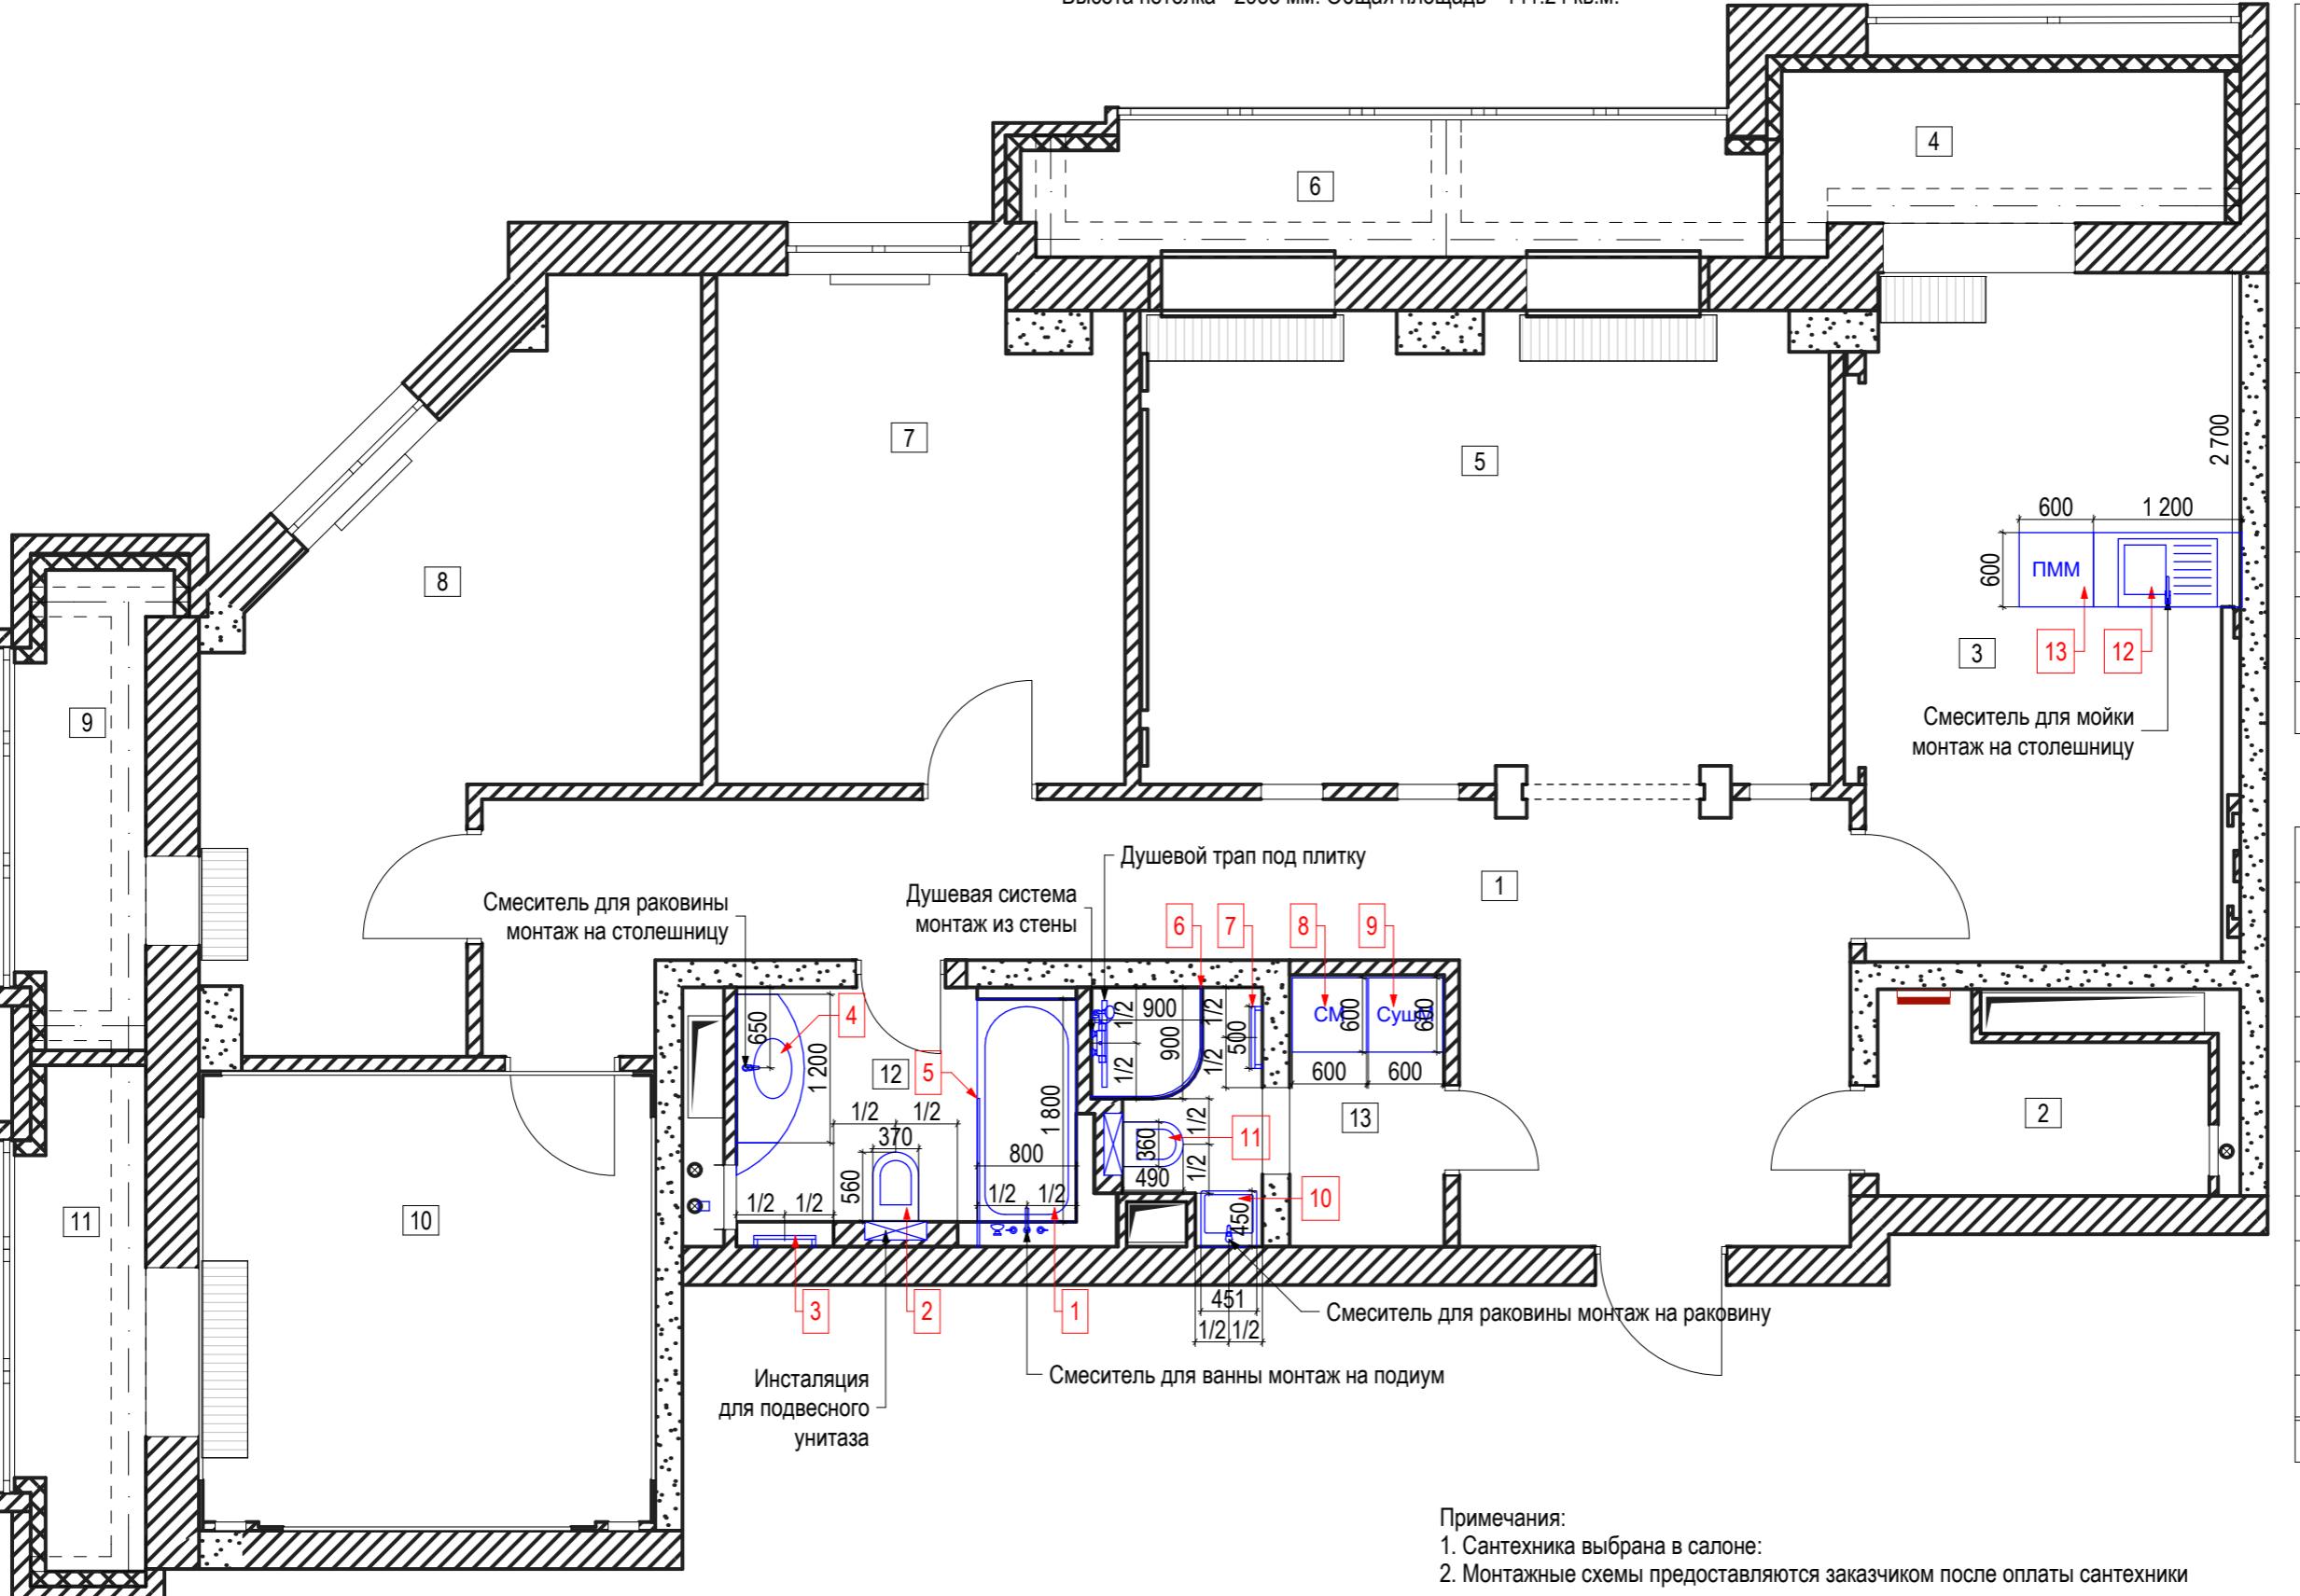

Примечания:

1. Сантехника выбрана в салоне:
2. Монтажные схемы предоставляются заказчиком после оплаты сантехники

Изм.	Кол.уч	Лист	№ док	Подп.	Дата	Адрес:	Стадия	Лист	Листов
Разработал							P	15	34
ГАП									
ГИП									
Чертил									
Дата изменения									
Заказчик									



План расстановки сантехники

Ракладка плитки по полу


Высота потолка - 2955 мм. Общая площадь - 142.27 кв.м.

Экспликация помещений

N-N	Наименование	Площадь м ²
1	Холл	23,52
2	Гардеробная	3,81
3	Кухня	17,45
4	Утепленная лоджия 1	5,13
5	Гостиная	21,36
6	Утепленная лоджия 2	7,65
7	Детская 1	13,18
8	Детская 2	16,17
9	Утепленная лоджия 3	4,16
10	Спальня	13,20
11	Утепленная лоджия 4	4,56
12	сан.узел 1	5,73
13	сан.узел 2	5,35
	Всего	141,27

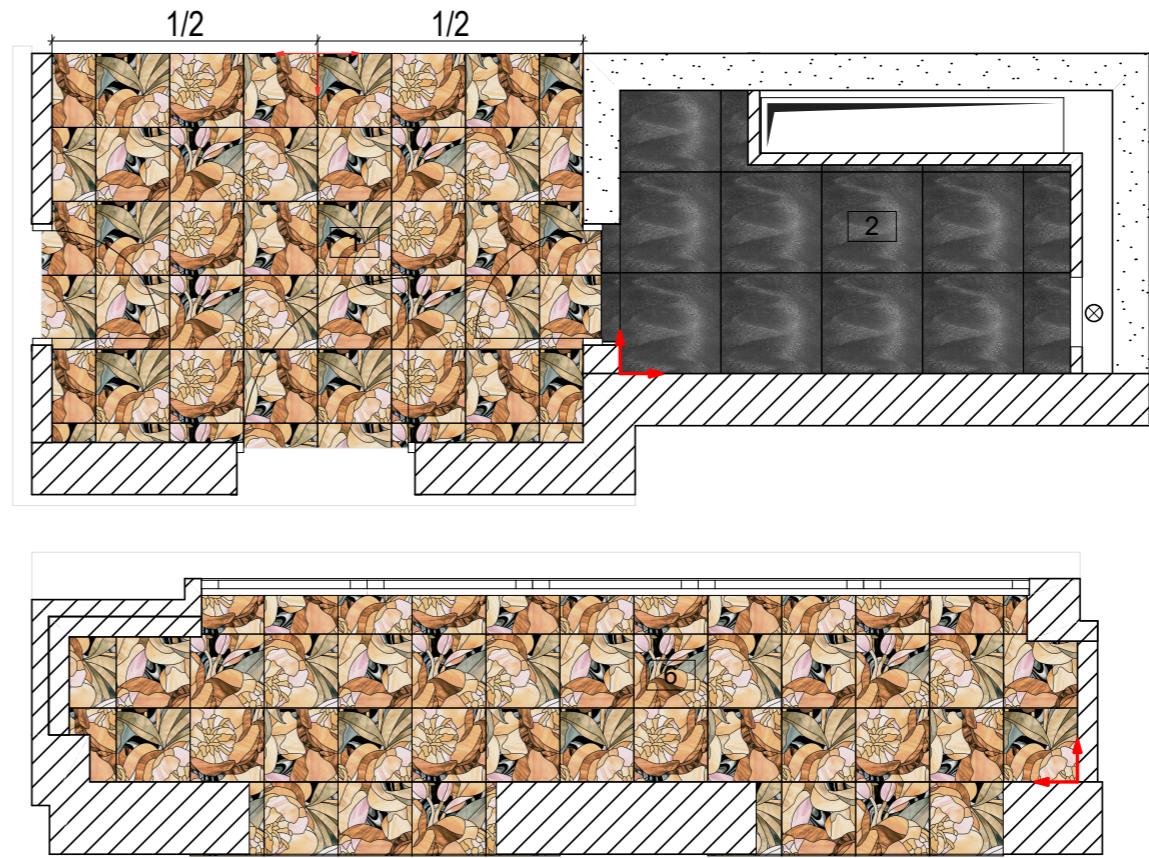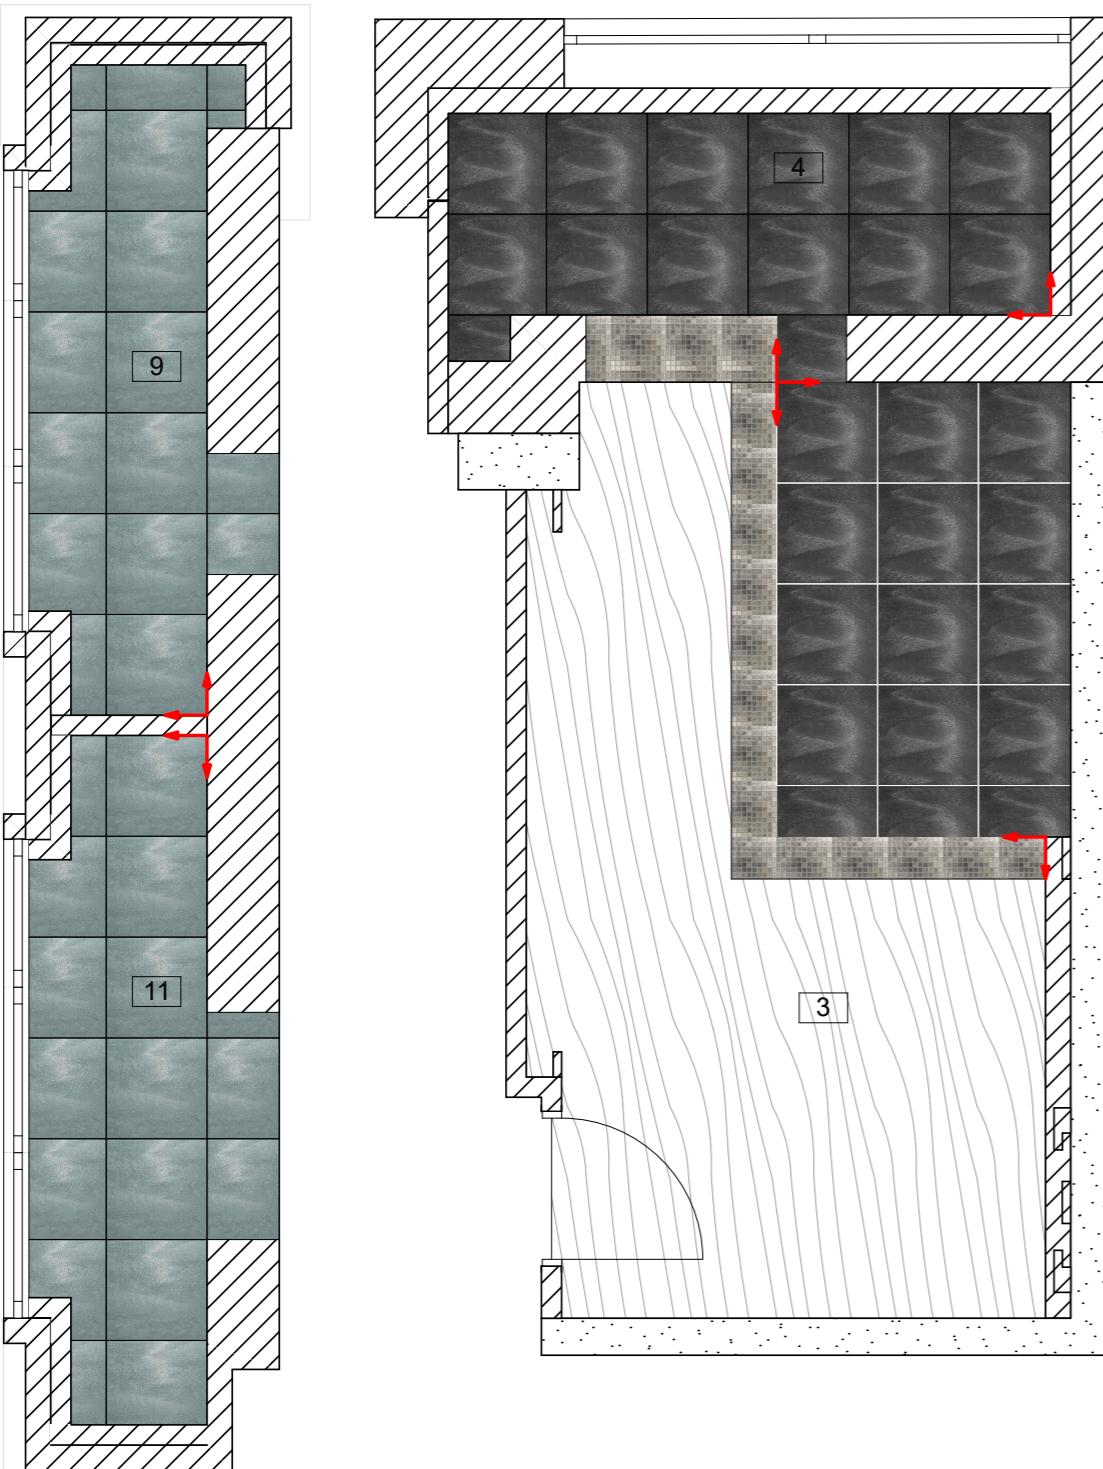


Условные обозначения:

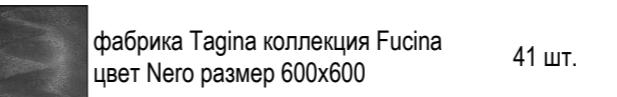


фабрика Tagina коллекция Fucina
цвет Nero размер 600x600

41 шт.

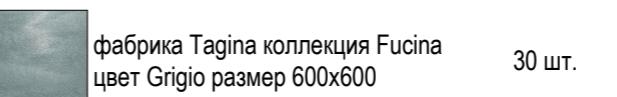

фабрика Tagina коллекция Fucina
цвет Grigio размер 600x600

30 шт.

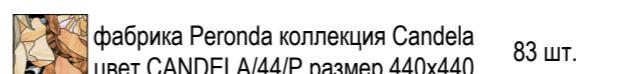

фабрика Peronda коллекция Candela
цвет CANDELA/44/P размер 440x440

83 шт.



Фабрика Dune 184330 2.5X2.5
VITRA MOSAICO PLATINO BRILL D910 290x290

← Направление раскладки

Примечания:

1. Количество плитки дано без учёта на скол и подрезку.
2. Плитка и керамогранит, шов минимальный.
3. Затирку шва подобрать в цвет плитки.
4. Магазин, плитка:

Изм.	Кол.уч	Лист	№ док	Подп.	Дата
Разработал					
ГАП					
ГИП					
Чертил					
Дата изменения					
Заказчик					

Заказчик:

Адрес:

Стадия	Лист	Листов
P	16	34


Раскладка плитки по полу

Инв. № подп.	Подп. и дата	Взам. инд. №
0	1000	2000

0 1000 2000 м

Раскладка плитки санузел 1

Высота потолка - 2955 мм. Общая площадь - 142.27 кв.м.

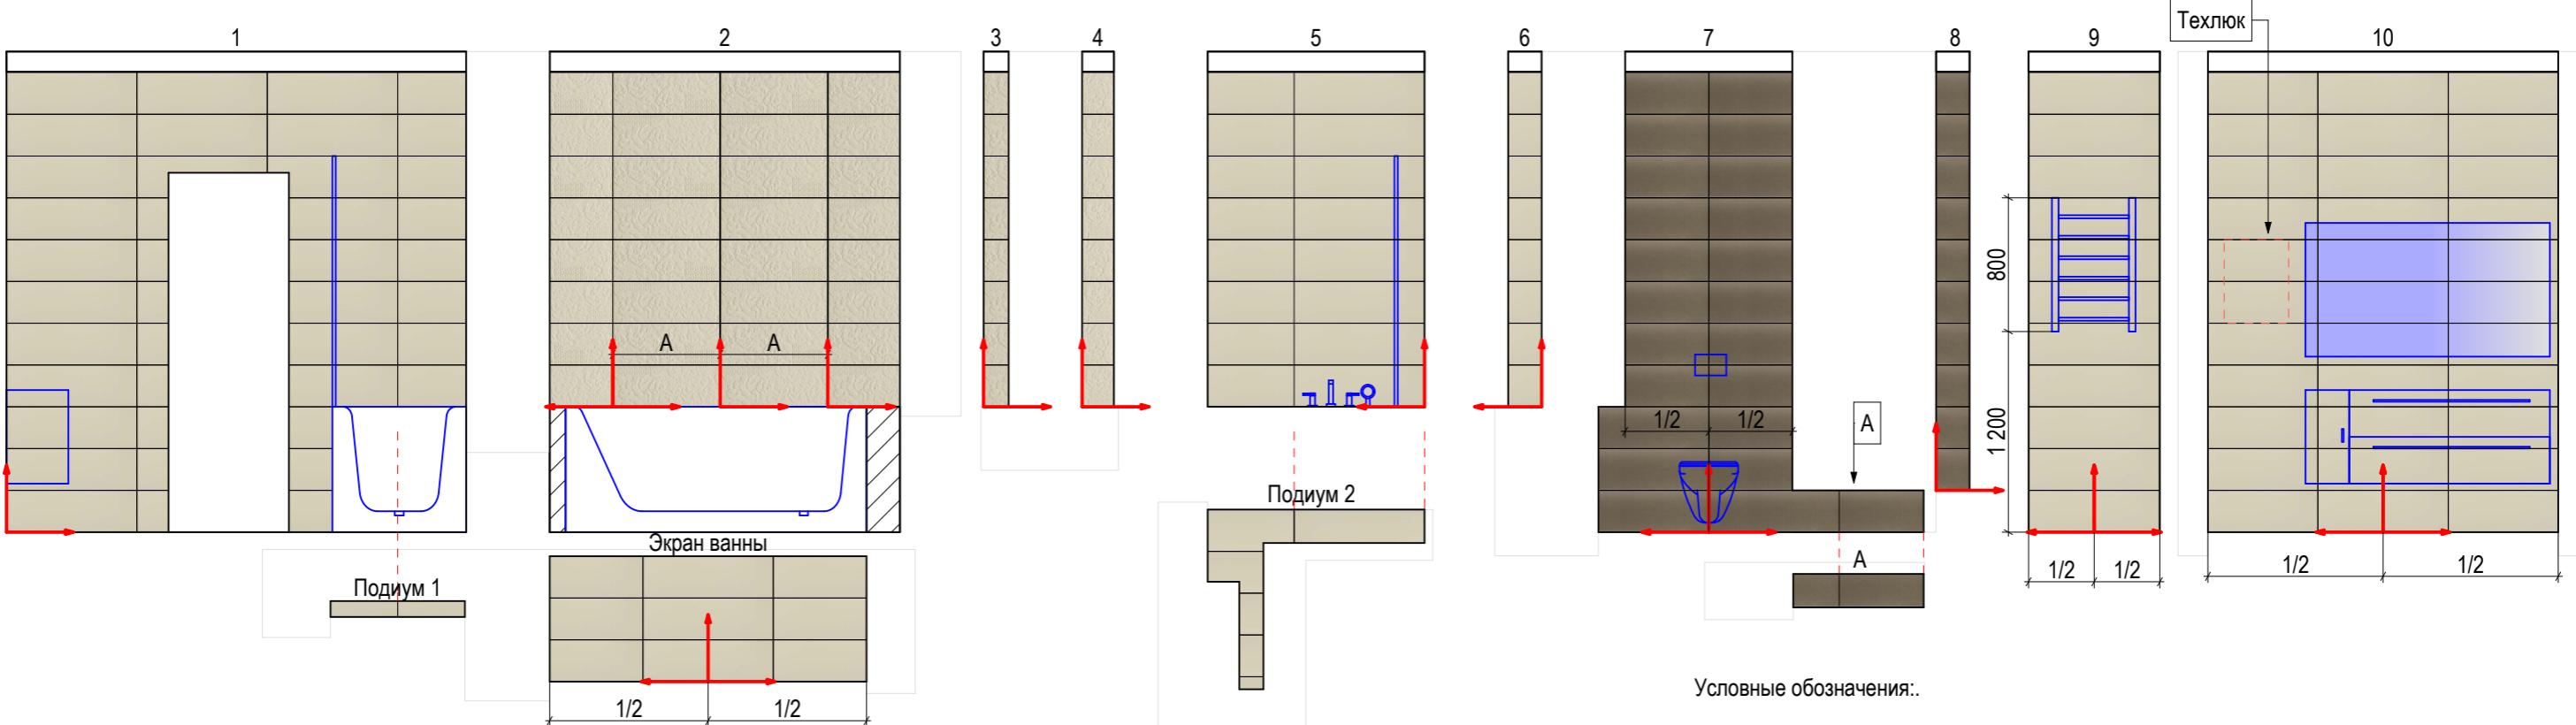

Условные обозначения:

Фабрика Versace коллекция Gold



Rivestimenti Crema 250x750 108 шт.

Rivestimenti Patchwork Crema 250x750 (mix 2 soggetti) 30 шт. (15 комплектов)

Rivestimenti Riga Marrone 250x750 24 шт.

Pavimenti Coordinati Marrone 600x600 14 шт.

→ Направление раскладки

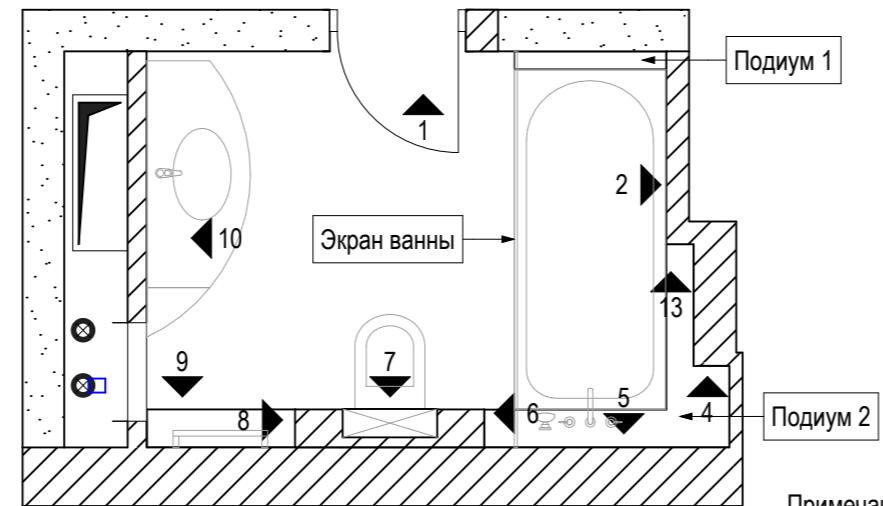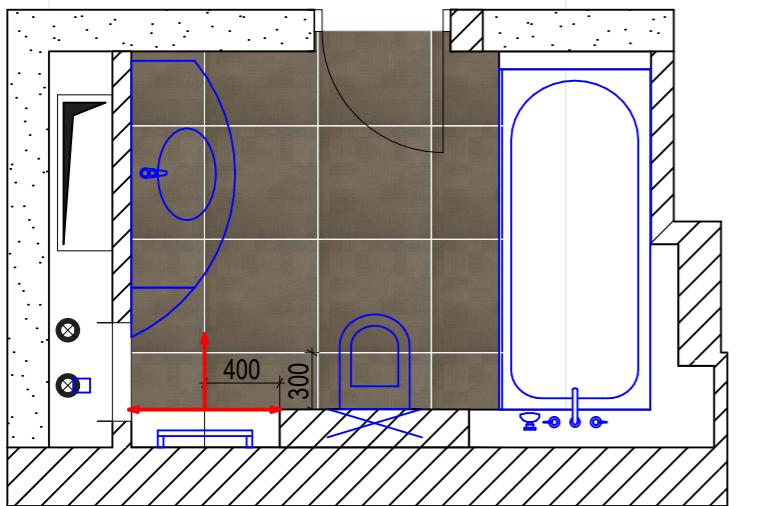

Примечания:

- Количество плитки дано без учета на скол и подрезку.
- Плитка и керамогранит, шов минимальный.
- Затирку шва подобрать в цвет плитки.
- Магазин, плитка:

Изм.	Кол.уч	Лист	№ док	Подп.	Дата
Разработал					
ГАП					
ГИП					
Чертил					
Дата изменения					
Заказчик					

Заказчик:

Адрес:	Стадия	Лист	Листов
	P	17	34

Раскладка плитки санузел 1


Согласовано

Инв. № подп.	Подп. и дата	Взам. инд. №
--------------	--------------	--------------

0 1000 2000 м

Раскладка плитки санузел 2

Высота потолка - 2955 мм. Общая площадь - 142.27 кв.м.

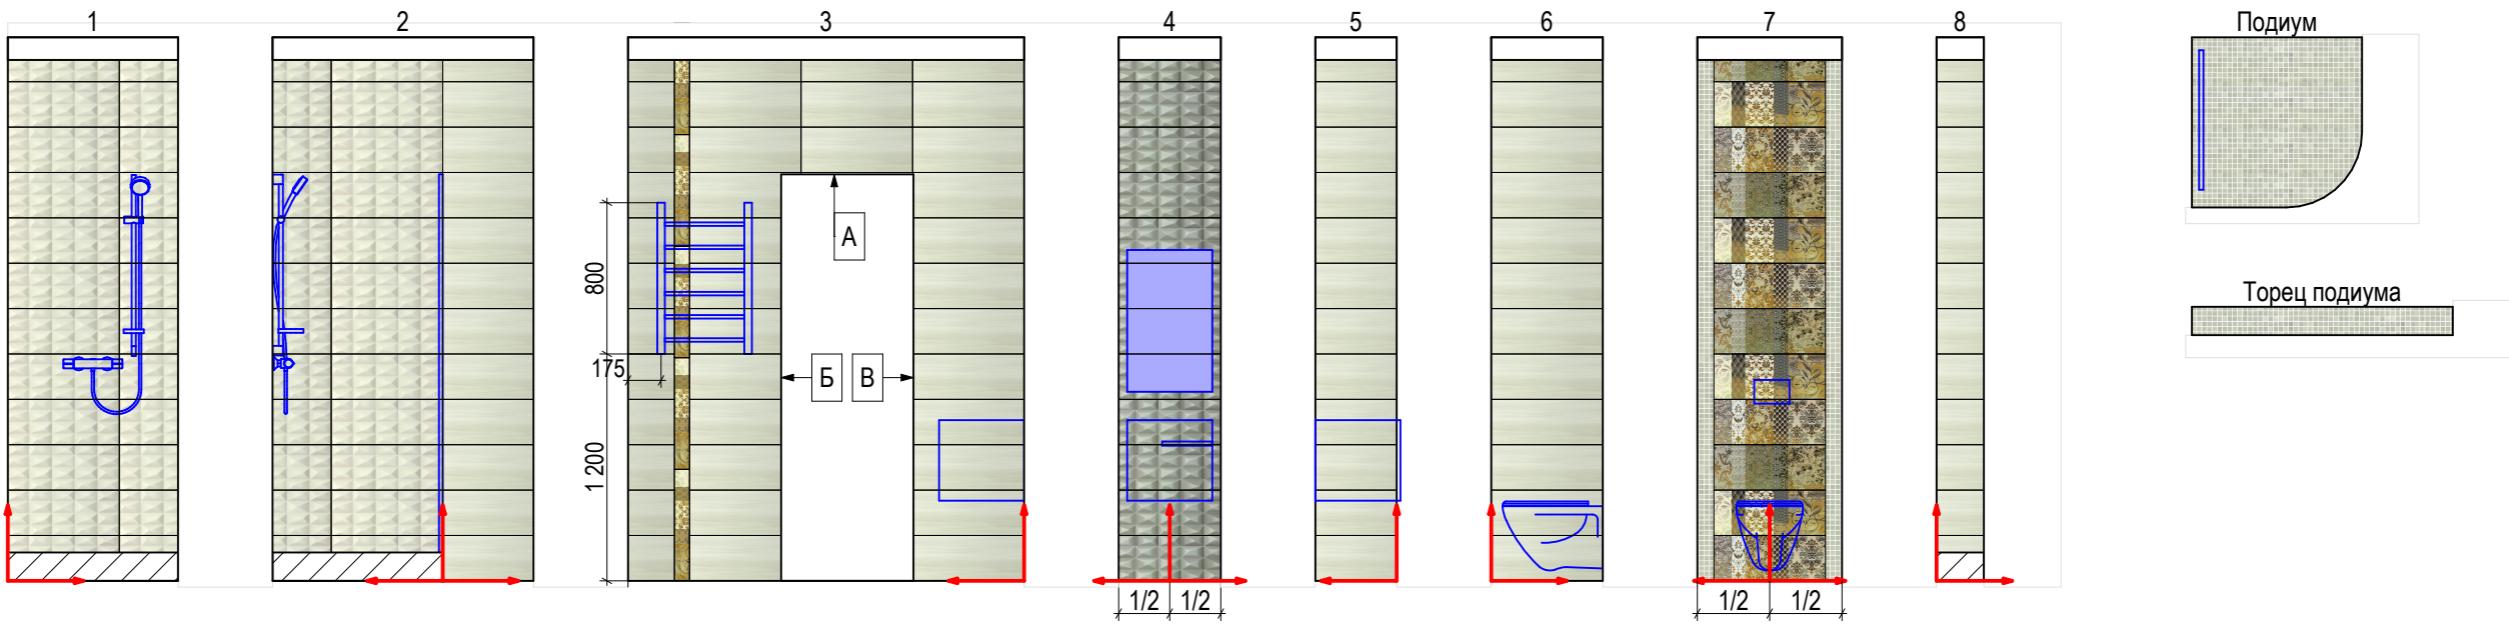

Условные обозначения:

Фабрика Importa Ceramiche коллекция Shine

	SH0229 SHINE OPALE 240x590	226 шт.
	SH0229M SHINE OPALE DIAMANTE MOSAICO 240x590	36 шт.
	SH02MA SHINE OPALE MOSAICO 240x590	1,47 м ²
	SH00DA SHINE BATIK ORO DECORO A 240x590	4 шт.
	SH00DB SHINE BATIK ORO DECORO B 240x590	4 шт.
	SH00DC SHINE BATIK ORO DECORO C 240x590	4 шт.
	SH0329M SHINE TORMALINA DIAMANTE MOSAICO 240x590	12 шт.
	SH00LA SHINE BATIK ORO LISTELLO A 80x590	5 шт.
	SQ0568 SQUARE DISTRICT 600x600	16 шт.

Направление раскладки

Примечания:

- Количество плитки дано без учета на скол и подрезку.
- Плитка и керамогранит, шов минимальный.
- Затирку шва подобрать в цвет плитки.
- Магазин, плитка:

Изв.	Кол.уч	Лист	№ док	Подп.	Дата	Адрес:	Стадия	Лист	Листов
Разработал							P	18	34
ГАП									
ГИП									
Чертил									
Дата изменения									
Заказчик									

Раскладка плитки санузел 2


Изв. № подп.	Подп. и дата	Взам. инд. №	Согласовано
0	1000	2000	M

План потолка

Высота потолка - 2955 мм. Общая площадь - 142.27 кв.м.

Экспликация помещений

Углубление на 8мм для крепления
туда перфорированного МДФ
Усилить потолок металлическим каркасом


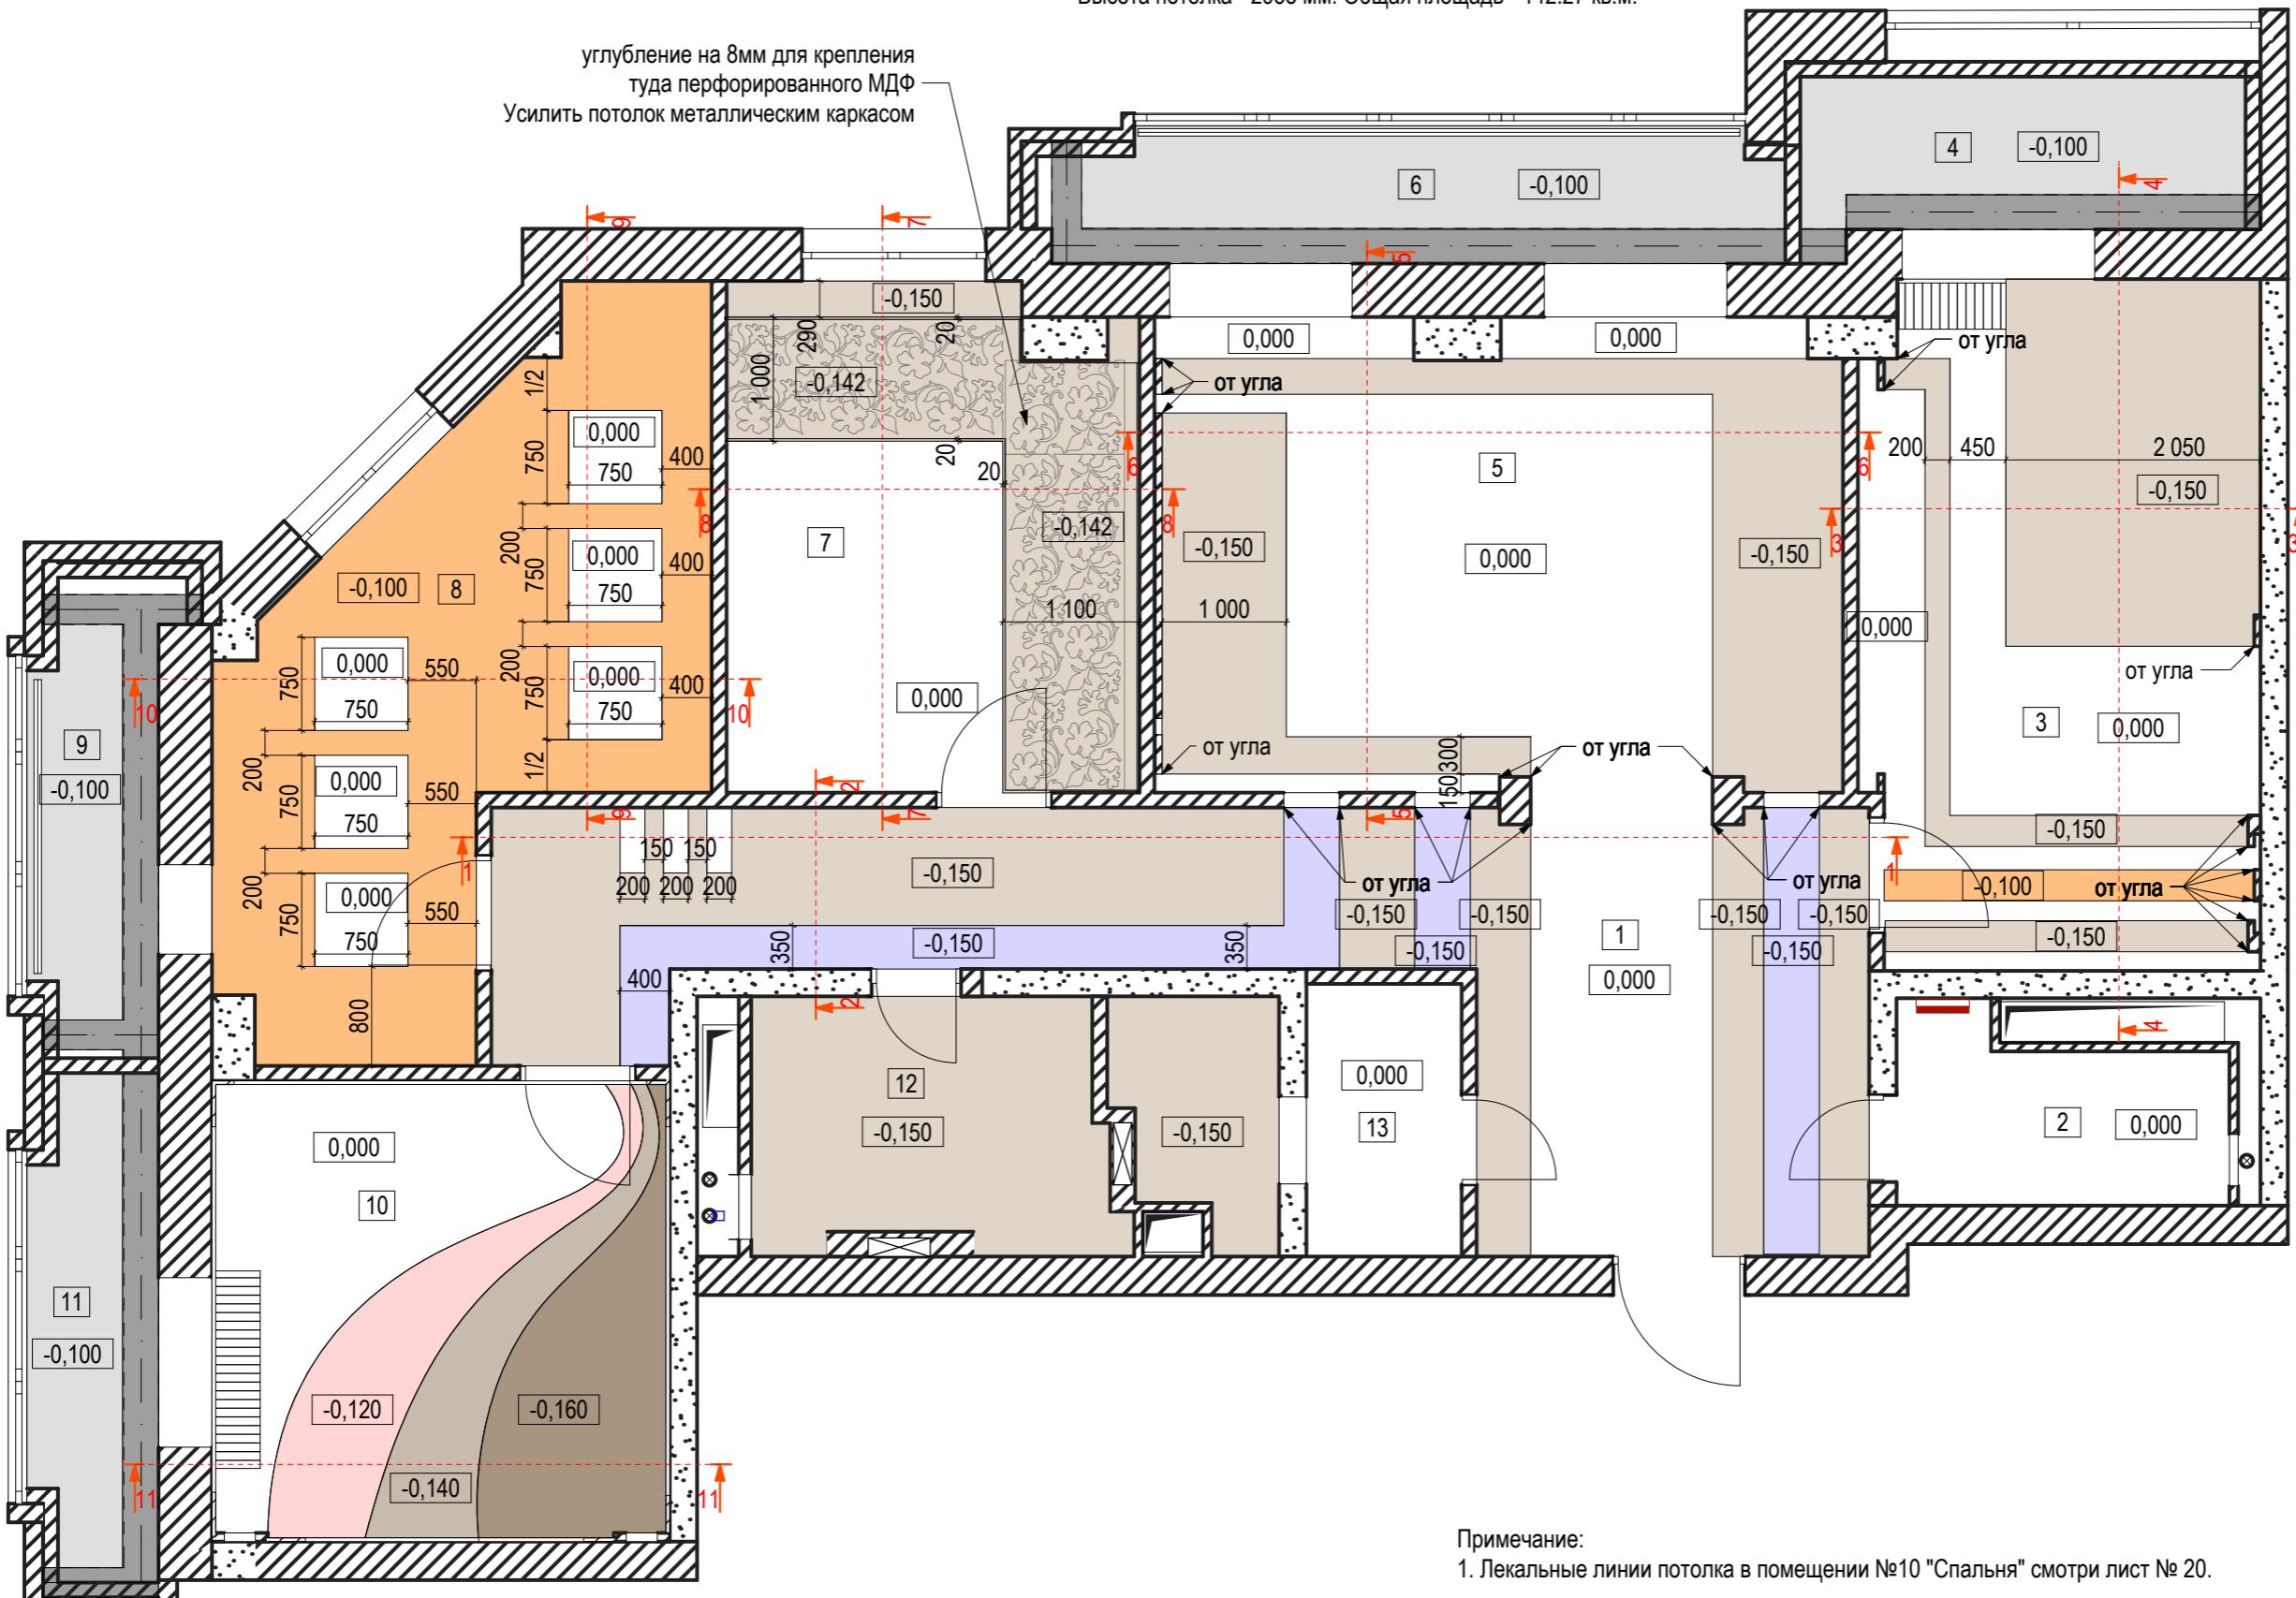


Примечание:

1. Лекальные линии потолка в помещении №10 "Спальня" смотри лист № 20.

Лекальные линии потолка

Высота потолка - 2955 мм. Общая площадь - 142.27 кв.м.

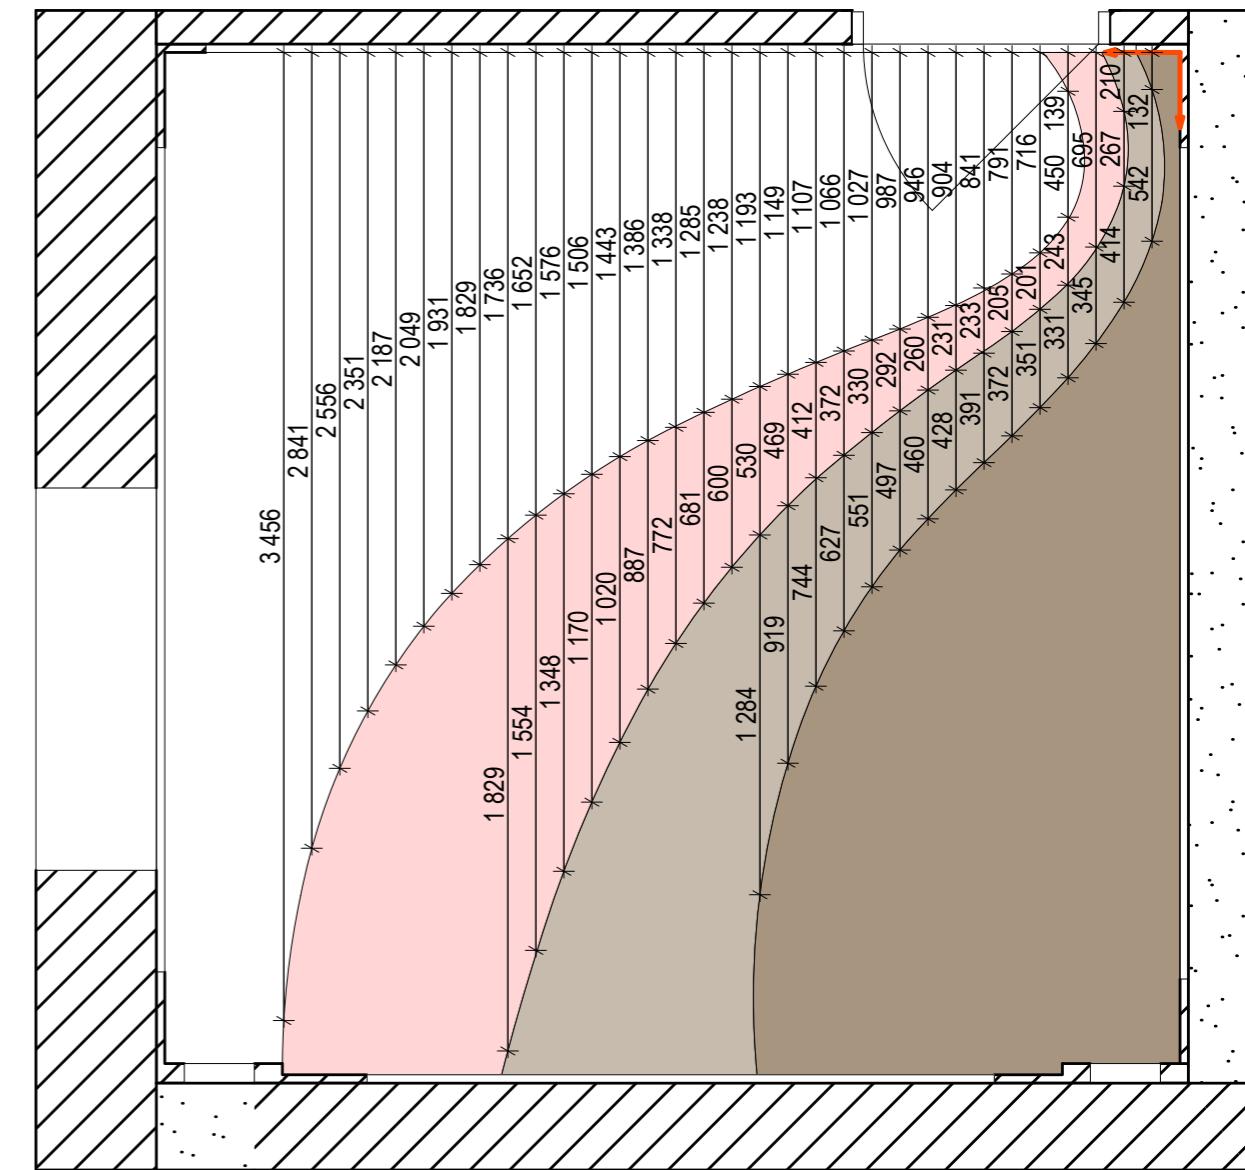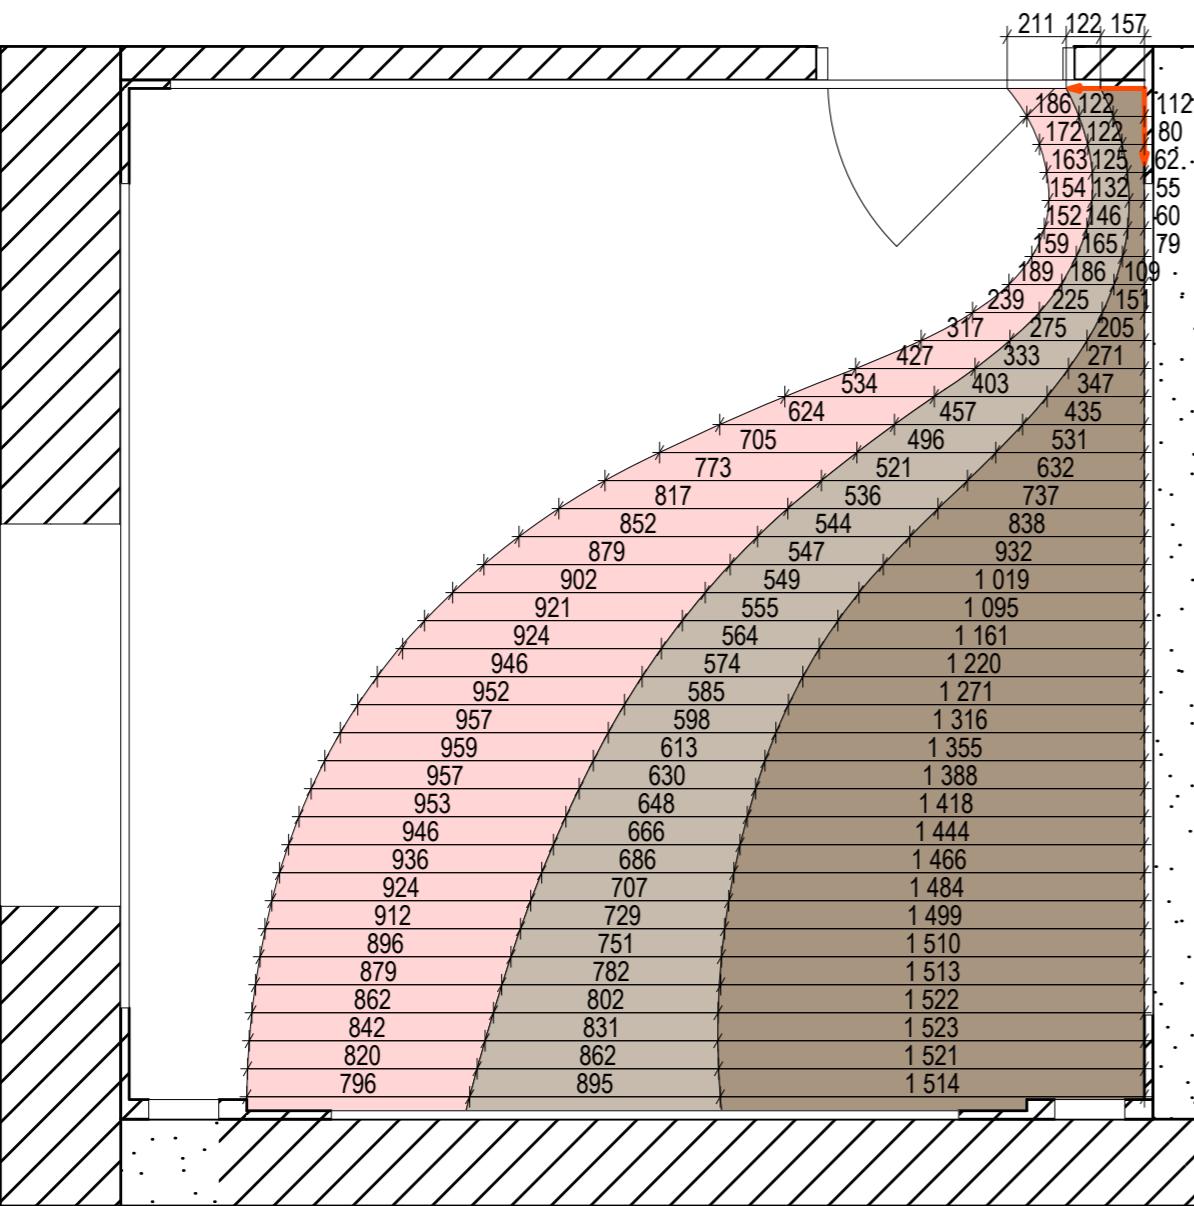

Согласовано

Инв. № подл.	Подл. и дата	Взам. инд. №



Примечания:

- Шаг лекальных линий 100 мм.
- Начало лекальных линий обозначено на плане.

Изм.	Кол.уч	Лист	№ док	Подп.	Дата
Разработал					
ГАП					
ГИП					
Чертит					
Дата изменения					
Заказчик					

Заказчик:

Адрес:

Стадия

Лист

Листов


P

20

34

Лекальные линии потолка

Разрезы потолка 1-1; 2-2;
Высота потолка - 2955 мм. Общая площадь - 142.27 кв.м.

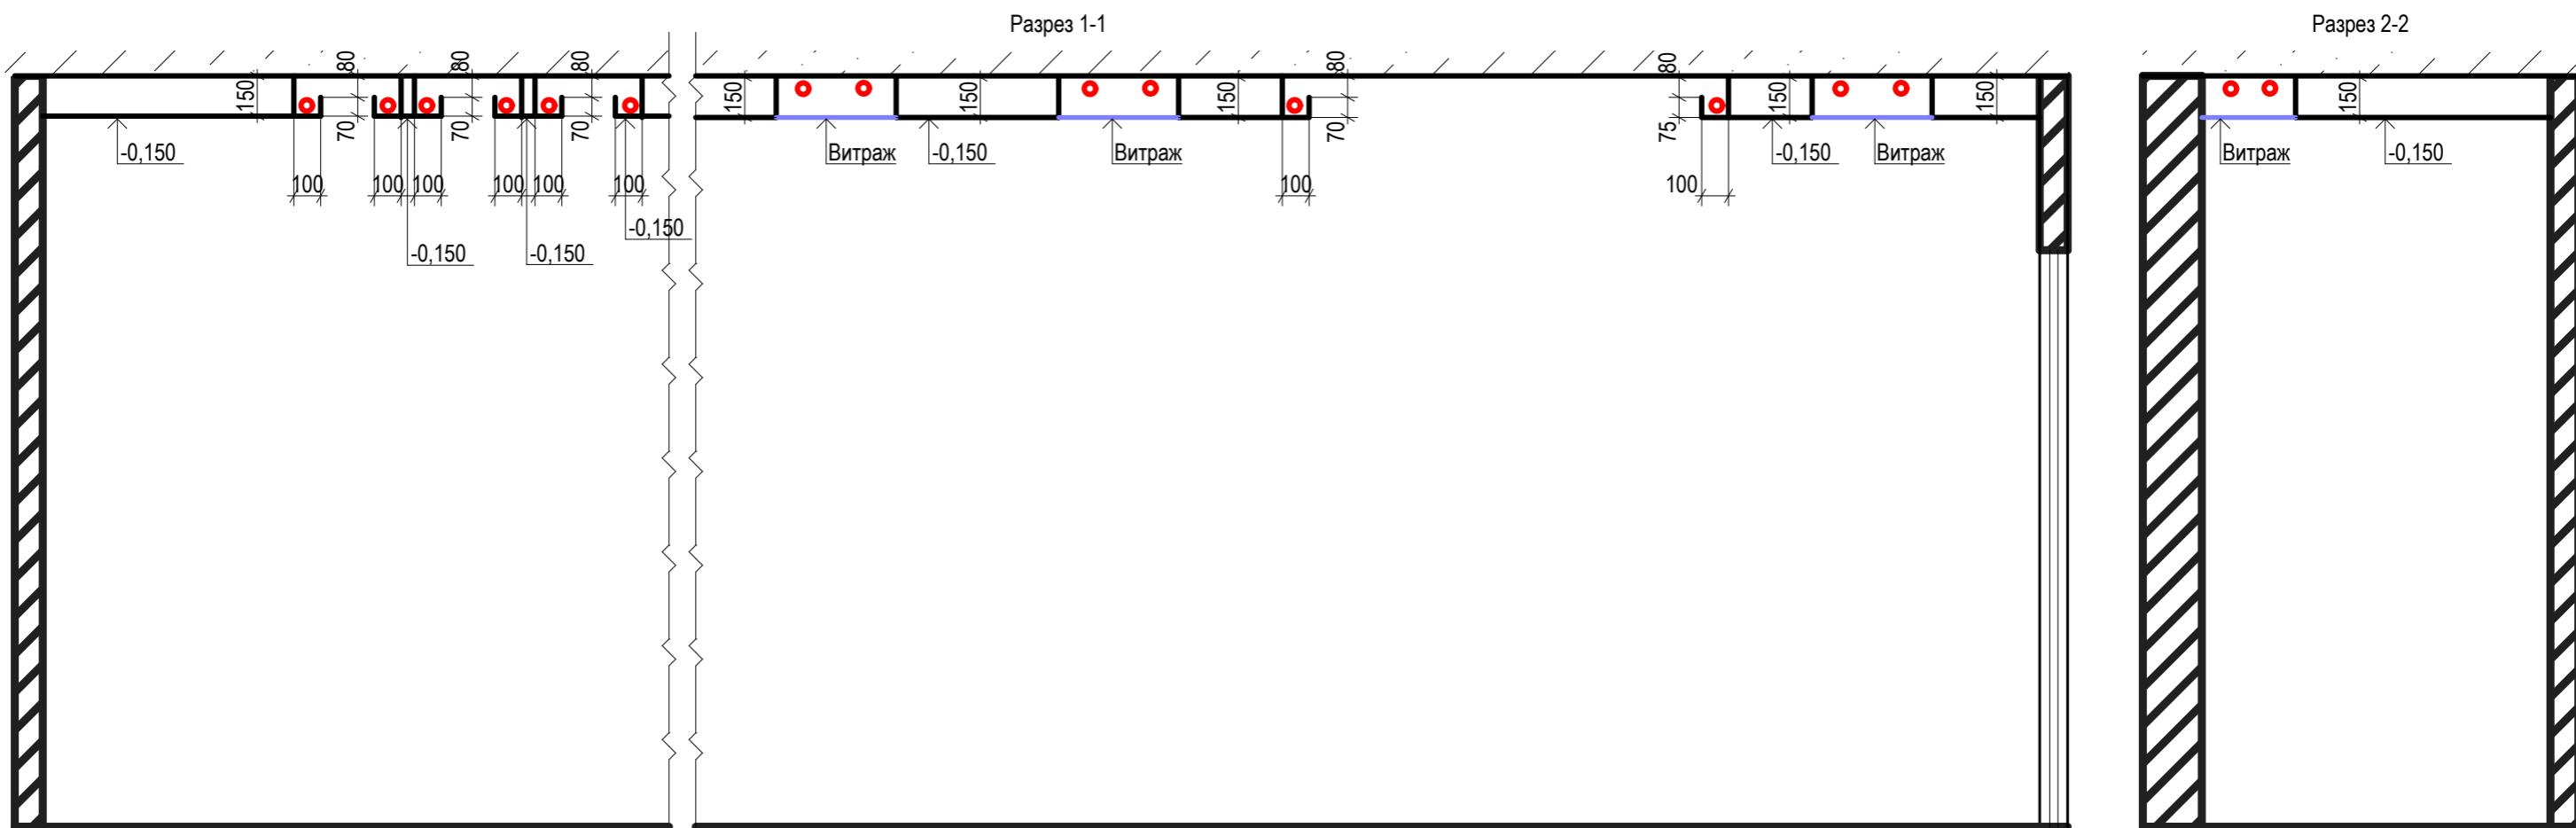

Согласовано

Инв. № подп.	Подп. и дата	Взам. инд. №

Изм.	Кол.уч	Лист	№ док	Подп.	Дата
Разработал					
ГАП					
ГИП					
Чертил					
Дата изменения					
Заказчик					





Заказчик:

Адрес:

Стадия	Лист	Листов
P	21	34

Разрезы потолка 1-1; 2-2;

Разрезы потолка 3-3; 4-4; 5-5; 6-6;
Высота потолка - 2955 мм. Общая площадь - 142.27 кв.м.

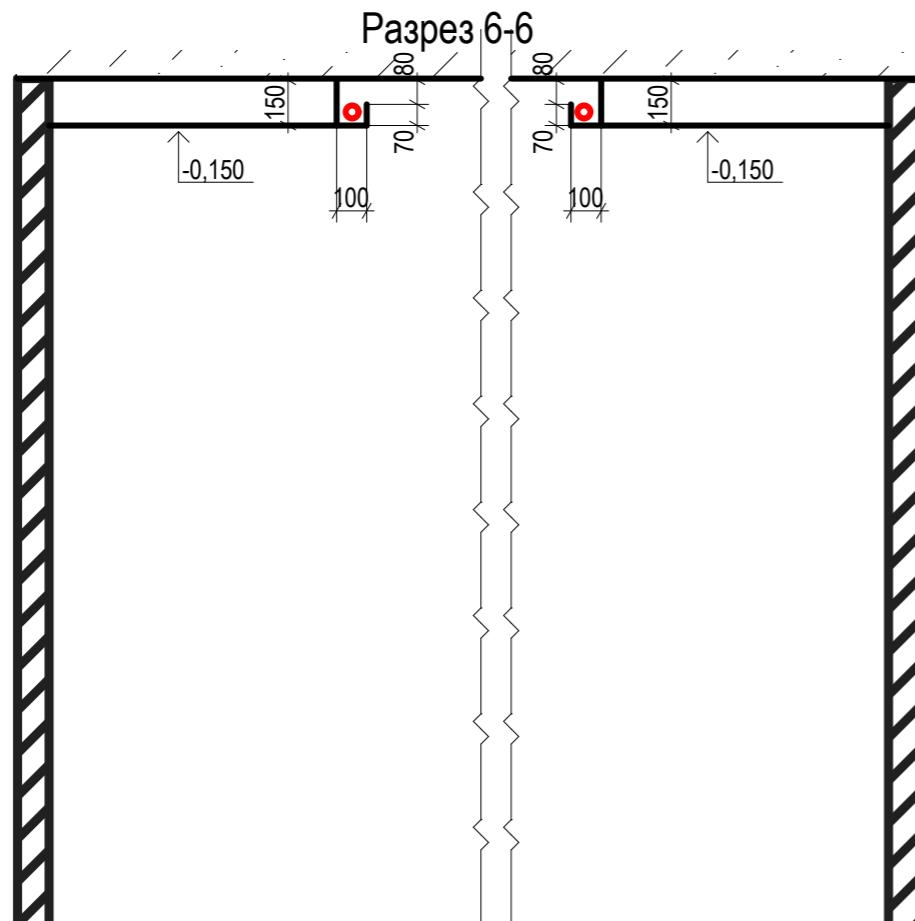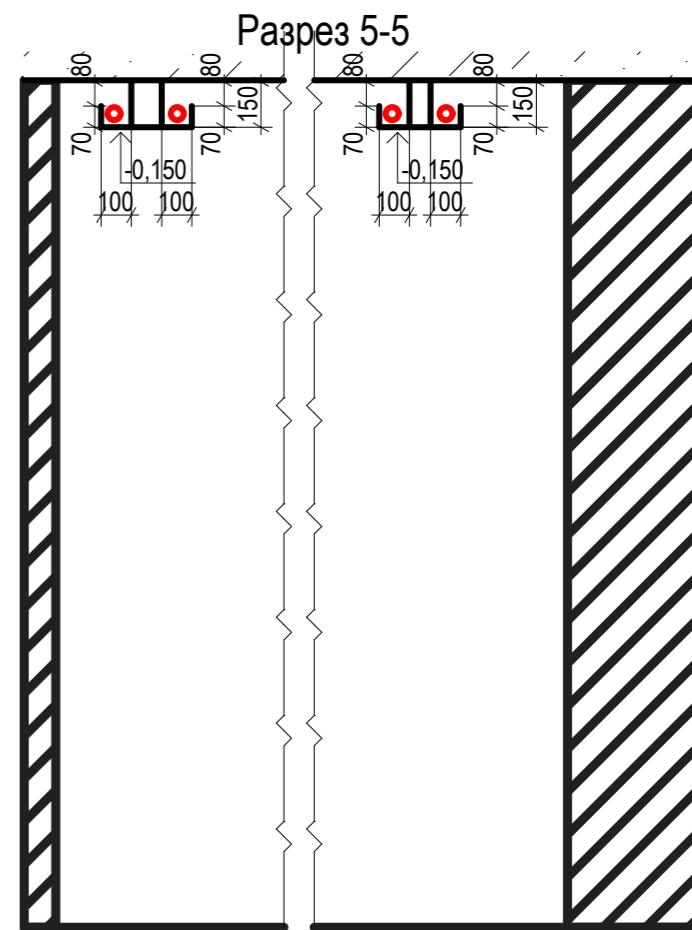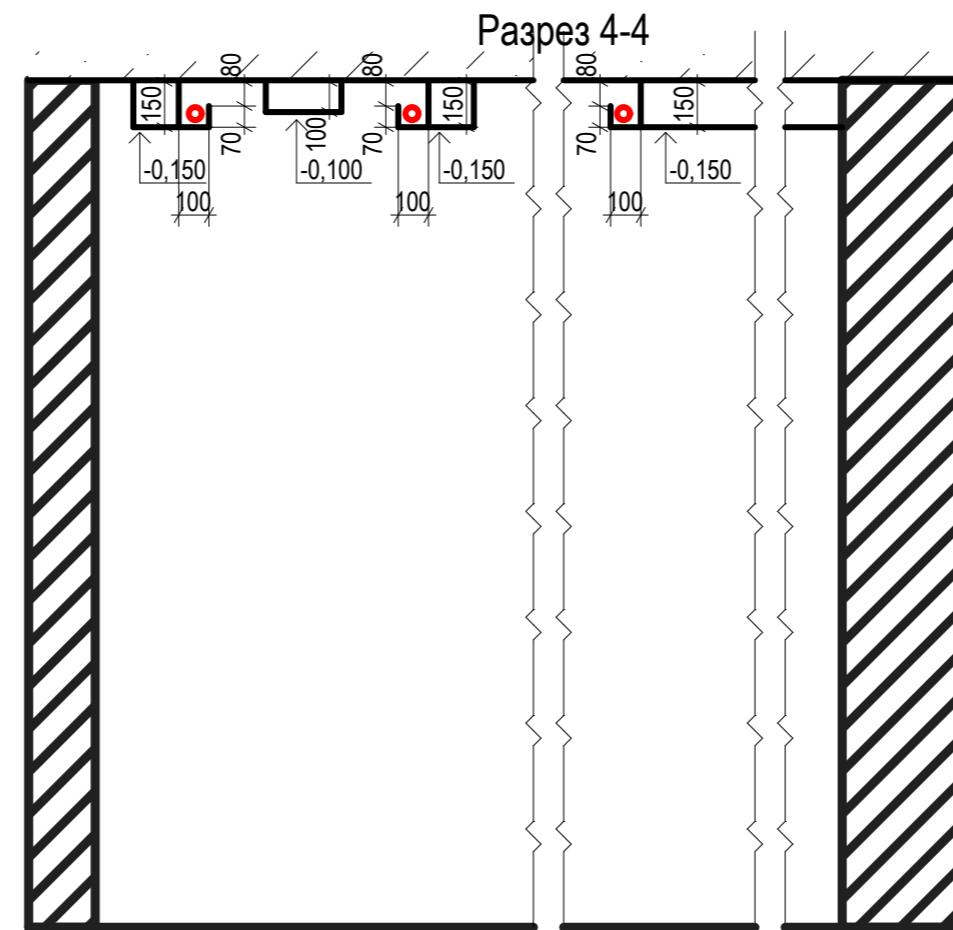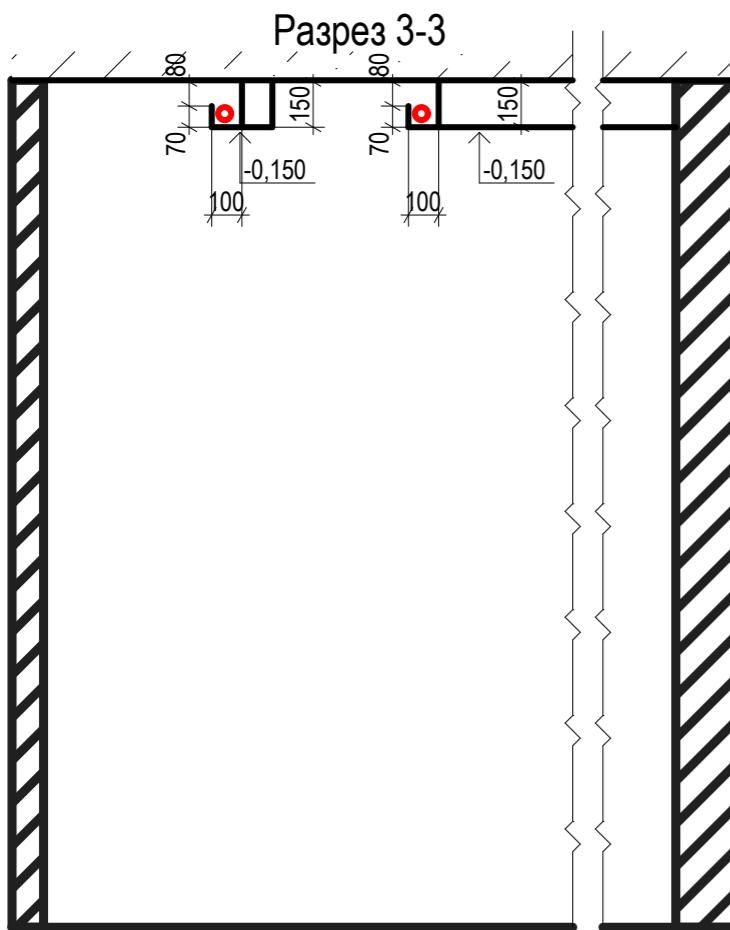

Согласовано			
Инв. № подп.	Подп. и дата	Взам. инд. №	




Изм.	Кол.уч	Лист	№ док	Подп.	Дата
Разработал					
ГАП					
ГИП					
Чертит					
Дата изменения					
Заказчик					

Заказчик:

Адрес:

Стадия	Лист	Листов
P	22	34

Разрезы потолка 3-3; 4-4; 5-5; 6-6;

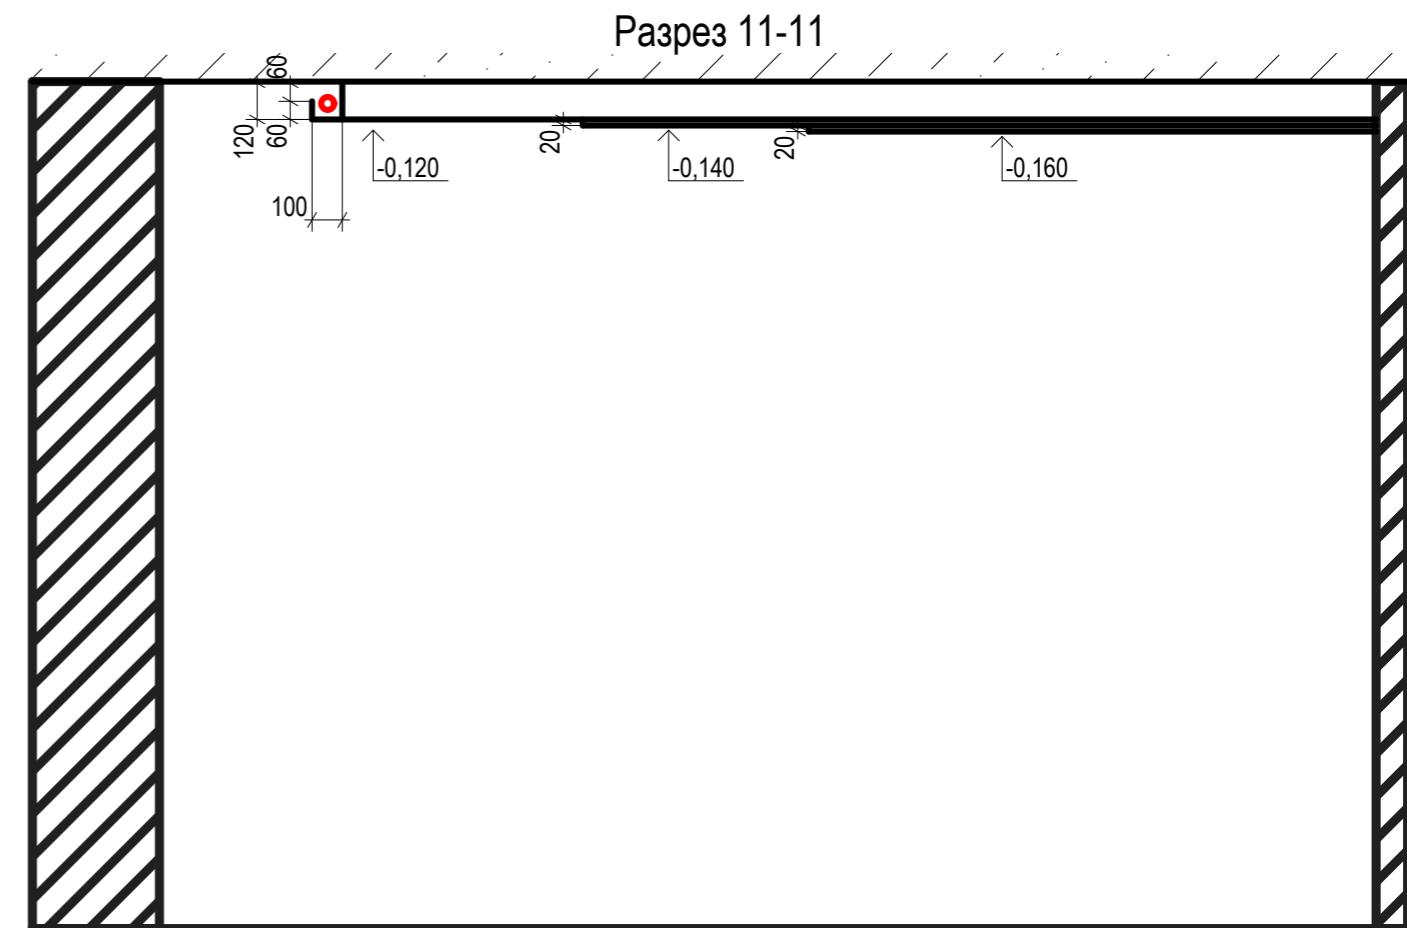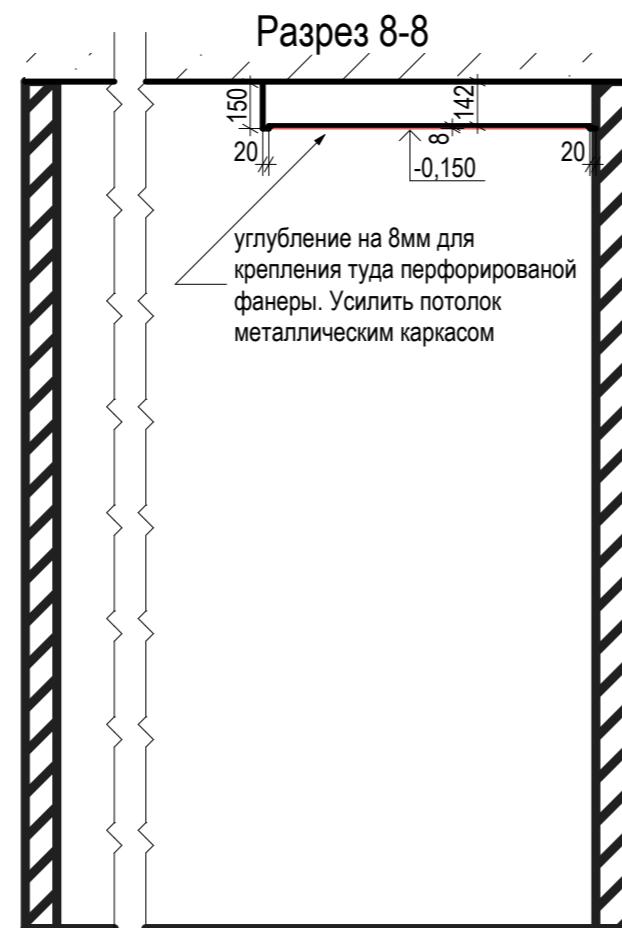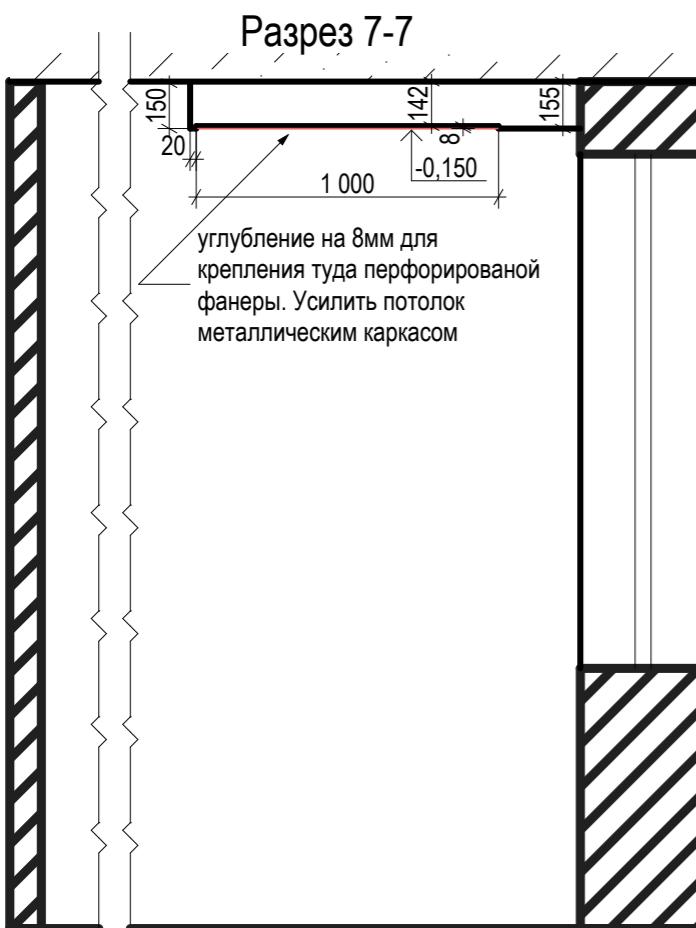

Согласовано			



Инв. № подп.	Подп. и дата	Взам. инд. №

Заказчик:

Адрес: Стадия Лист Листов
Р 23 34

Разрезы потолка 7-7; 8-8; 11-11;

Разрезы потолка 9-9; 10-10;
Высота потолка - 2955 мм. Общая площадь - 142.27 кв.м.

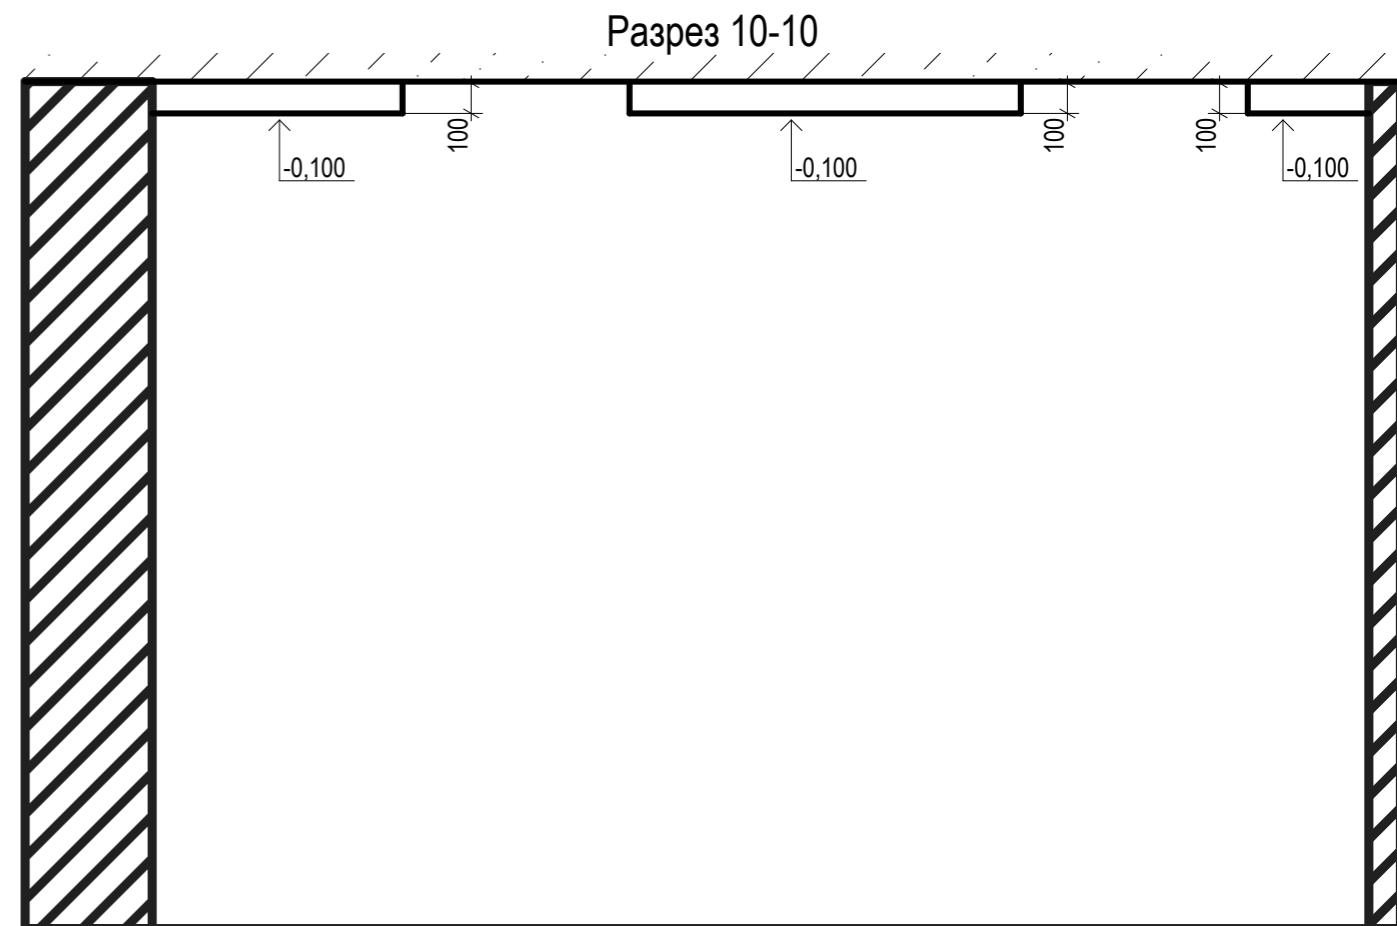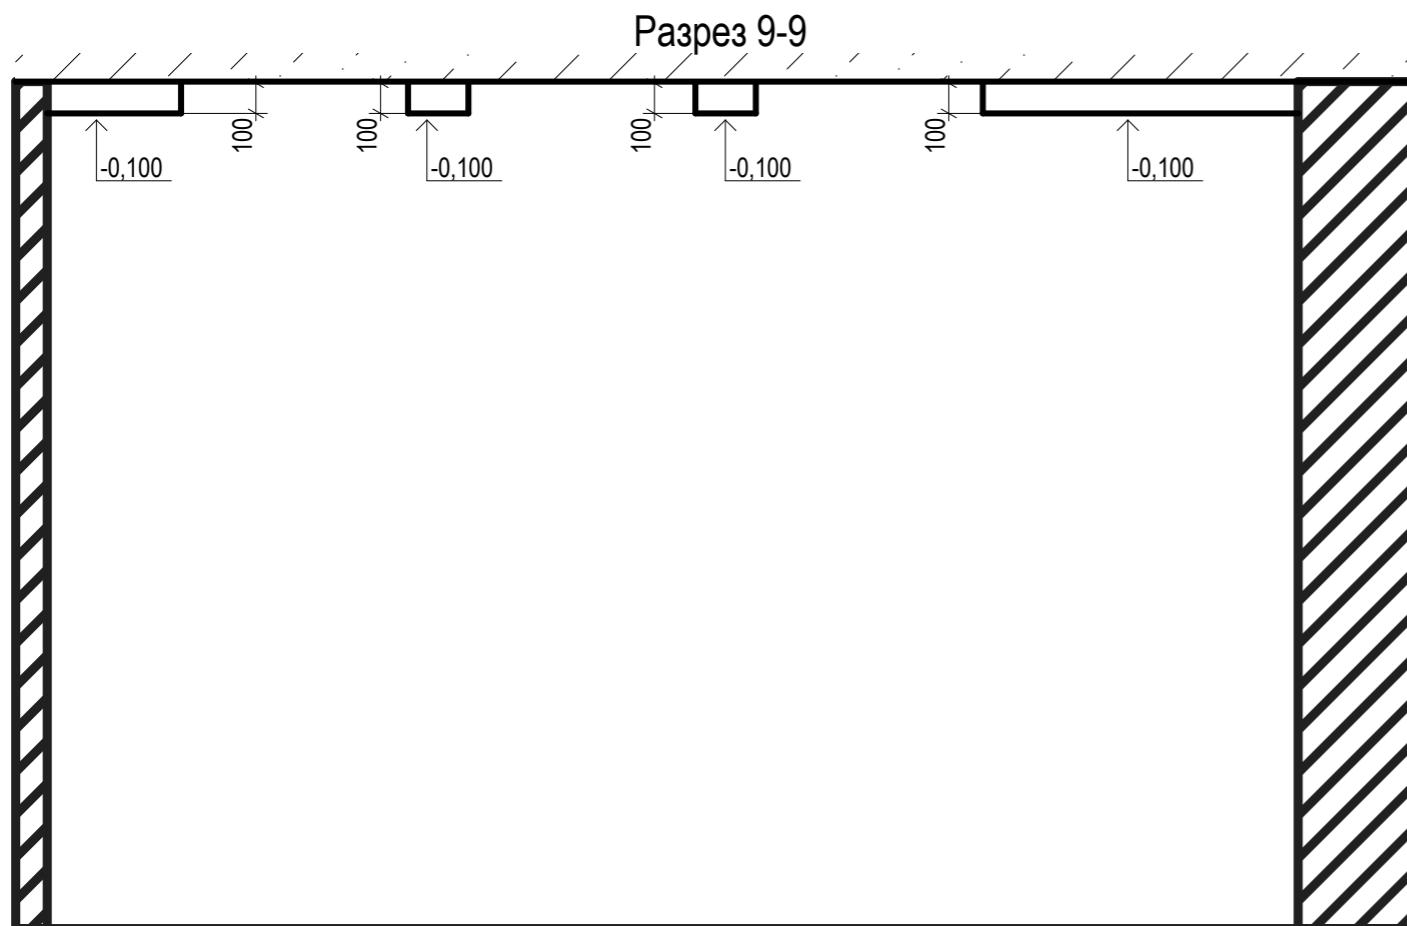

Согласовано			

Инв. № подп.	Подп. и дата	Взам. инд. №

Изм.	Кол.уч	Лист	№ док	Подп.	Дата
Разработал					
ГАП					
ГИП					
Чертит					
Дата изменения					
Заказчик					

Заказчик:

Адрес:
Стадия Лист Листов
Р 24 34

Разрезы потолка 9-9; 10-10;

План расположения светильников

Экспликация помещений

N-N	Наименование	Площадь м ²
1	Холл	23,52
2	Гардеробная	3,81
3	Кухня	17,45
4	Утепленная лоджия 1	5,13
5	Гостиная	21,36
6	Утепленная лоджия 2	7,65
7	Детская 1	13,18
8	Детская 2	16,17
9	Утепленная лоджия 3	4,16
10	Спальня	13,20
11	Утепленная лоджия 4	4,56
12	сан.узел 1	5,73
13	сан.узел 2	5,35
Всего		141,27

Условные обозначения:


№ п/п	Обознач. на плане	Наименование
01		Встроенный светильник 220 В
02		IP44/IP65 низковольтный
03		Светильник потолочный
04		Светильник потолочный IP44
05		Люстра
06		Бра
07		Бра IP44
08		Светодиодная лента
09		Электрорывывод
10		Вентилятор
11		ЭлектроЩит

Заказчик:

Изм.	Кол.уч	Лист	№ док	Подп.	Дата
Разработал					
АП					
ИП					
ертил					
ата изменения					
заказчик					

план расстановки светильников

	Стадия	Лист	Листов
	P	25	34

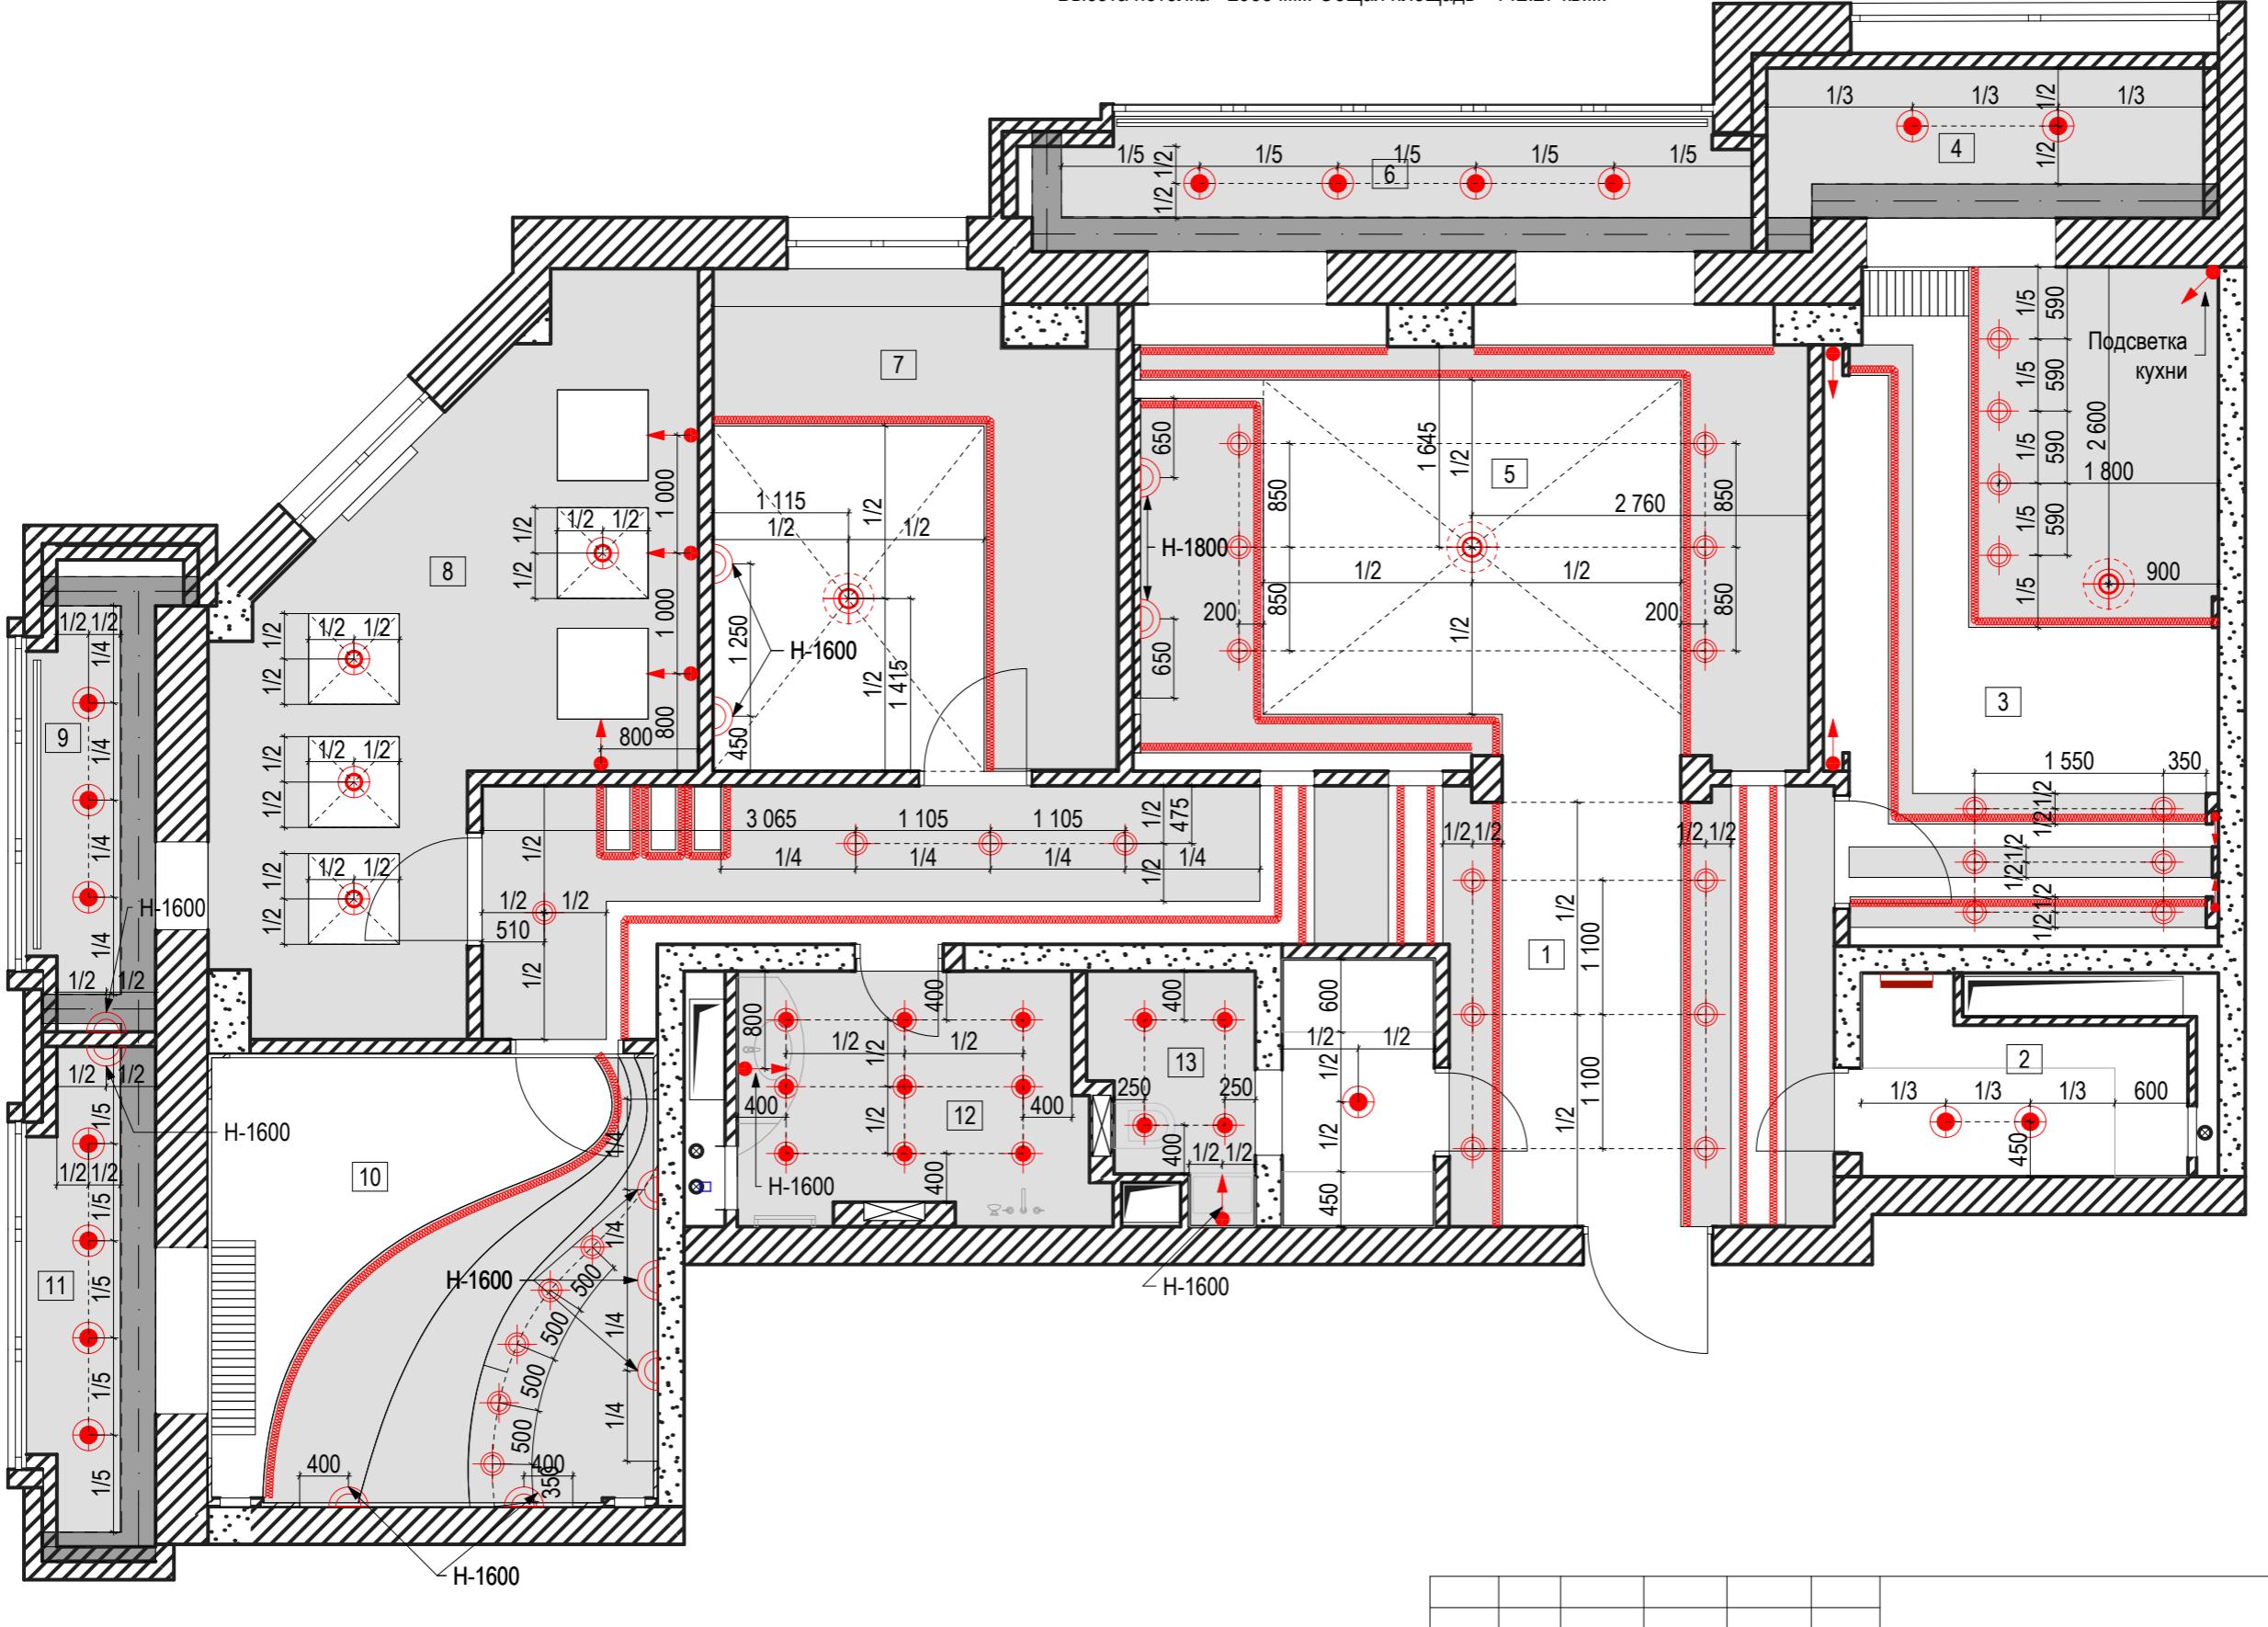

A horizontal number line starting at 0 and ending at M . Tick marks are present at 1000 and 2000.

Инв. № подп.	Подп. и дата	Взам. инд. №


План расстановки выключателей
Высота потолка - 2955 мм. Общая площадь - 142.27 кв.м.

Экспликация помещений

N-N	Наименование	Площадь м ²
1	Холл	23,52
2	Гардеробная	3,81
3	Кухня	17,45
4	Утепленная лоджия 1	5,13
5	Гостиная	21,36
6	Утепленная лоджия 2	7,65
7	Детская 1	13,18
8	Детская 2	16,17
9	Утепленная лоджия 3	4,16
10	Спальня	13,20
11	Утепленная лоджия 4	4,56
12	сан.узел 1	5,73
13	сан.узел 2	5,35
	Всего	141,27

Условные обозначения:

№ п/п	Обознач. на плане	Наименование
01	● ●	Встроенный светильник
02	○ ○ ●	Светильник потолочный
03	○ ○ ○	Люстра
04	○ ○ ○ ○	Бра
05	— — —	Светодиодная лента
06	● →	Электропровод
07	※	Вентилятор
08	— —	Электрощит
09	δ	Выключатель одноклавишный
10	δ δ	Выключатель двухклавишный
11	δ ↗	Одноклавишный проходной
11	δ ↘	Двухклавишный проходной

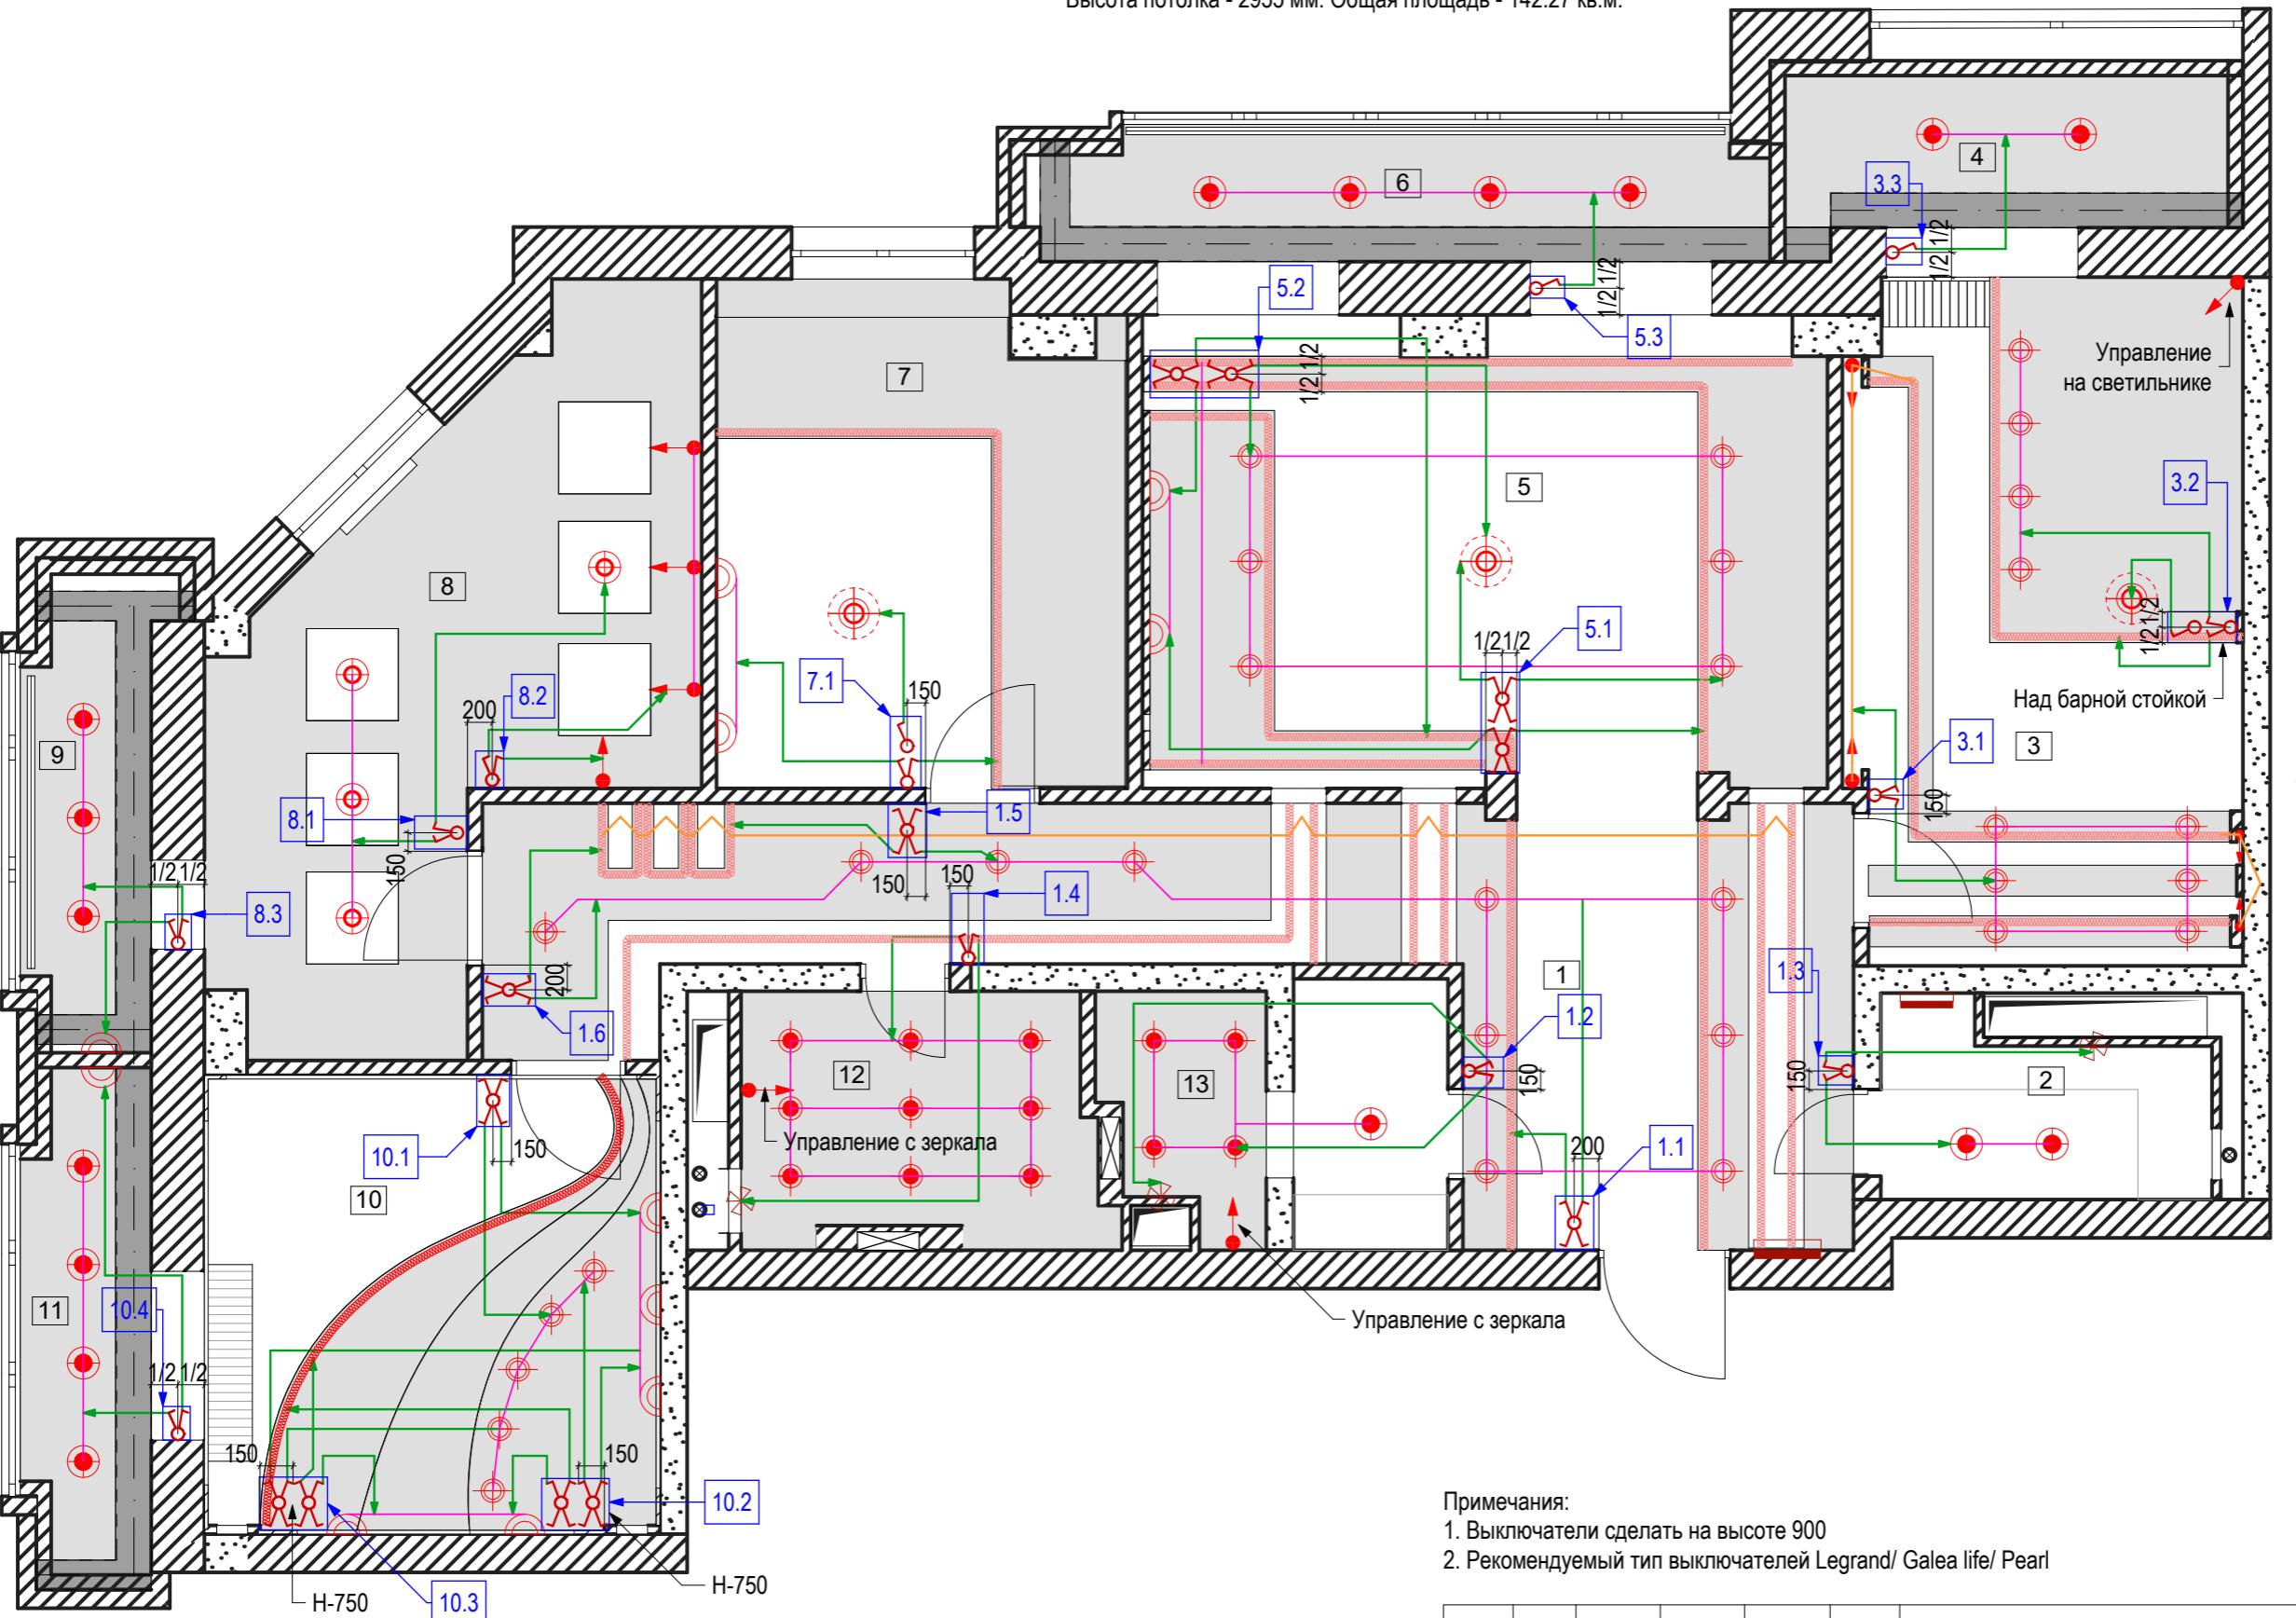

- Примечания:
 1. Выключатели сделать на высоте 900
 2. Рекомендуемый тип выключателей Legrand/ Galea life/ Pearl

Изв.	Кол.уч	Лист	№ док	Подп.	Дата	Адрес:	Стадия	Лист	Листов
Разработал									
ГАП									
ГИП									
Чертит									
Дата изменения									
Заказчик									

План расстановки выключателей

0 1000 2000 м

Согласовано

Взам. инд. №


Подп. и дата

Инв. № подп.

План расстановки электропроводов, силовых и слаботочных

Высота потолка - 2955 мм. Общая площадь - 142.27 кв.м.

Экспликация помещений

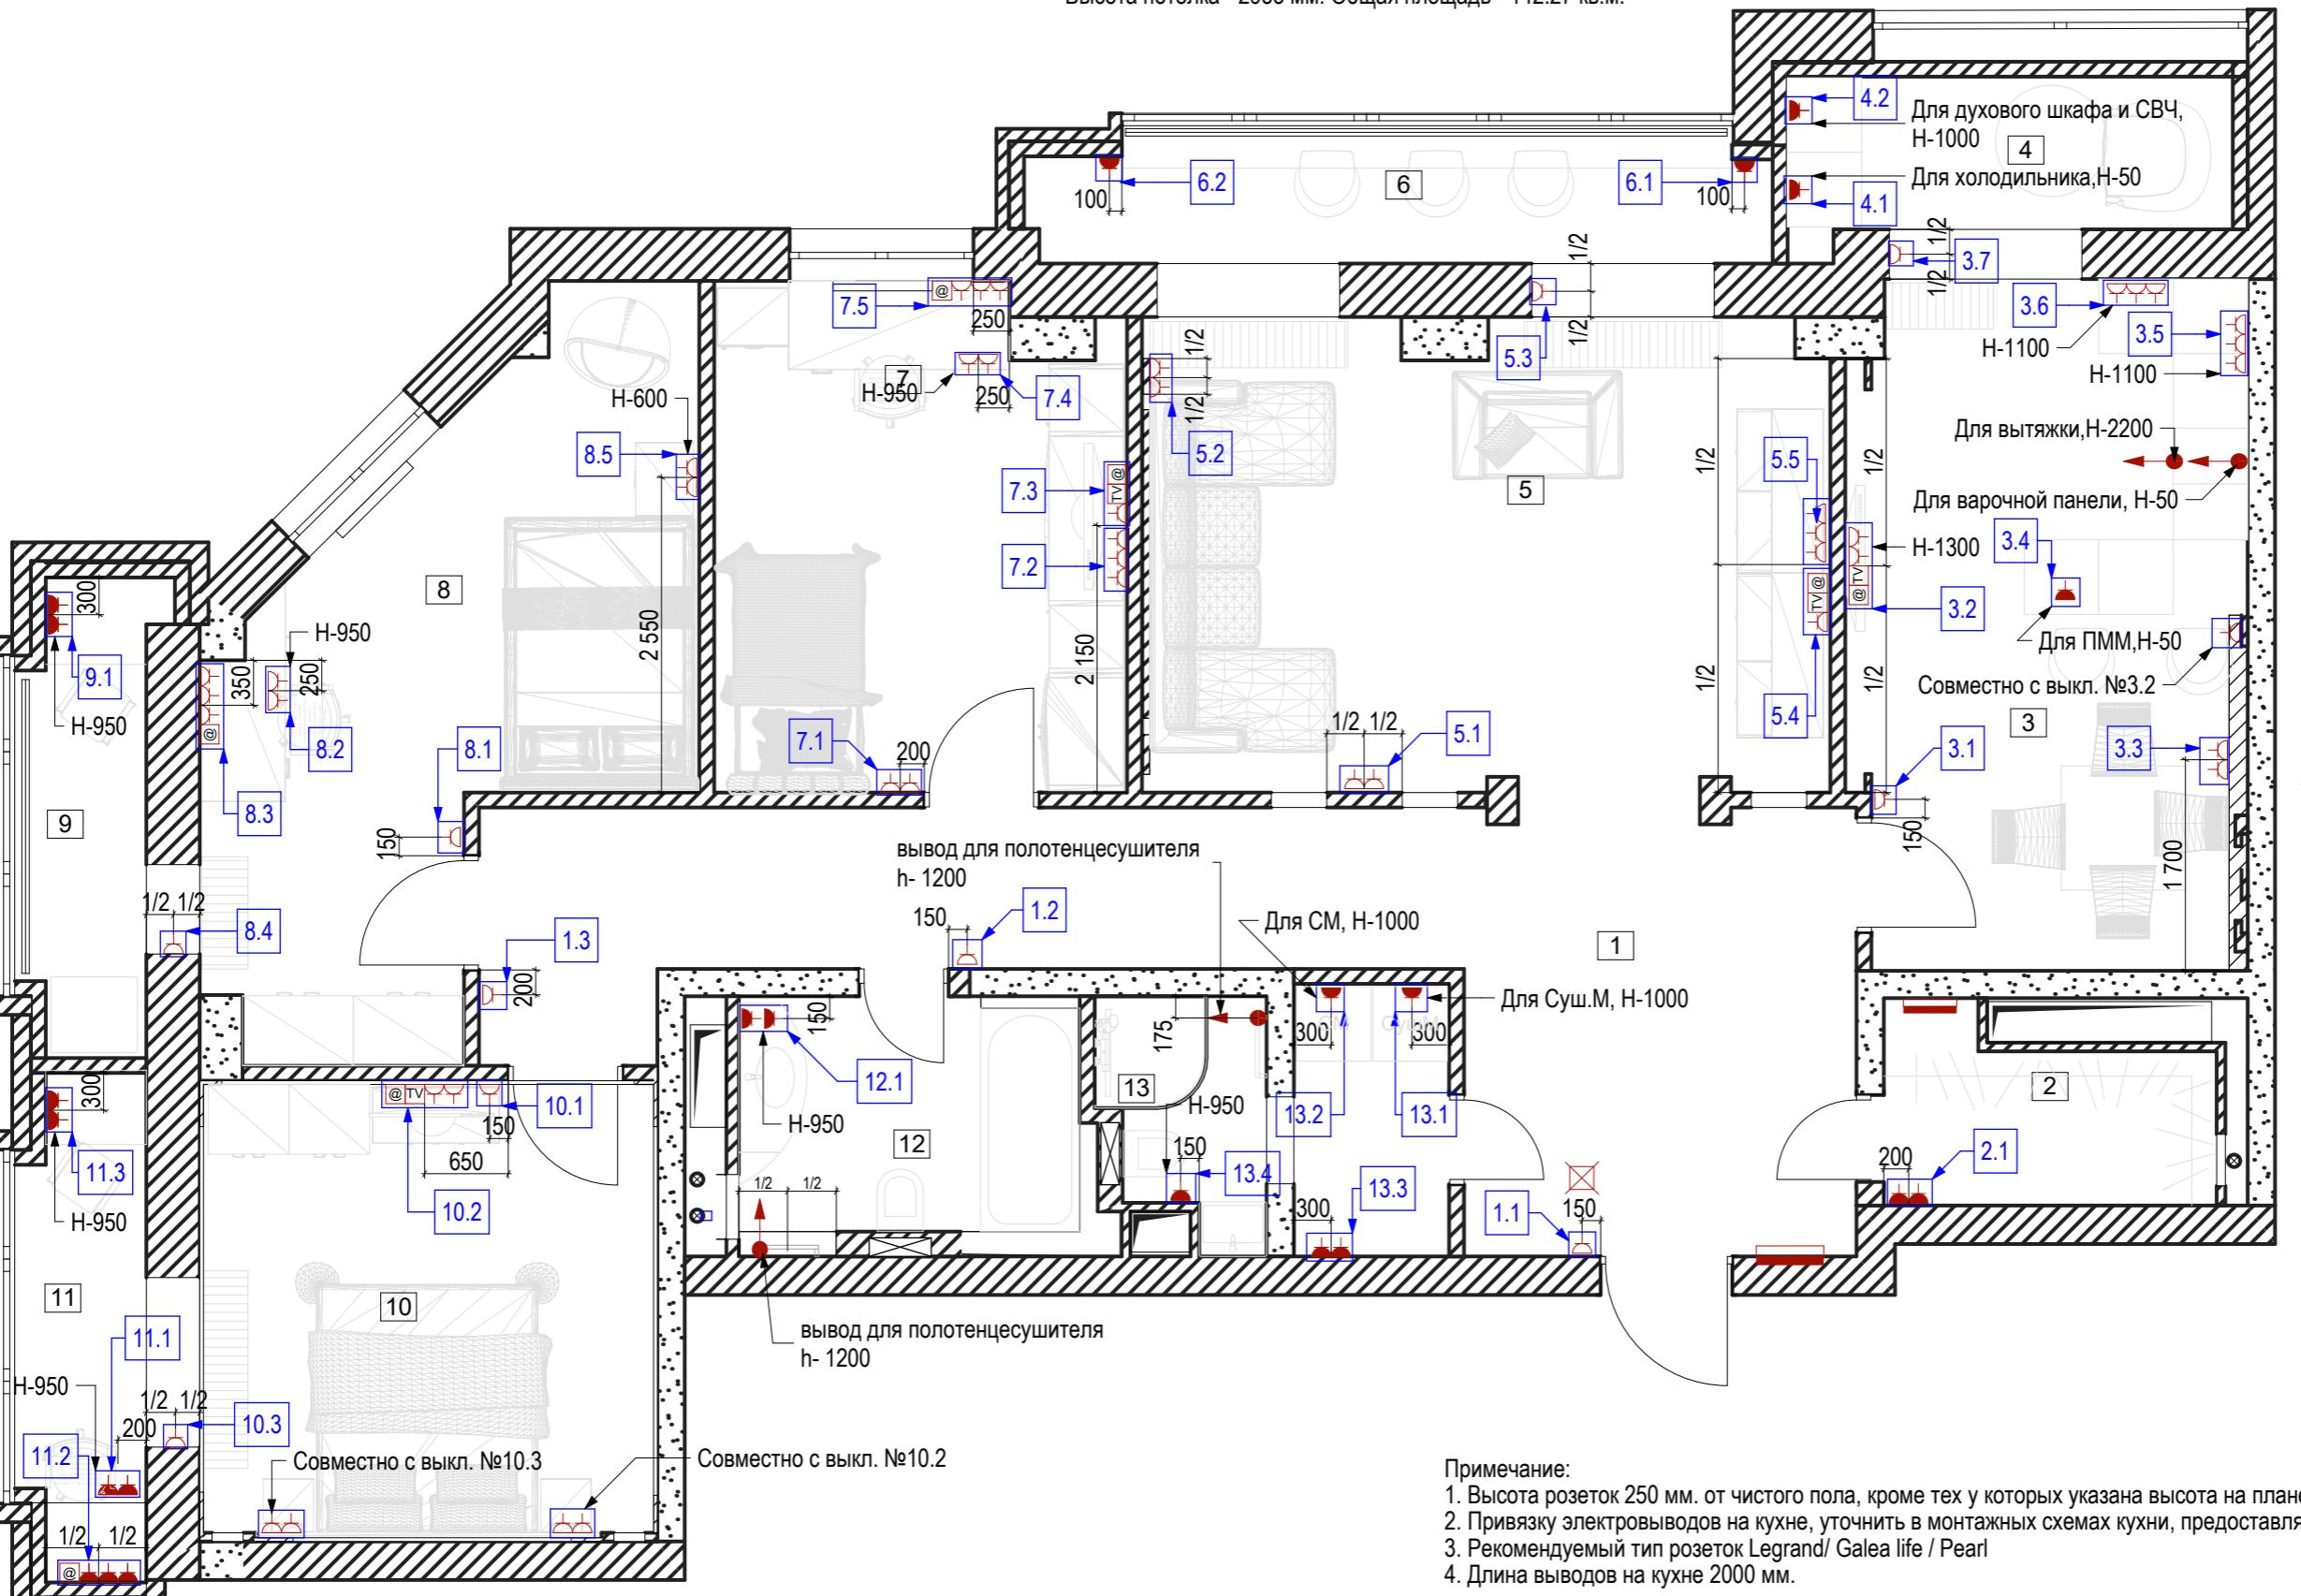

Примечание:

- Высота розеток 250 мм. от чистого пола, кроме тех у которых указана высота на плане.
- Привязку электропроводов на кухне, уточнить в монтажных схемах кухни, предоставляемых заказчиком.
- Рекомендуемый тип розеток Legrand/ Galea life / Pearl
- Длина выводов на кухне 2000 мм.

N-N	Наименование	Площадь м2
1	Холл	23,52
2	Гардеробная	3,81
3	Кухня	17,45
4	Утепленная лоджия 1	5,13
5	Гостиная	21,36
6	Утепленная лоджия 2	7,65
7	Детская 1	13,18
8	Детская 2	16,17
9	Утепленная лоджия 3	4,16
10	Спальня	13,20
11	Утепленная лоджия 4	4,56
12	сан.узел 1	5,73
13	сан.узел 2	5,35
Условные обозначения:		141,27

Условные обозначения:

№ п/п	Обознач. на плане	Наименование
01	△	Розетка эл. 220V
02	■	Розетка эл. IP-44
03	TV	Телевизионная розетка
04	RH	Розетка телефонная
05	@	Розетка интернет
06	K	Кабельканал
07	→●	Электро вывод
08	—	Электро щит
09	☒	Домофон

Заказчик:

Изм.	Кол.уч	Лист	№ док	Подп.	Дата	Адрес:	Стадия	Лист	Листов
Разработал									
ГАП									
ГИП									
Чертит									
Дата изменения									
Заказчик									
План расстановки электропроводов, силовых и слаботочных									

Согласовано

Изв. № подп.	Подп. и дата	Взам. инд. №
--------------	--------------	--------------

0 1000 2000 м

Компоновка внешней электрофурнитуры

Высота потолка - 2955 мм. Общая площадь - 142.27 кв.м.

Розетки

1.1	
1.2	
1.3	
2.1	IP-44
3.1	
3.2	@ TV
3.3	
3.4	IP-44
3.5	
3.6	
3.7	
4.1	IP-44
4.2	IP-44
5.1	
5.2	
5.3	
5.4	@ TV
5.5	
6.1	IP-44
6.2	IP-44
7.1	
7.2	
7.3	@ TV

Розетки

7.4	
7.5	@
8.1	
8.2	
8.3	@
8.4	
8.5	
9.1	IP-44
10.1	
10.2	@ TV
10.3	
11.1	IP-44
11.2	IP-44 @
11.3	IP-44
12.1	IP-44 IP-44
13.1	IP-44
13.2	IP-44
13.3	IP-44
13.3	IP-44

Выключатели

1.1	p
1.2	
1.3	
1.4	
1.5	p
1.6	p
3.1	
3.2	
3.3	
5.1	p p
5.2	p p
5.3	p
7.1	
8.1	
8.2	
8.3	
10.1	p p
10.2	p p
10.3	p p p p
10.4	

Условные обозначения:


- IP-44 Розетка с повышенной пылевлагозащитой
- тел Телефонная розетка
- тв Телевизионная розетка
- Эл.Розетка
- Выключатель одноклавишный
- p Выключатель одноклавишный проходной
- Выключатель двухклавишный
- p Выключатель двухклавишный проходной
- @ И интернет розетка

Розетки эл.220v - 54 шт.
 Розетки IP-44 - 24 шт.
 Телевизионная розетка - 4 шт.
 Интернет розетка - 7 шт.
 Выключатель одноклавишный - 4 шт.
 Выключатель двухклавишный - 10 шт.
 Выключатель одноклавишный проходной - 0 шт.
 Выключатель двухклавишный проходной - 12 шт.
 Одинарная рамка - 31 шт.
 Двойная рамка - 17 шт.
 Тройная рамка - 7 шт.
 Четырехпозиционная рамка - 7 шт.
 Регулятор теплого пола - 8 шт.

Изв. № подп.	Подп. и дата	Взам. инд. №	Заказчик:				
			Изм.	Кол.уч	Лист	№ док	Подп.
			Разработал				
			ГАП				
			ГИП				
			Чертил				
			Дата изменения				
			Заказчик				
			Адрес:				
			Стадия				
			P		28		34
			Компановка внешней электрофурнитуры				

План расстановки мебели

Высота потолка - 2955 мм. Общая площадь - 142.27 кв.м.

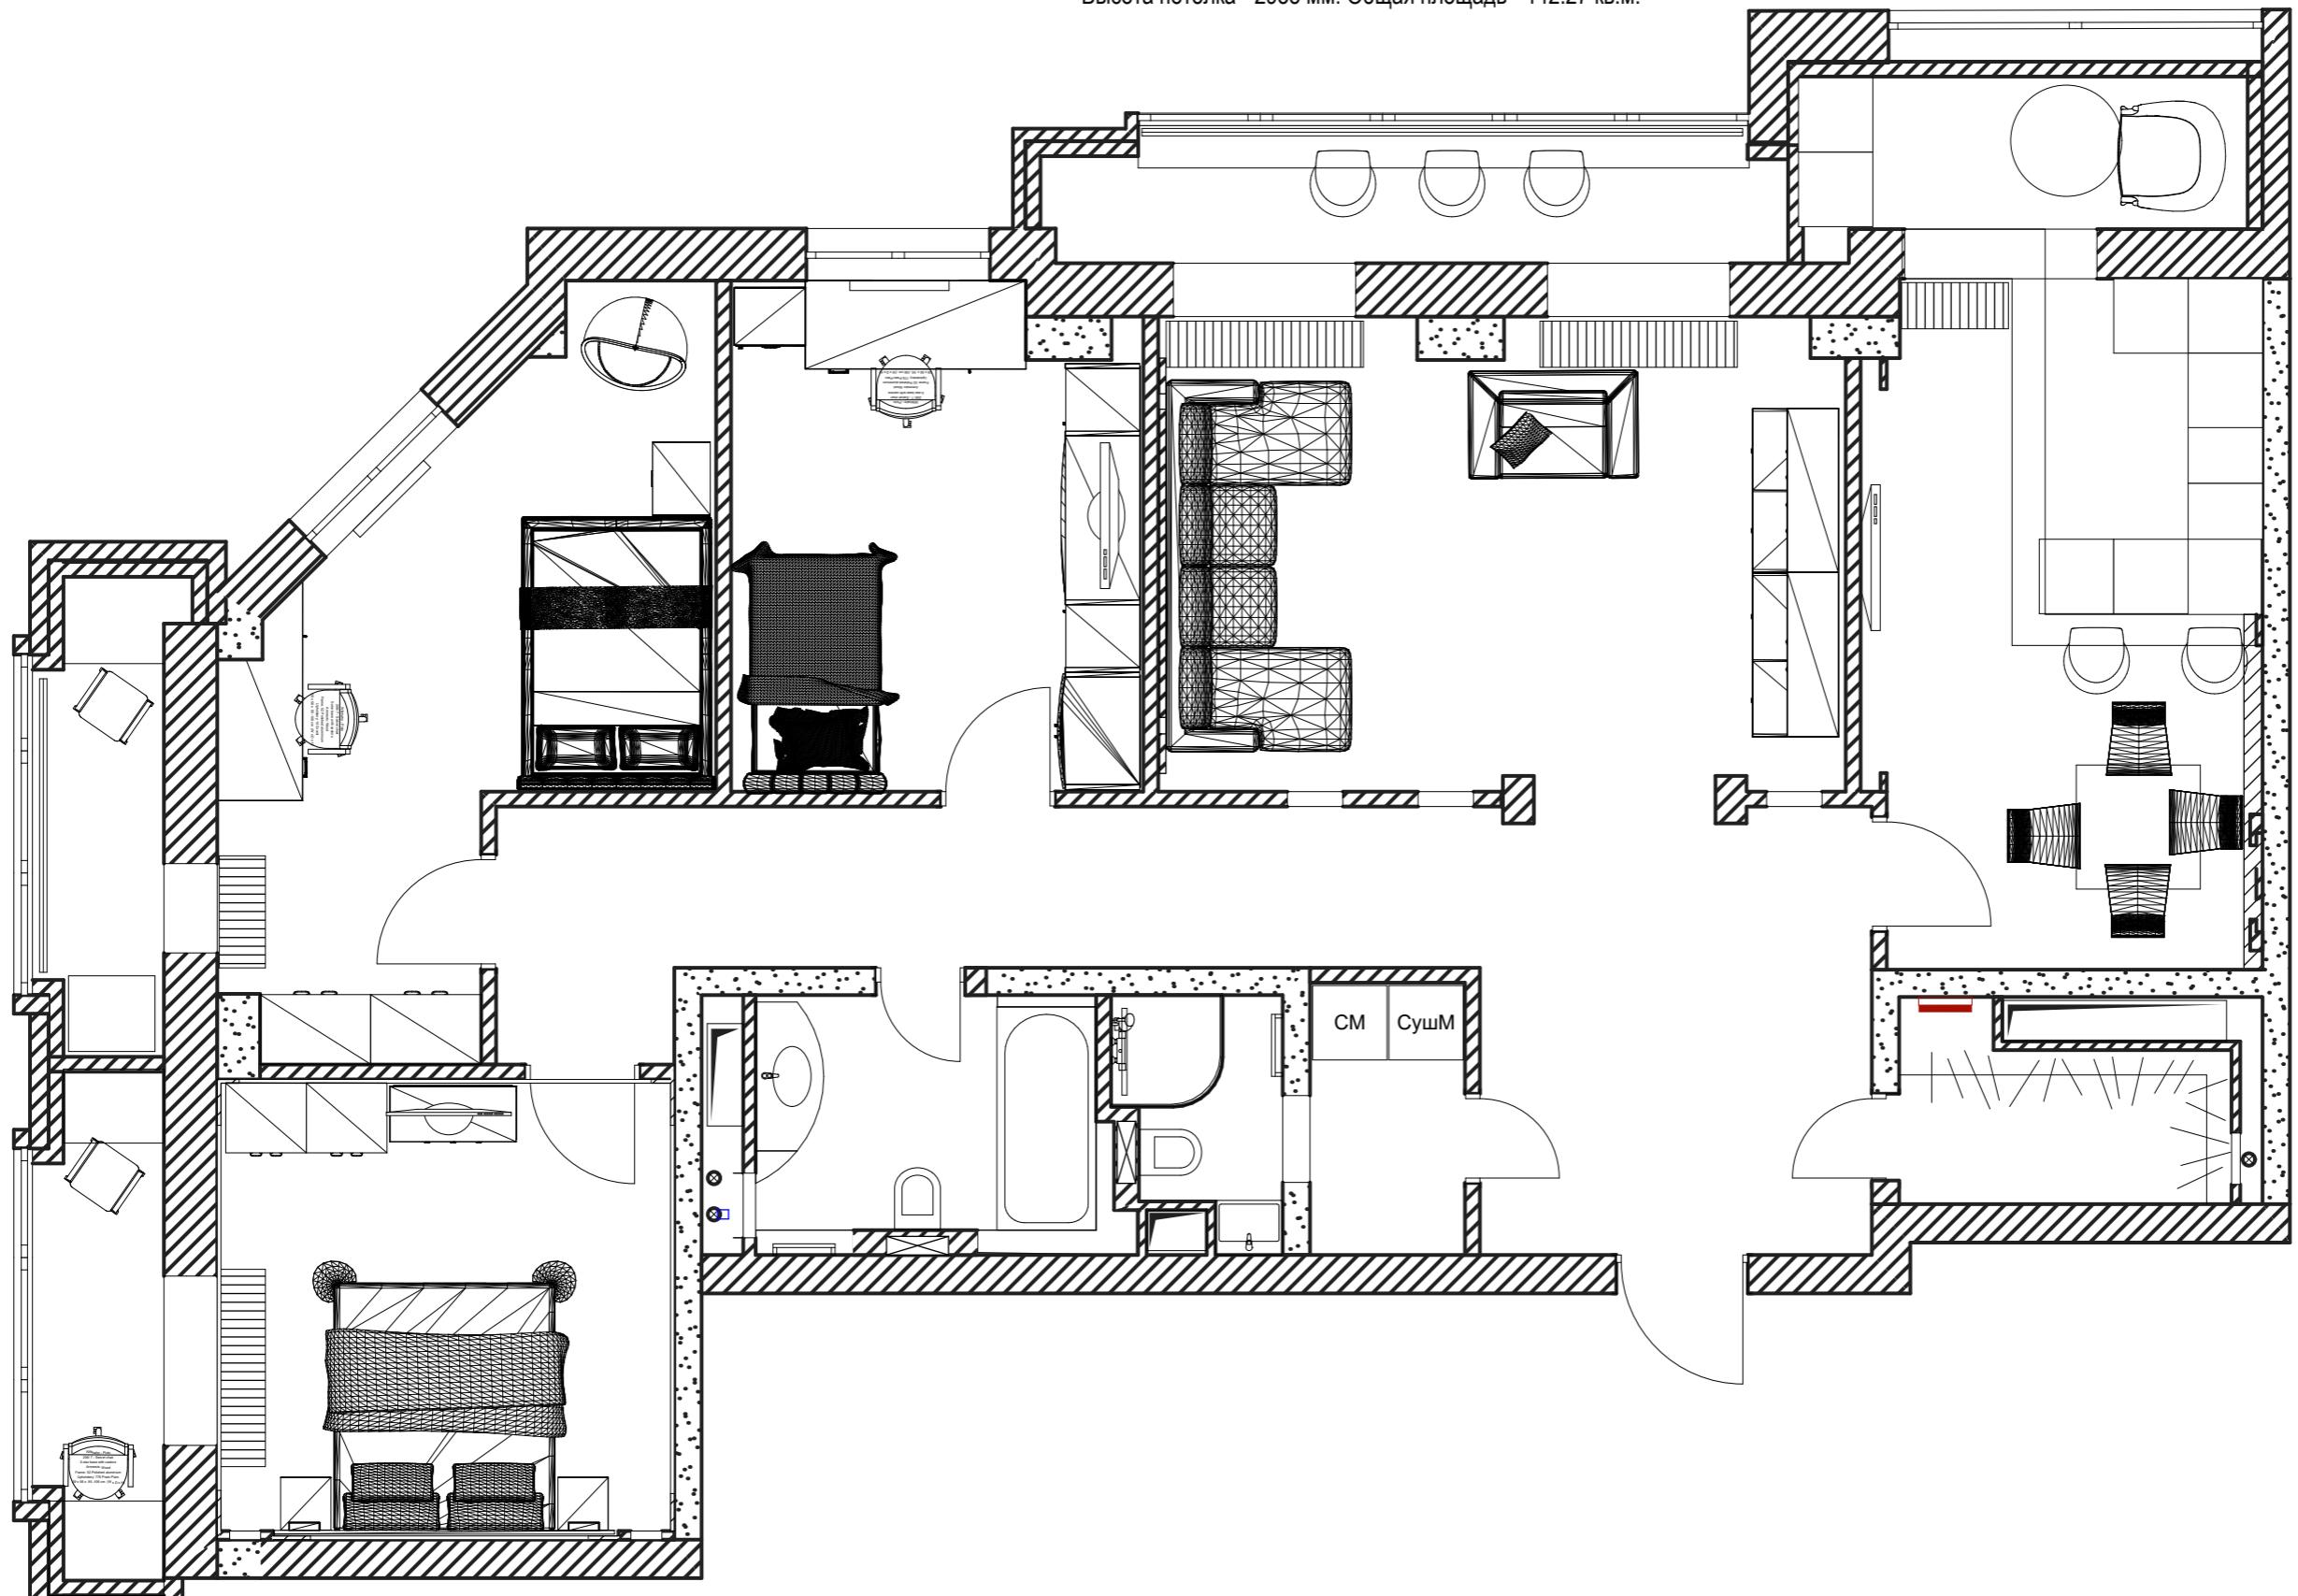

Экспликация помещений

N-N	Наименование	Площадь м ²
1	Холл	23,52
2	Гардеробная	3,81
3	Кухня	17,45
4	Утепленная лоджия 1	5,13
5	Гостиная	21,36
6	Утепленная лоджия 2	7,65
7	Детская 1	13,18
8	Детская 2	16,17
9	Утепленная лоджия 3	4,16
10	Спальня	13,20
11	Утепленная лоджия 4	4,56
12	сан.узел 1	5,73
13	сан.узел 2	5,35
Всего		141,27

Согласовано		
Подп. и дата	Взам. инд. №	
Инв. № подп.		

Изм.	Кол.уч	Лист	№ док	Подп.	Дата	Адрес:	План расстановки мебели
Разработал							
ГАП							
ГИП							
Чертит							
Дата изменения							
Заказчик							

Заказчик:


Стадия Лист Листов
Р 29 34

План отделочных материалов

Высота потолка - 2955 мм. Общая площадь - 142.27 кв.м.

Экспликация помещений

N-N	Наименование	Площадь м ²
1	Холл	23,52
2	Гардеробная	3,81
3	Кухня	17,45
4	Утепленная лоджия 1	5,13
5	Гостиная	21,36
6	Утепленная лоджия 2	7,65
7	Детская 1	13,18
8	Детская 2	16,17
9	Утепленная лоджия 3	4,16
10	Спальня	13,20
11	Утепленная лоджия 4	4,56
12	сан.узел 1	5,73
13	сан.узел 2	5,35
	Всего	141,27

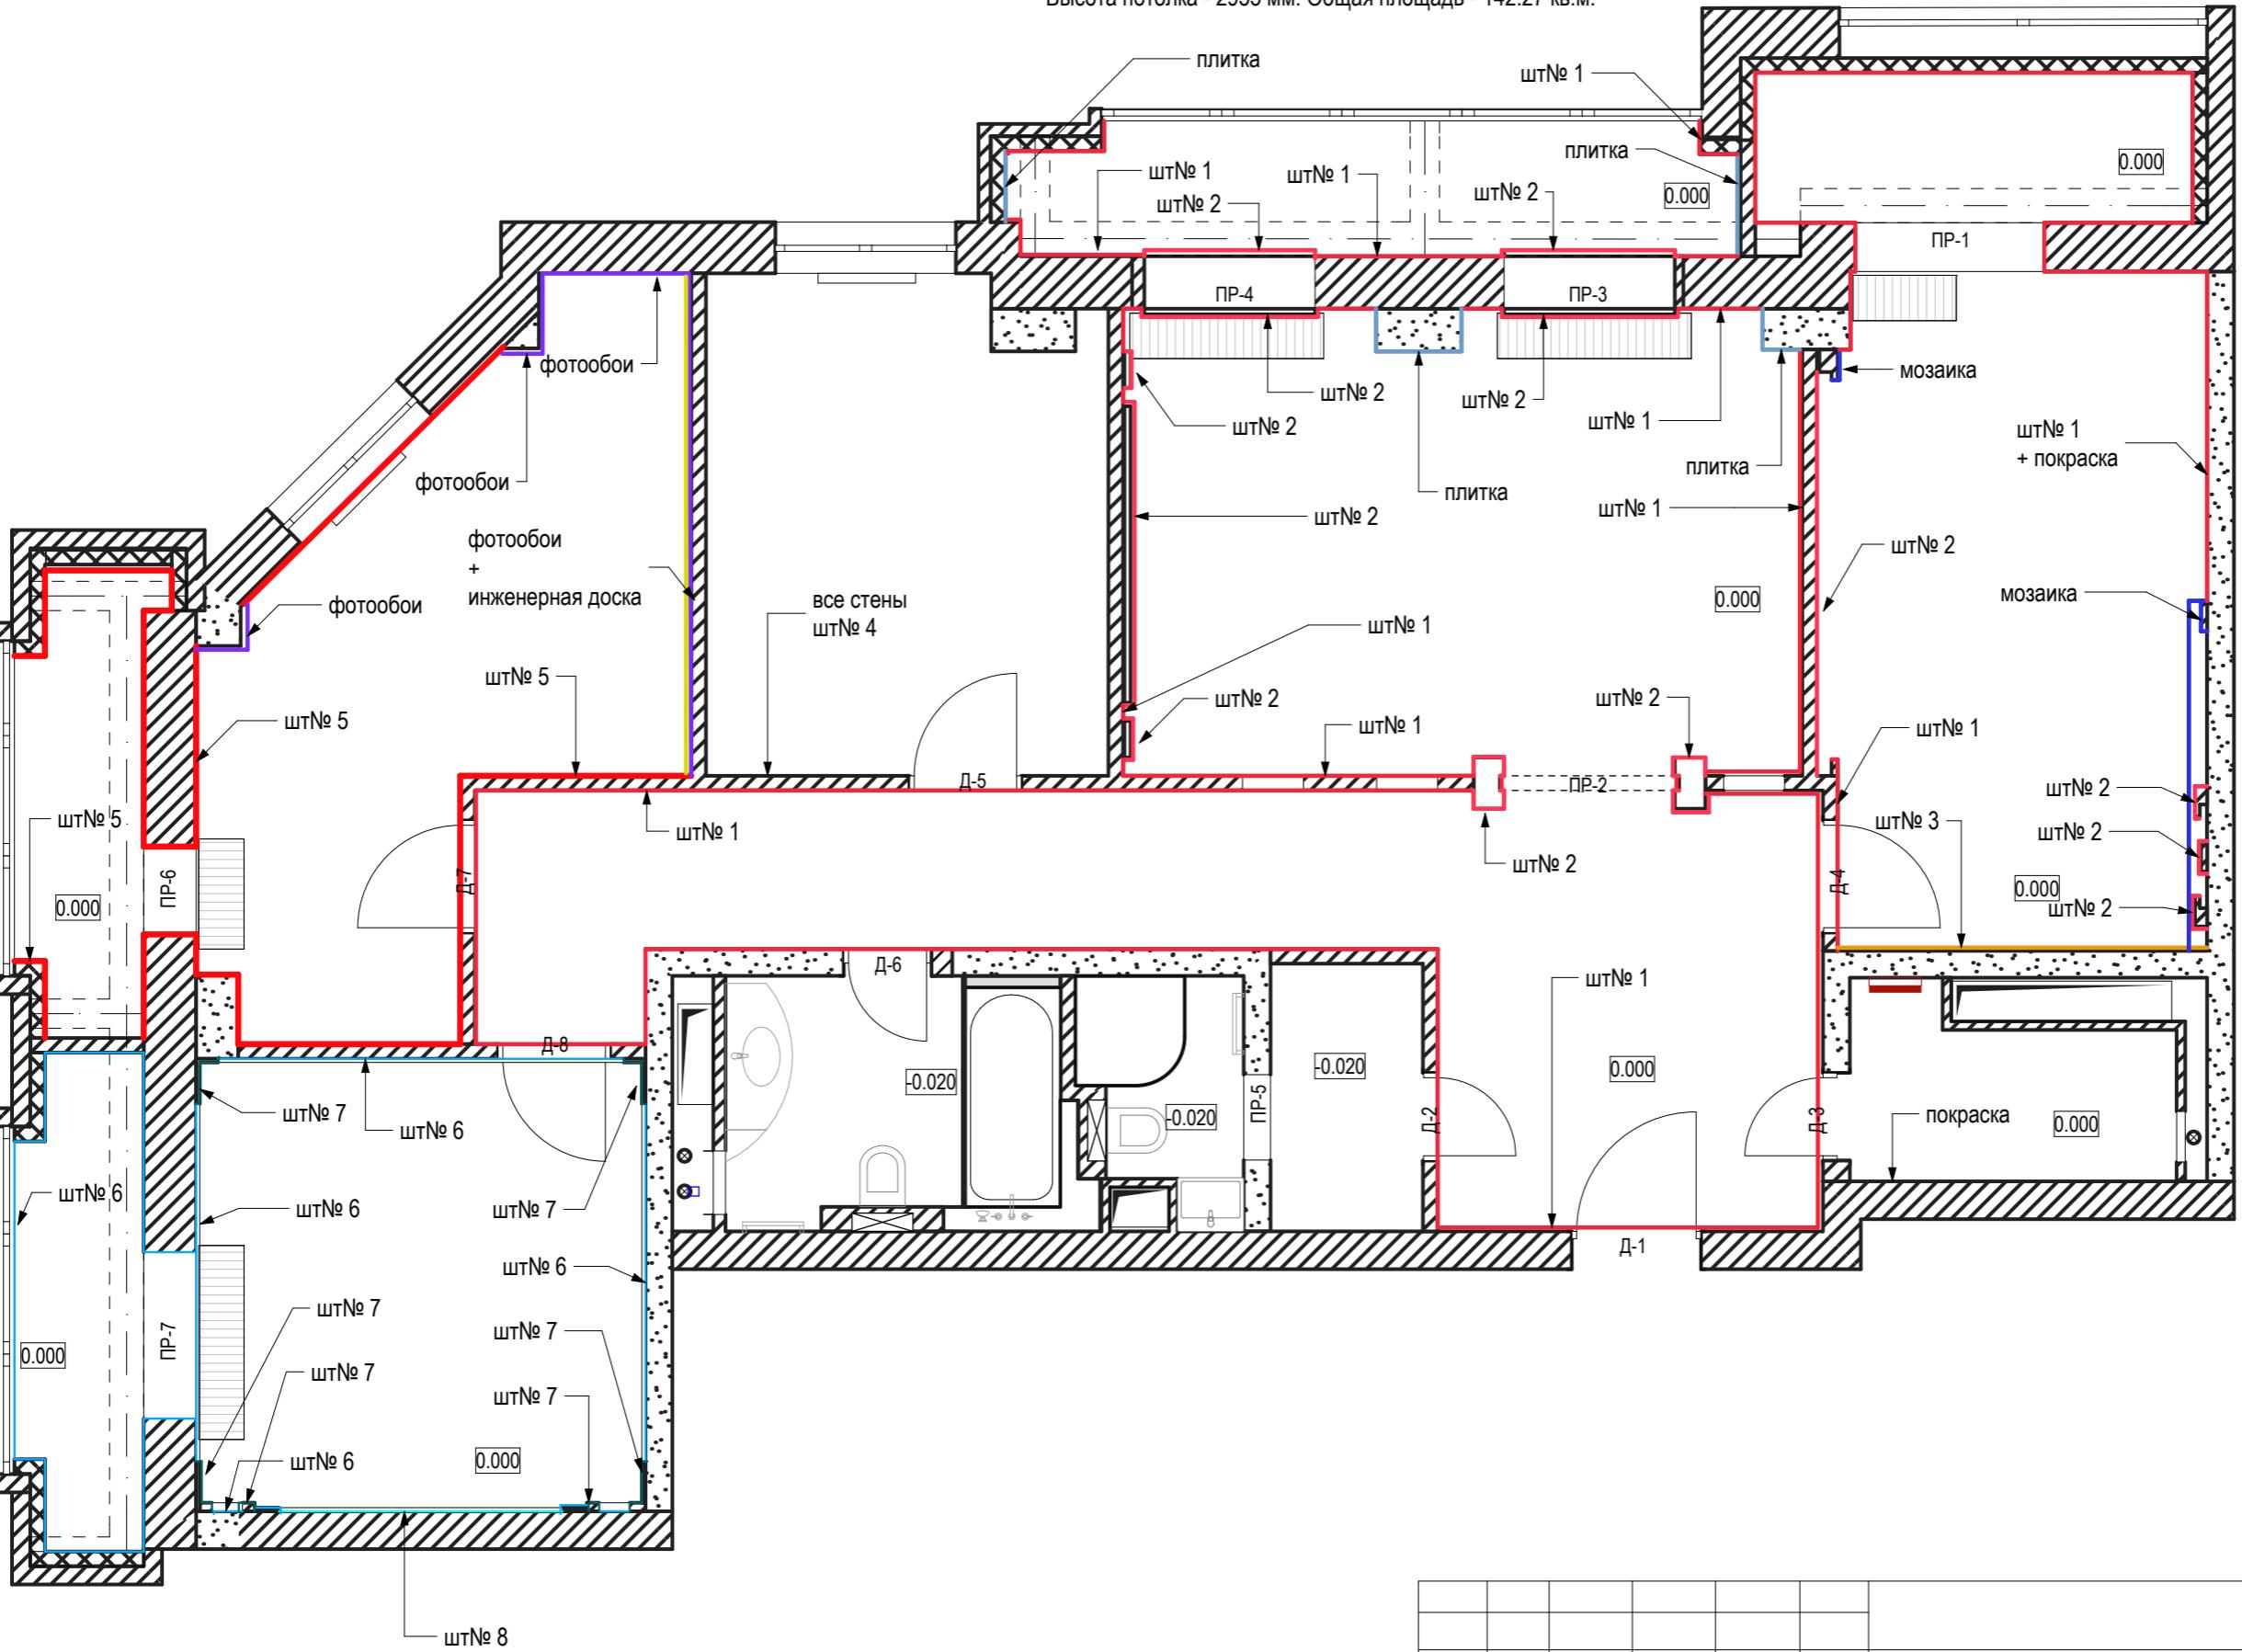

Изм.	Кол.уч	Лист	№ док	Подп.	Дата	Заказчик:	Стадия	Лист	Листов
Разработал									
ГАП									
ГИП									
Чертит									
Дата изменения									
Заказчик									

План отделочных материалов

Ведомость отделочных материалов 1

№ пп	Наименование помещения	ПОТОЛОК		СТЕНЫ		ДЕКОРАТИВНЫЕ ЭЛЕМЕНТЫ		ПОЛЫ	
		площадь м ²	вид отделки	площадь м ²	вид отделки	кол-во шт./м.п	вид отделки	площадь м ²	вид отделки
1	Холл	12,23 6,09 4,95	Потолок из ГКЛ Штукатурка, покраска Витраж "Стекло и мир" Проезд Серебрякова/ 8-916-841-87-87	70,88	Декоративная штукатурка 1 Фактура 27.02.15.01 цвет 22.01.16.01 "РЭМдекор" Скаковая 36. 8-903-561-88-16			7,64 16,25	Керамогранит ф-ка Peronda Candela цвет CANDELA/44/P размер 440x440 "СтудиоЛайн" Нахимовский 30 Инженерная доска FINEX/Фиочки/ 185x500/2400x16 "Файнекс" Сретенский бульвар, д. 6/1, стр. 1.
2	Гардеробная	3,81	Штукатурка, покраска	23,86	Покраска			3,81	Керамогранит фабрика Tagina коллекция Fucina цвет Grigio размер 600x600 "СтудиоЛайн" Нахимовский 30
3	Кухня	8,89	Штукатурка, покраска	15,88 11,41 8,42 2,42 6,65 2,71	Декоративная штукатурка 1 Фактура 27.02.15.01 цвет 22.01.16.01 Декоративная штукатурка 2 Фактура струдо скин цвет серый Декоративная штукатурка 3 Фактура 29.05.15.01 цвет под фасад кухни "РЭМдекор" Скаковая 36. 8-903-561-88-16 Фартук кухни Покраска за мебелью Мозаика Фабрика Dune 184330 2.5X2.5 VITRA MOSAICO PLATINO BRILL D910 290x290 "СтудиоЛайн" Нахимовский 30			11,16 4,74 1,64	Инженерная доска FINEX/Фиочки/ 185x500/2400x16 "Файнекс" Сретенский бульвар, д. 6/1, стр. 1. Керамогранит фабрика Tagina коллекция Fucina цвет Nero размер 600x600 Мозаика Фабрика Dune 184330 2.5X2.5 VITRA MOSAICO PLATINO BRILL D910 290x290 "СтудиоЛайн" Нахимовский 30
4	Лоджия 1	4,51	Утепленный потолок и балки	19,38	Декоративная штукатурка 1 Фактура 27.02.15.01 цвет 22.01.16.01 "РЭМдекор" Скаковая 36. 8-903-561-88-16			4,68	Керамогранит фабрика Tagina коллекция Fucina цвет Grigio размер 600x600 "СтудиоЛайн" Нахимовский 30
5	Гостиная	8,43 14,24	Потолок из ГКЛ Штукатурка, покраска	30,64 13,94 5,72	Декоративная штукатурка 1 Фактура 27.02.15.01 цвет 22.01.16.01 Декоративная штукатурка 2 Фактура струдо скин цвет серый Керамогранит ф-ка Peronda Candela цвет CANDELA/44/P размер 440x440 "СтудиоЛайн" Нахимовский 30			20,83	Инженерная доска FINEX/Фиочки/ 185x500/2400x16 "Файнекс" Сретенский бульвар, д. 6/1, стр. 1.
6	Лоджия 2	6,38	Утепленный потолок и балки	14,60 3,82	Декоративная штукатурка 1 Фактура 27.02.15.01 цвет 22.01.16.01 "РЭМдекор" Скаковая 36. 8-903-561-88-16 Керамогранит ф-ка Peronda Candela цвет CANDELA/44/P размер 440x440 "СтудиоЛайн" Нахимовский 30			7,64	Керамогранит ф-ка Peronda Candela цвет CANDELA/44/P размер 440x440 "СтудиоЛайн" Нахимовский 30

Согласовано

Изв. № подп.	Подп. и дата	Взам. инд. №
--------------	--------------	--------------

Изм.	Кол.уч	Лист	№ док	Подп.	Дата	Заказчик:			
Разработал						Адрес:			
ГАП						Стадия			
ГИП						Лист			
Чертил						Листов			
Дата изменения						Ведомость отделочных материалов 1			
Заказчик									

P

31

34

Ведомость отделочных материалов 2

№ пп	Наименование помещения	ПОТОЛОК		СТЕНЫ		ДЕКОРАТИВНЫЕ ЭЛЕМЕНТЫ		ПОЛЫ	
		площадь м ²	вид отделки	площадь м ²	вид отделки	кол-во шт./м.п	вид отделки	площадь м ²	вид отделки
7	Детская 1	6,91 6,17	Потолок из ГКЛ Штукатурка, покраска	38,72	Декоративная штукатурка 4 Лучера 31.03.14.02 цвет G343+перламутр "РЭМдекор" Скаковая 36. 8-903-561-88-16			13,18	Инженерная доска FINEX/Фиоччи/ 185x500/2400x16 "Файнекс" Сретенский бульвар, д. 6/1, стр. 1.
8	Детская 2	12,79 3,62	Потолок из ГКЛ Штукатурка, покраска	29,87 8,48 9,50	Декоративная штукатурка 5 Бетон 15.12.15.01 "РЭМдекор" Скаковая 36. 8-903-561-88-16 Фото обои "Pitera" Конный пер. 4/ 8-495-690-9999 доб. 392 Инженерная доска FINEX/Фиоччи/ 185x500/2400x16 "Файнекс" Сретенский бульвар, д. 6/1, стр. 1.			16,17	Инженерная доска FINEX/Фиоччи/ 185x500/2400x16 "Файнекс" Сретенский бульвар, д. 6/1, стр. 1.
9	Лоджия 3	4,17		22,03	Декоративная штукатурка 5 Бетон 15.12.15.01 "РЭМдекор" Скаковая 36. 8-903-561-88-16			4,16	Керамогранит фабрика Tagina коллекция Fucina цвет Grigio размер 600x600 "СтудиоЛайн" Нахимовский 30
10	Спальня	7,51 5,69	Потолок из ГКЛ Штукатурка, покраска	19,75 9,93 5,34	Декоративная штукатурка 6 Светлый 04.07.15.03 шелк Декоративная штукатурка 7 Серый шелк H488 Декоративная штукатурка 8 Пано листья без желтого "РЭМдекор" Скаковая 36. 8-903-561-88-16			13,20	Керамогранит/ Peronda "Керамистика" Нахимовский 30
11	Лоджия 4	4,58	Утепленный потолок и балки	20,16	Декоративная штукатурка 6 Светлый 04.07.15.03 шелк "РЭМдекор" Скаковая 36. 8-903-561-88-16			4,56	Керамогранит фабрика Tagina коллекция Fucina цвет Grigio размер 600x600 "СтудиоЛайн" Нахимовский 30
12	Санузел 1	5,94	Потолок из ГКЛ	29,51	Керамогранит Фабрика Versace коллекция Gold "СтудиоЛайн" Нахимовский 30			5,25	Керамогранит Фабрика Versace коллекция Gold "СтудиоЛайн" Нахимовский 30
13	Санузел 2	2,36 2,74	Потолок из ГКЛ Штукатурка, покраска	34,80	Керамогранит Фабрика Importa Ceramiche коллекция Shine "СтудиоЛайн" Нахимовский 30			5,35	Керамогранит Фабрика Importa Ceramiche коллекция Shine "СтудиоЛайн" Нахимовский 30

Согласовано


Ззам. инд. №

Подп. и дата

Инв. № подп.

Приложение 1. Монтажные схемы сантехники

Высота потолка - 2955 мм. Общая площадь - 142.27 кв.м.

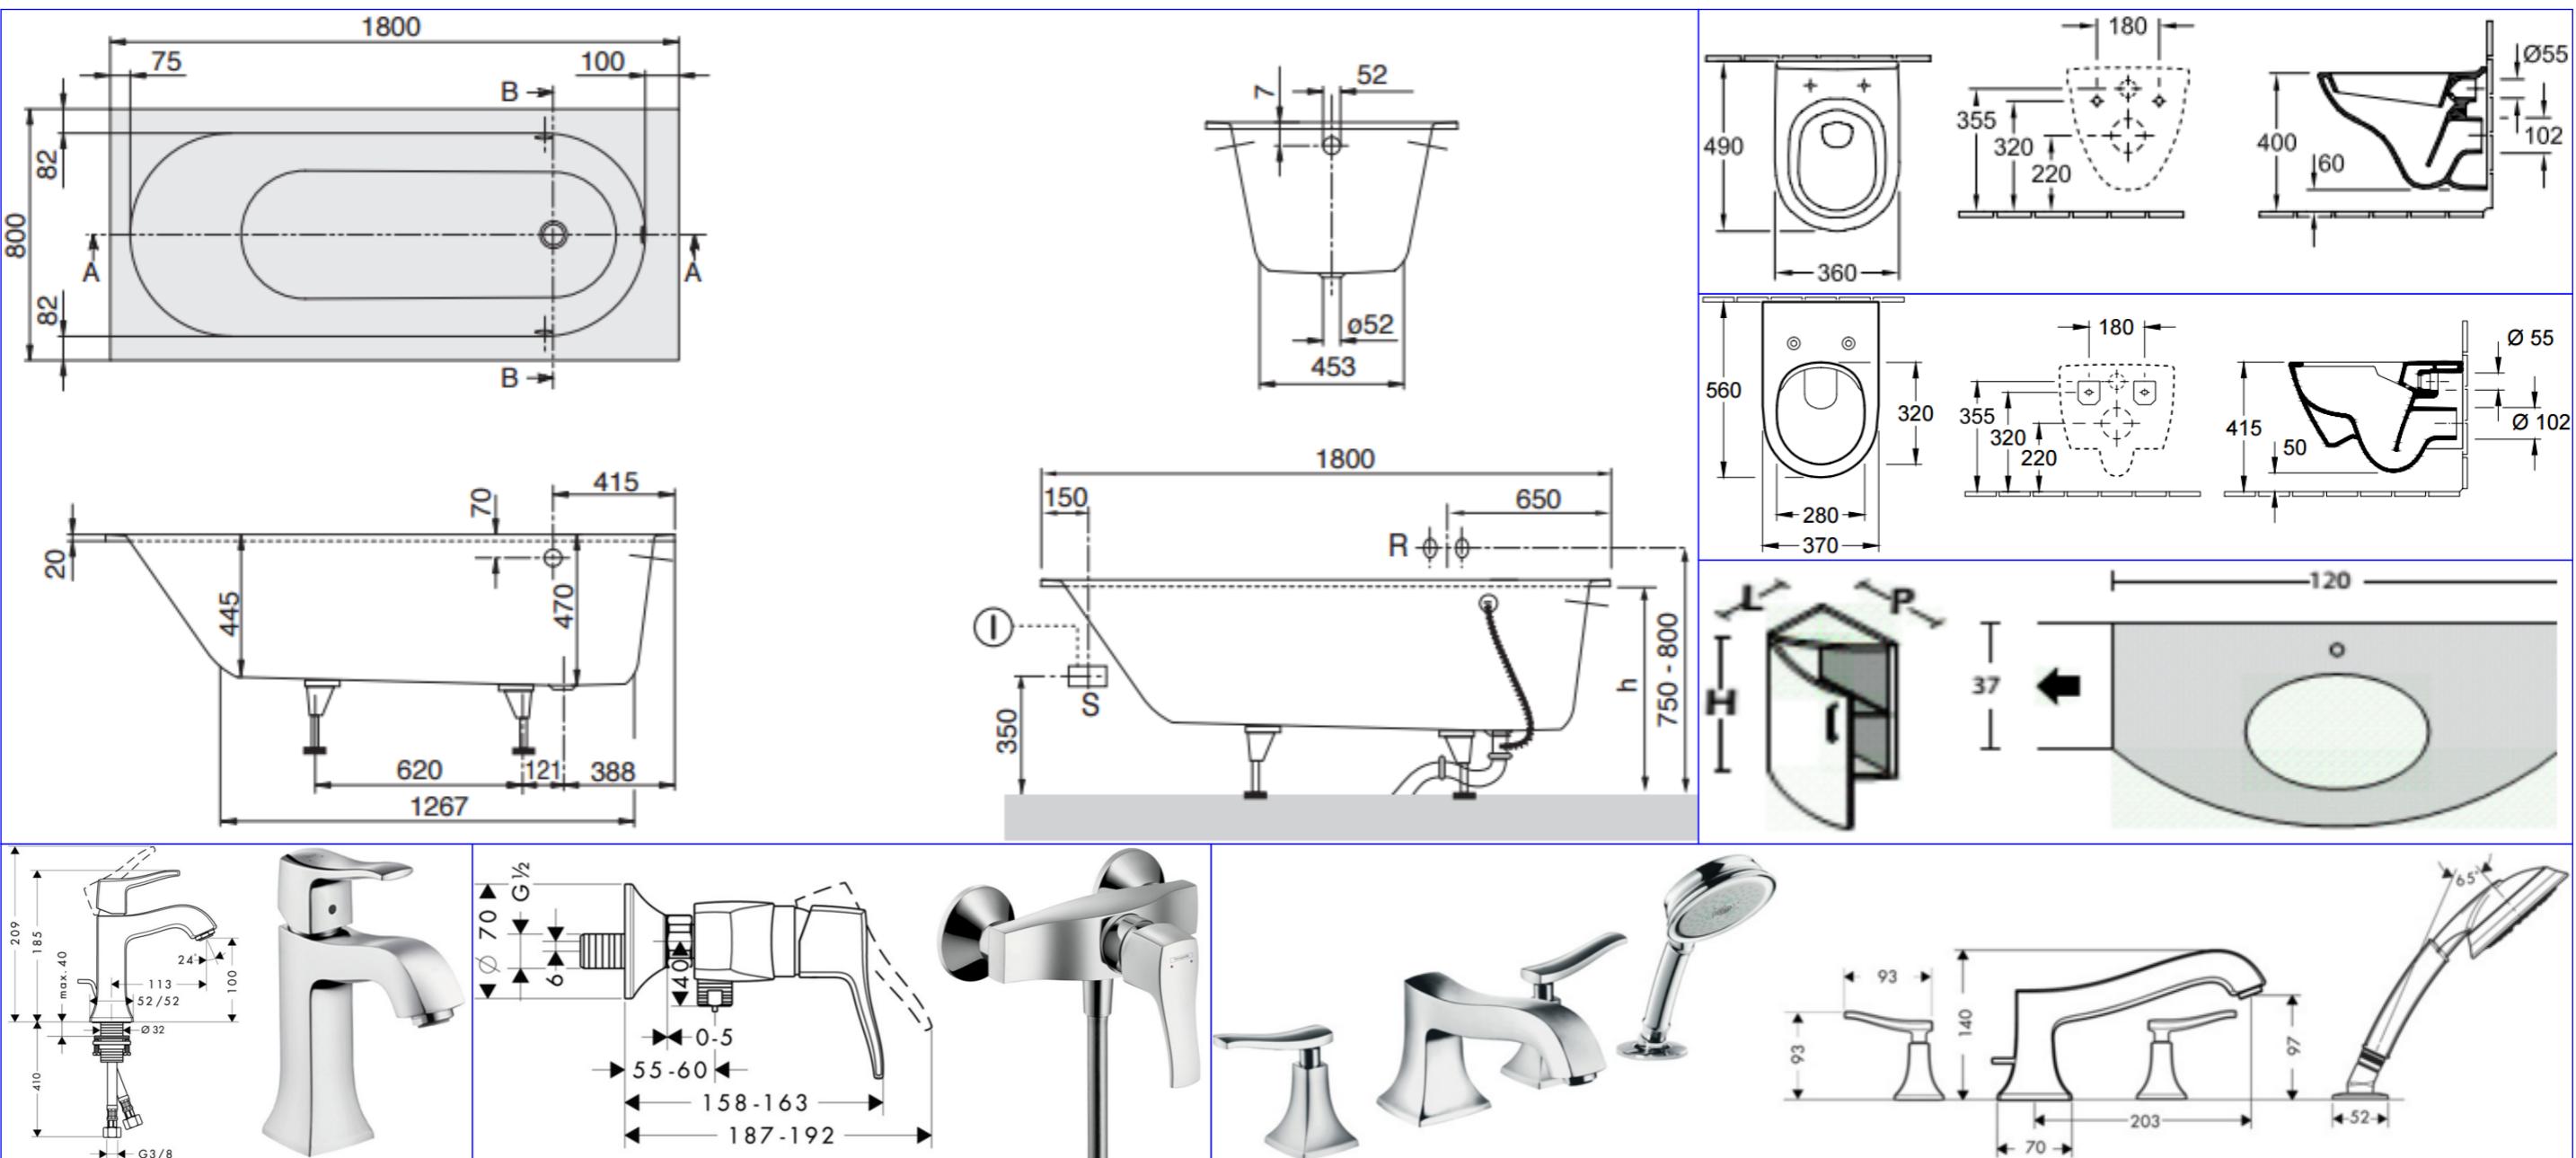


Согласовано			

Инв. № подл.	Подл. и дата	Взам. инд. №

Изм.	Кол.уч	Лист	№ док	Подп.	Дата	Заказчик:	Стадия	Лист	Листов
Разработал									
ГАП						Адрес:			
ГИП						P	33	34	
Чертит									
Дата изменения									
Заказчик									

Приложение 2. Монтажные схемы кухни
Высота потолка - 2955 мм. Общая площадь - 142.27 кв.м.

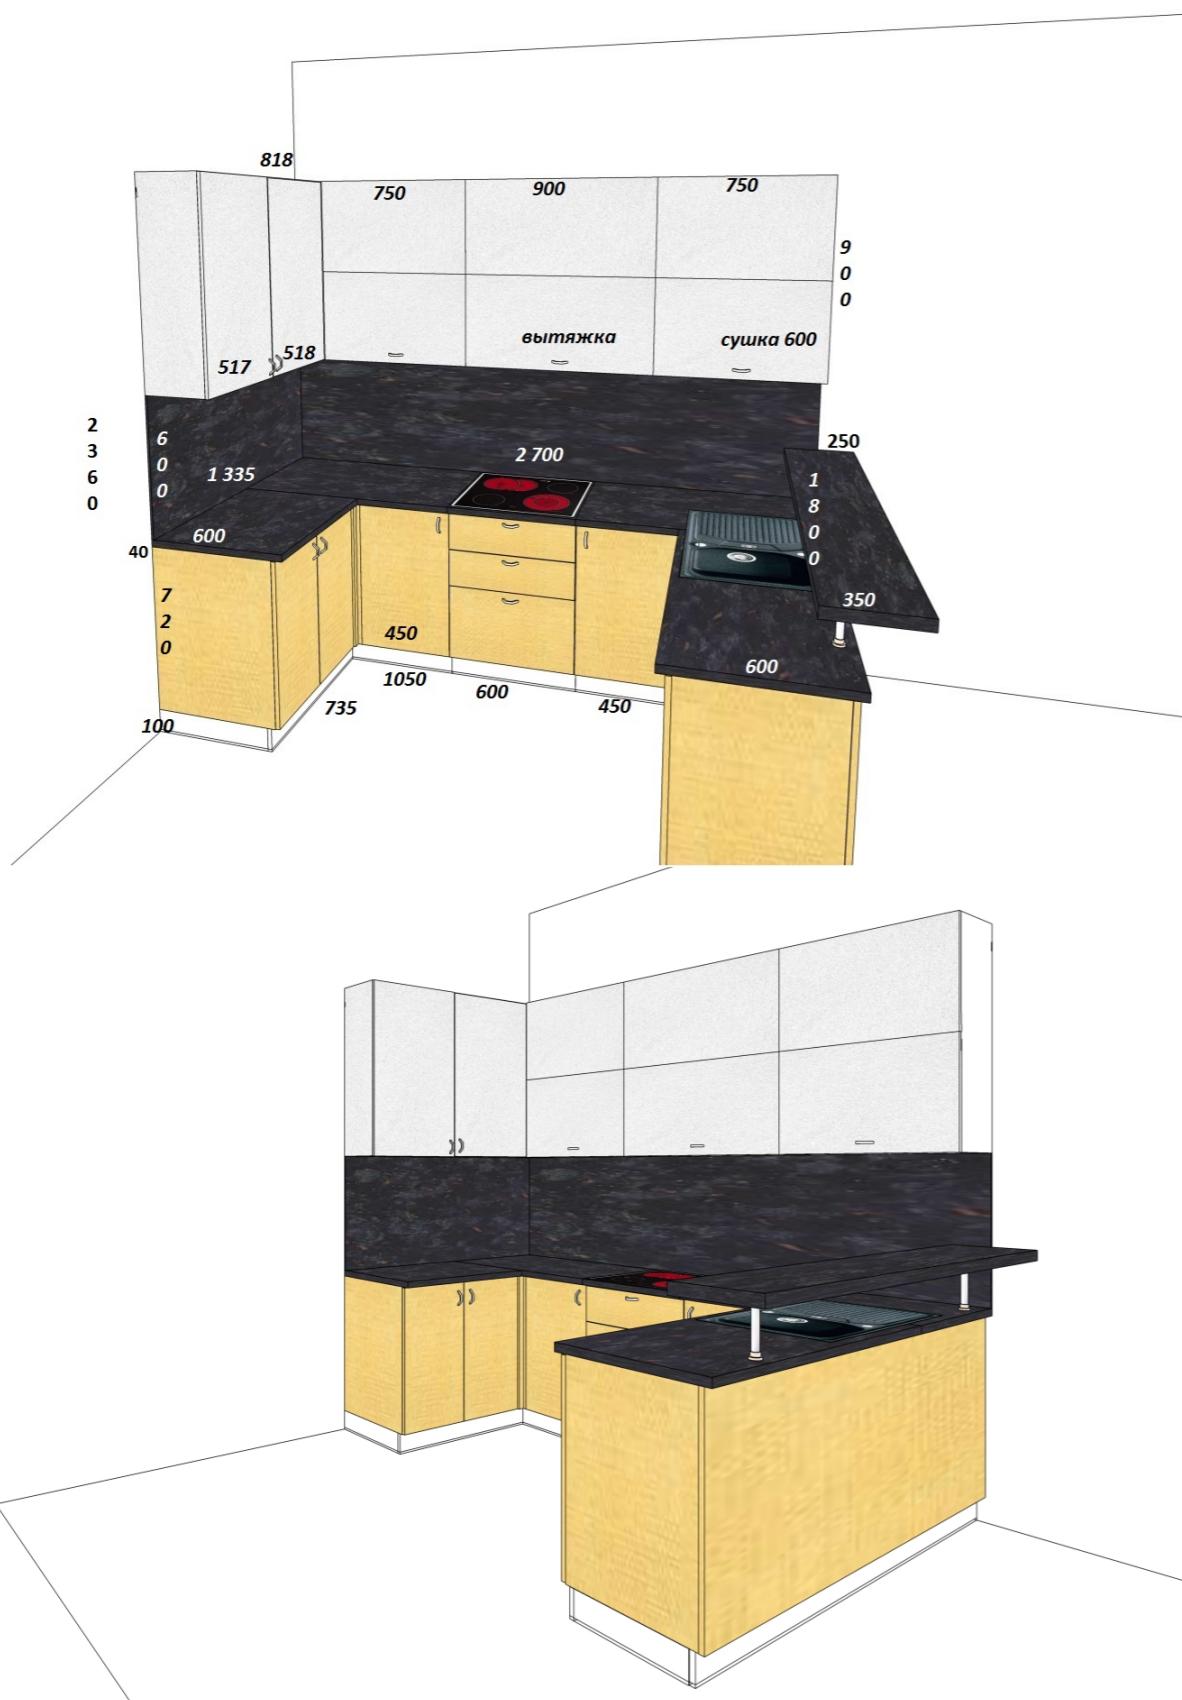

Согласовано		

Изм.	Кол.уч	Лист	№ док	Подп.	Дата	Заказчик:	Стадия	Лист	Листов
Разработал						Адрес:			
ГАП									
ГИП									
Чертит									
Дата изменения						Приложение 2. Монтажные схемы кухни			
Заказчик									
P	34	34							